

Фізична особа-підприємець - Никифорець І.І.  
ГІП Зіньків А. Б. - Кваліфікаційний сертифікат АР №018965  
ГАП Головецький Н. Я. - Кваліфікаційний сертифікат АА №001873

ПРОЕКТ:  
НОВЕ БУДІВНИЦТВО БАГАТОКВАРТИРНОГО ЖИТЛОВОГО БУДИНКУ З  
ПРИМІЩЕННЯМИ ГРОМАДСЬКОГО ПРИЗНАЧЕННЯ, ЗА АДРЕСОЮ: ПЛ.  
АВІАЦІЇ, 19Б, М. НОВИЙ КАЛИНІВ, САМБІРСЬКИЙ РАЙОН,  
ЛЬВІВСЬКА ОБЛАСТЬ.

Замовник: Товариство з обмеженою відповідальністю ОК ЖБК «Грінхауз Калинів»

Том 2

АРХІТЕКТУРНІ РІШЕННЯ  
ОСНОВНІ КРЕСЛЕННЯ

04-01/24 - АР




Фізична особа підприємець



І. І. Никифорець

Головний архітектор проекту

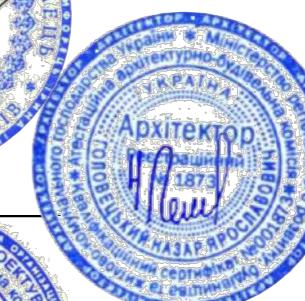

Н. Я. Головецький

Головний інженер проекту



А. Б. Зіньків

## Перелік креслень основного комплекту АР

| Аркуш | Найменування   | Марка |
|-------|--|-------|
| 1     | Перелік креслень.  | АР    |
| 2     | Загальні дані. Техніко-економічні показники.                                     | АР    |
| 3     | Схема генерального плану. М1:500.  | ГП    |
| 4     | План підземного поверху на відм. -3,060. М1:100                                  | АР    |
| 5     | Експлікація приміщень підземного поверху.  | АР    |
| 6     | План першого поверху на відм. ±0,000. М1:100                                     | АР    |
| 7.1   | Експлікація квартир 1 поверху. Секція №1 (Квартири 1-47)                         | АР    |
| 7.2   | Експлікація комерційних приміщень громадського призначення 1 поверху. Секція №2. | АР    |
| 8     | План 2 поверху на відм. +3,750. М1:100   | АР    |
| 9     | Експлікація квартир 2 поверху. Секція №1 (Квартири 1-47)                         | АР    |
| 10    | Експлікація квартир 2 поверху. Секція №2 (Квартири 48-82)                        | АР    |
| 11    | План 3 поверху на відм. +6,750. М1:100   | АР    |
| 12    | Експлікація квартир 3 поверху. Секція №1 (Квартири 1-47)                         | АР    |
| 13    | Експлікація квартир 3 поверху. Секція №2 (Квартири 48-82)                        | АР    |
| 14    | План 4 поверху на відм. +9,750. М1:100   | АР    |
| 15    | Експлікація квартир 4 поверху. Секція №1 (Квартири 1-47)                         | АР    |
| 16    | Експлікація квартир 4 поверху. Секція №2 (Квартири 48-82)                        | АР    |
| 17    | План 5 поверху на відм. +12,750. М1:100  | АР    |
| 18    | Експлікація квартир 5 поверху. Секція №1 (Квартири 1-47)                         | АР    |

## Перелік креслень основного комплекту АР

| Аркуш | Найменування  | Марка |
|-------|---|-------|
| 19    | Експлікація квартир 5 поверху. Секція №2 (Квартири 48-82) | АР    |
| 20    | План 6 поверху на відм. +15,750. М1:100                   | АР    |
| 21    | Експлікація квартир 6 поверху. Секція №1 (Квартири 1-47)  | АР    |
| 22    | Експлікація квартир 6 поверху. Секція №2 (Квартири 48-82) | АР    |
| 23    | План покрівлі на відм. +18,980 М1:100                     | АР    |
| 24    | Фасад в осіах 1-28. М1:100                                | АР    |
| 25    | Фасад в осіах 28-1. М1:100                                | АР    |
| 26    | Фасад в осіах А-Н. Фасад в осіах Н-А М1:100               | АР    |
| 27    | Розріз 1-1 М1:100   | АР    |
| 28    | Розріз 2-2 М1:100   | АР    |
| 29    | Розріз 3-3 М1:100   | АР    |
| 30    | Розріз 4-4 М1:100   | АР    |
| 31    | Розгортка вентиляційних каналів М1:50                     | АР    |
| 32    | Розгортка вентиляційних каналів М1:50                     | АР    |
| 33    | Розгортка вентиляційних каналів М1:50                     | АР    |
| 34    | Розгортка вентиляційних каналів М1:50                     | АР    |
| 35    | Розгортка вентиляційних каналів М1:50                     | АР    |
| 36    | Розгортка вентиляційних каналів М1:50                     | АР    |

|           |        |      |       |        |      |          |    |
|-----------|--------|------|-------|--------|------|----------|----|
| змін      | кільк. | арк. | №док. | підпис | дата | 04-01/24 | АР |
| ГП        |        |      |       |        |      |          |    |
| ГАП       |        |      |       |        |      |          |    |
| Виконав   |        |      |       |        |      |          |    |
| Перевірив |        |      |       |        |      |          |    |

Нове будівництво багатоквартирного житлового будинку з приміщеннями громадського призначення, за адресою: пл. Авіації, 196, м. Новий Калинів, Самбірський район, Львівська область.

Багатоквартирний житловий будинок  
м. Новий Калинів, Львівська область.  
1 черга будівництва.

Перелік креслень.

ФОП Никифорець І.І.

## Загальні дані. Техніко-економічні показники.

- Даний проект виконано на підставі містобудівних умов і обмежень
- Даний розділ включає основні архітектурні та конструктивні рішення марки АР стадії П.
- За умовну відмітку 0.000 прийнято рівень чистої підлоги першого поверху.
- Основні техніко-економічні показники по будинку (1 черга будівництва):
  - Площа земельної ділянки – 0,8550 га.
  - Площа забудови – 1 132,6 м<sup>2</sup>
  - Відсоток забудови – 13,25 %
  - Поверховість – 6 поверхів.
  - Висота поверху – 2,40; 2,70; 2,75; 3,00; 3,45; м.
  - Кількість квартир – 82 (1К-38; 2К-39; 3К-5;)
  - Границя висота будинку – 22,45 м
  - Умовна висота будинку – 16,70 м
  - Загальна площа всіх приміщень – 6 603,88 м<sup>2</sup>

В тому числі:

Площа квартир в будинку (без урах. літніх приміщень) – 4 113,17 м<sup>2</sup>

Площа літніх приміщень – 375,13 м<sup>2</sup>

Площа приміщень загального користування – 1 006,29 м<sup>2</sup>

Площа приміщень громадського призначення – 426,96 м<sup>2</sup>

Площа приміщень подвійного призначення – 228,62 м<sup>2</sup>

Площа інших нежитлових приміщень – 425,77 м<sup>2</sup>

Площа технічних приміщень – 27,94 м<sup>2</sup>

10) Загальна площа квартир – 4 488,3 м<sup>2</sup>

11) Житлова площа квартир – 1 723,01 м<sup>2</sup>

12) Площа житлового будинку – 7 336,20 м<sup>2</sup>

13) Будівельний об'єм – 29 164,45 м<sup>3</sup>, в тому числі:

вище ±0,000 – 25 426,87 м<sup>3</sup>

нижче ±0,000 – 3 737,58 м<sup>3</sup>

## 5. Основні техніко-економічні показники по генплану:

- Площа земельної ділянки – 0,4475 га.
- Площа забудови (в т.ч ТП) – 1 162,60 м<sup>2</sup>
- Площа замощення – 1 950,60 м<sup>2</sup>
- Площа дитячого майданчику – 121,00 м<sup>2</sup>
- Площа майданчику для відпочинку дорослого населення – 35,00 м<sup>2</sup>
- Площа майданчику для заняття фізкультурою – 35,00 м<sup>2</sup>
- Площа проїздів – 399,07 м<sup>2</sup>
- Площа озеленення – 771,73 м<sup>2</sup>
- Відсоток забудови – 25,98 %

## 6. Навантаження і фактори, прийняті для розрахунку конструкцій:

нормативне снігове навантаження 1400 Па (140 кгс/кв м)  
швидкісний напір вітру 530 Па (53 кгс/кв м)

\*інші нормативні навантаження згідно ДБН В.1.2-2-2006 у залежності від призначення приміщення

## 7. Клас будинку II

## 8. Вогнестійкість будинку II

9. Фундаменти – монолітна фундаментна плита.

10. Стіни по поверхові – керамічна цегла з зовнішнім утепленням, перегородки – цегляні.

11. Перекриття – монолітне залізобетонне.

12. Сходи – монолітні залізобетонні.

13. Дах – плоский, з рулонним покриттям. (Покрівля інверсійного типу)

14. Горизонтальну гідроізоляцію виконати з двох шарів гідроізолу на бітумній мастиці по вирівняній цементним розчином поверхні; Вертикальна гідроізоляція: Бокові поверхні фундаментів, що контактують з ґрунтом, загрунтувати холодною бітумною емульсією і покрити гарячим бітумом за 2 рази механізованим способом. Додатково по бітумній мастиці влаштувати шиповану мембрану і за необхідності геотекстиль.

## ПЕРЕЛІК ВИКОРИСТАНИХ НОРМАТИВНИХ ДОКУМЕНТІВ

| № | Найменування   | Позначення        |
|---|--|-------------------|
| 1 | Склад та зміст проектної документації на будівництво | ДБН А.2.2-3:2014  |
| 2 | Пожежна безпека об'єктів будівництва                 | ДБН В.1.1.7-2016  |
| 3 | Громадські будинки і споруди. Основні положення      | ДБН В.2.2-9:2018  |
| 4 | Житлові будинки. Основні положення                   | ДБН В.2.2-15:2019 |
| 5 | Планування і забудова територій.                     | ДБН Б.2.2-12:2019 |

Цей комплект креслень виготовлено у відповідності з діючими нормами і правилами  
(в тому числі по вибухо-пожежній безпеці)


Головний архітектор проекту Н. Головецький


|           |        |                |       |        |          |   |
|-----------|--------|----------------|-------|--------|----------|---|
|           |        |                |       |        | 04-01/24 | АР  |
| змін      | кільк. | арк.           | №док. | підпис | дата     | Нове будівництво багатоквартирного житлового будинку з приміщеннями громадського призначення, за адресою: пл. Авіації, 196, м. Новий Калинів, Самбірський район, Львівська область. |
| ГП        |        | Зіньків А.Б.   |       |        |          | Багатоквартирний житловий будинок м. Новий Калинів, Львівська область. 1 черга будівництва.   |
| ГАП       |        | Головецький Н. |       |        |          |   |
| Виконав   |        | Попелястий Р.  |       |        |          |   |
| Перевірив |        | Зіньків А.Б.   |       |        |          | Загальні дані. Техніко-економічні показники.  |
|           |        |                |       |        |          | ФОП Никифорець І.І.   |



# СХЕМА ГЕНЕРАЛЬНОГО ПЛАНУ

М 1:500

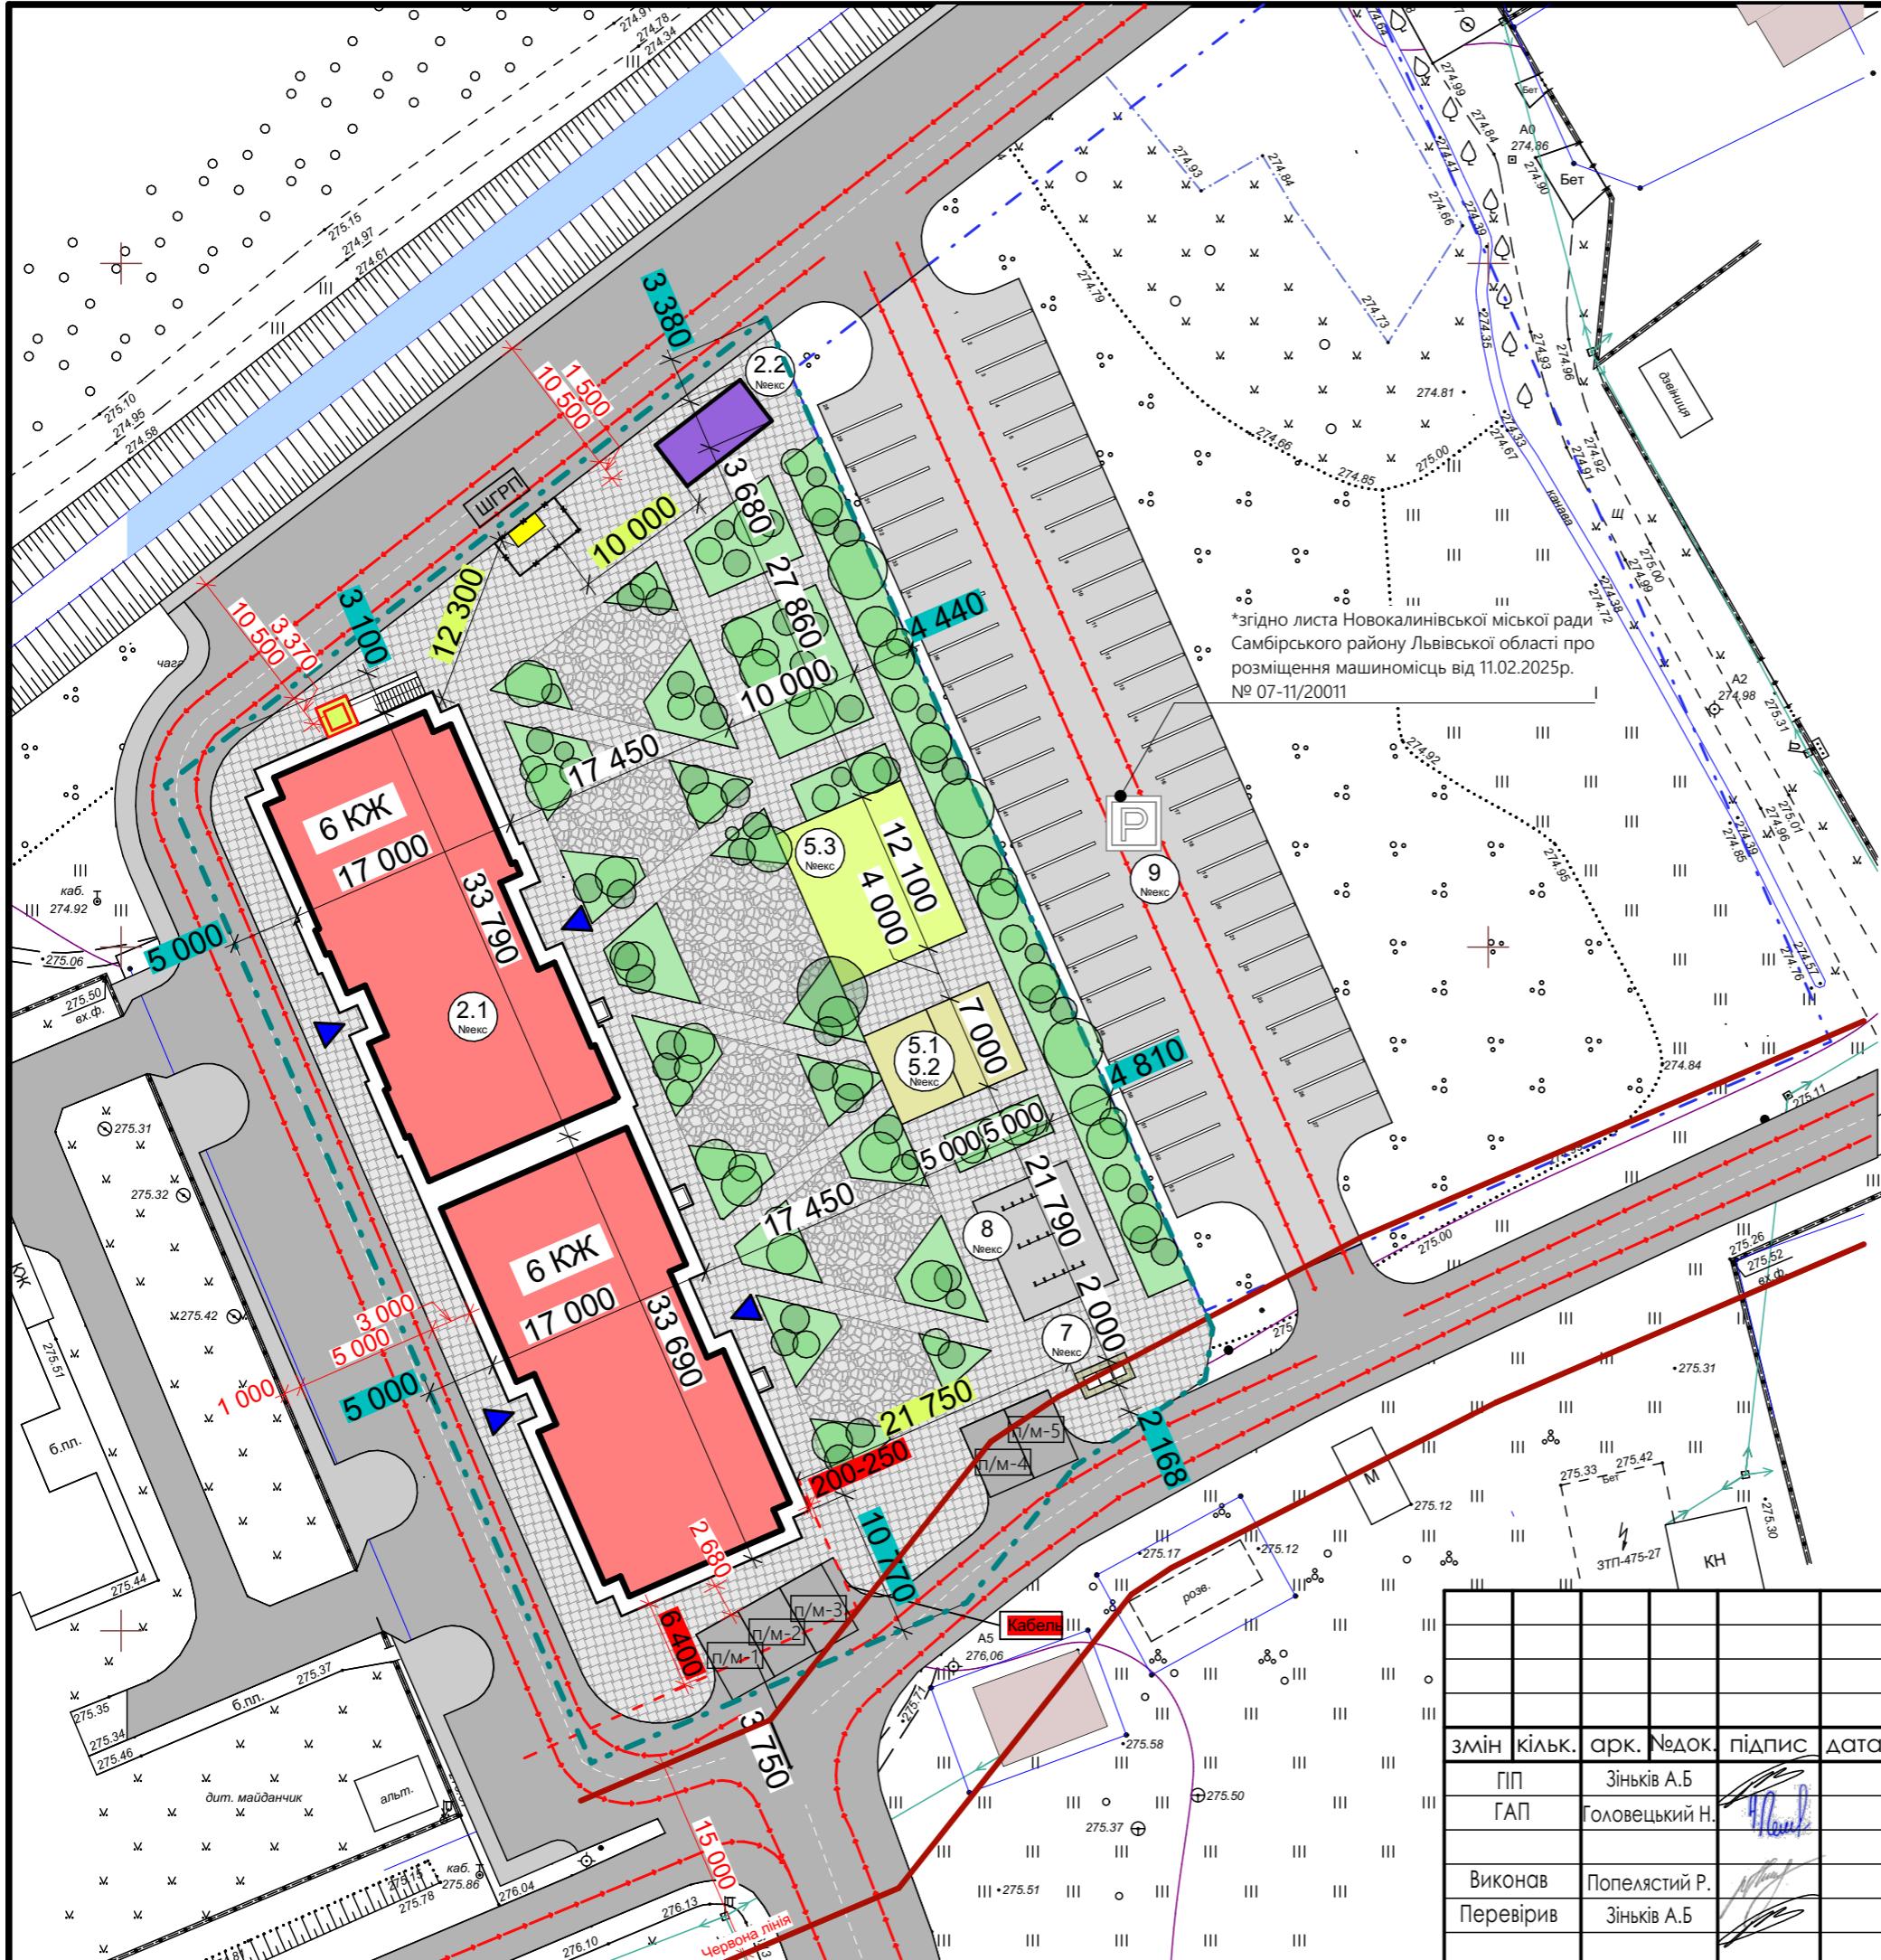

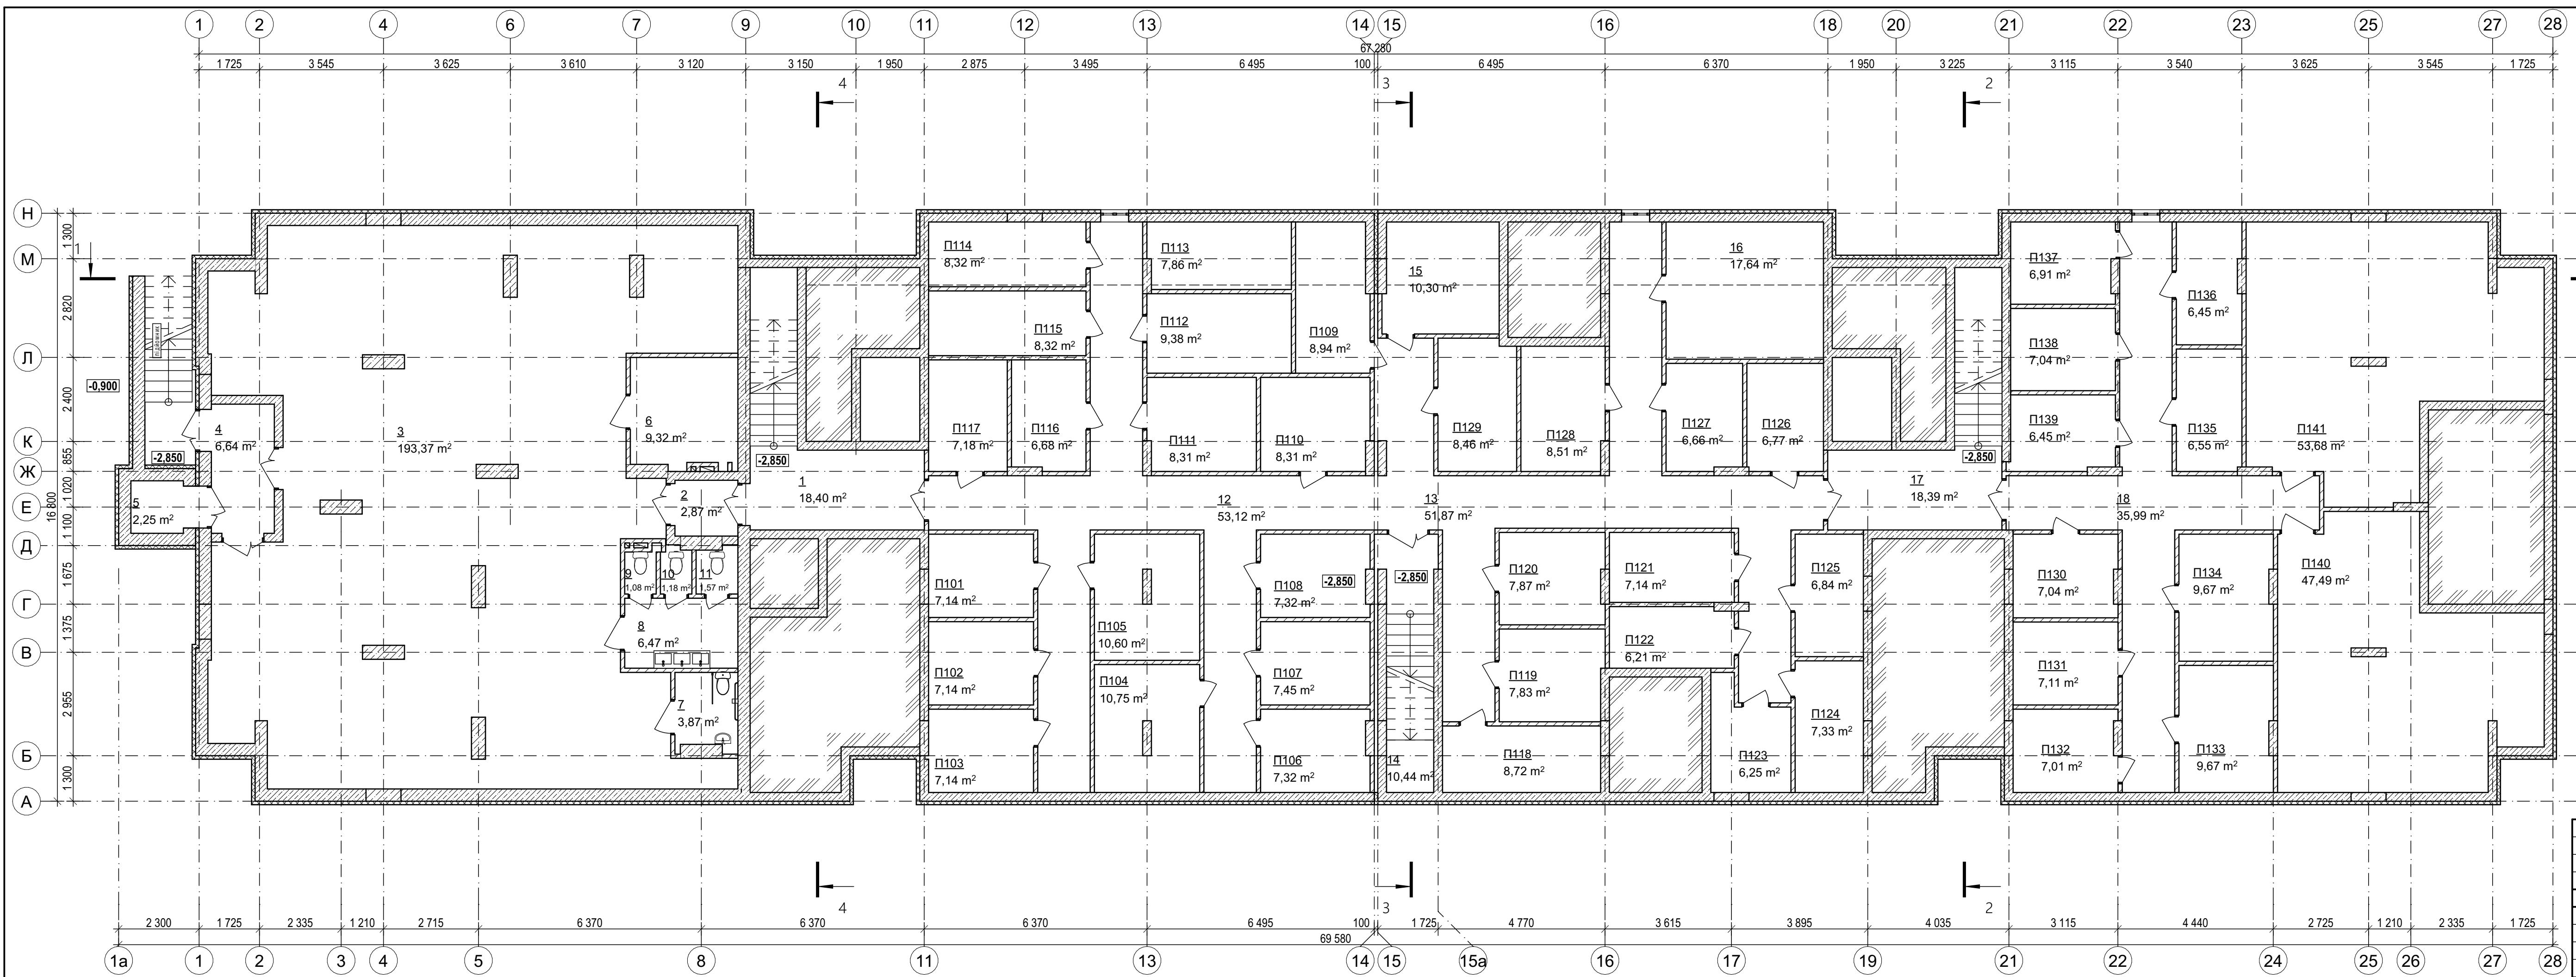


Експлікація приміщень

| №                         | Найменування | Площа, м <sup>2</sup>       |
|---------------------------|--------------|-----------------------------|
| <b>Секція 1</b>           |              |                             |
| П101                      | Комора       | 7,14                        |
| П102                      | Комора       | 7,14                        |
| П103                      | Комора       | 7,14                        |
| П104                      | Комора       | 10,75                       |
| П105                      | Комора       | 10,60                       |
| П106                      | Комора       | 7,32                        |
| П107                      | Комора       | 7,45                        |
| П108                      | Комора       | 7,32                        |
| П109                      | Комора       | 8,94                        |
| П110                      | Комора       | 8,31                        |
| П111                      | Комора       | 8,31                        |
| П112                      | Комора       | 9,38                        |
| П113                      | Комора       | 7,86                        |
| П114                      | Комора       | 8,32                        |
| П115                      | Комора       | 8,32                        |
| П116                      | Комора       | 6,68                        |
| П117                      | Комора       | 7,18                        |
| <b>Всього по секції 1</b> |              | <b>138,16 м<sup>2</sup></b> |

Експлікація приміщень

| №                         | Найменування | Площа, м <sup>2</sup>       |
|---------------------------|--------------|-----------------------------|
| <b>Секція 2</b>           |              |                             |
| П118                      | Комора       | 8,72                        |
| П119                      | Комора       | 7,83                        |
| П120                      | Комора       | 7,87                        |
| П121                      | Комора       | 7,14                        |
| П122                      | Комора       | 6,21                        |
| П123                      | Комора       | 6,25                        |
| П124                      | Комора       | 7,33                        |
| П125                      | Комора       | 6,84                        |
| П126                      | Комора       | 6,77                        |
| П127                      | Комора       | 6,66                        |
| П128                      | Комора       | 8,51                        |
| П129                      | Комора       | 8,46                        |
| П130                      | Комора       | 7,04                        |
| П131                      | Комора       | 7,11                        |
| П132                      | Комора       | 7,01                        |
| П133                      | Комора       | 9,67                        |
| П134                      | Комора       | 9,67                        |
| П135                      | Комора       | 6,55                        |
| П136                      | Комора       | 6,45                        |
| П137                      | Комора       | 6,91                        |
| П138                      | Комора       | 7,04                        |
| П139                      | Комора       | 6,45                        |
| П140                      | Приміщення 1 | 47,49                       |
| П141                      | Приміщення 2 | 53,68                       |
| <b>Всього по секції 2</b> |              | <b>263,66 м<sup>2</sup></b> |
| <b>Всього по коміркам</b> |              | <b>401,82</b>               |

|           |        |                |       |        |          |   |
|-----------|--------|----------------|-------|--------|----------|---|
|           |        |                |       |        | 04-01/24 | АР  |
| змін      | кільк. | арк.           | №док. | підпис | дата     | Нове будівництво багатоквартирного житлового будинку з приміщеннями громадського призначення, за адресою: пл. Авіації, 196, м. Новий Калинів, Самбірський район, Львівська область. |
| ГП        |        | Зіньків А.Б.   |       |        |          | Багатоквартирний житловий будинок   |
| ГАП       |        | Головецький Н. |       |        |          | м. Новий Калинів, Львівська область.  |
| Виконав   |        | Попелястий Р.  |       |        |          | 1 черга будівництва.  |
| Перевірив |        | Зіньків А.Б.   |       |        |          | Експлікація приміщень підземного поверху.   |
|           |        |                |       |        |          | ФОП Никифорець І.І.   |

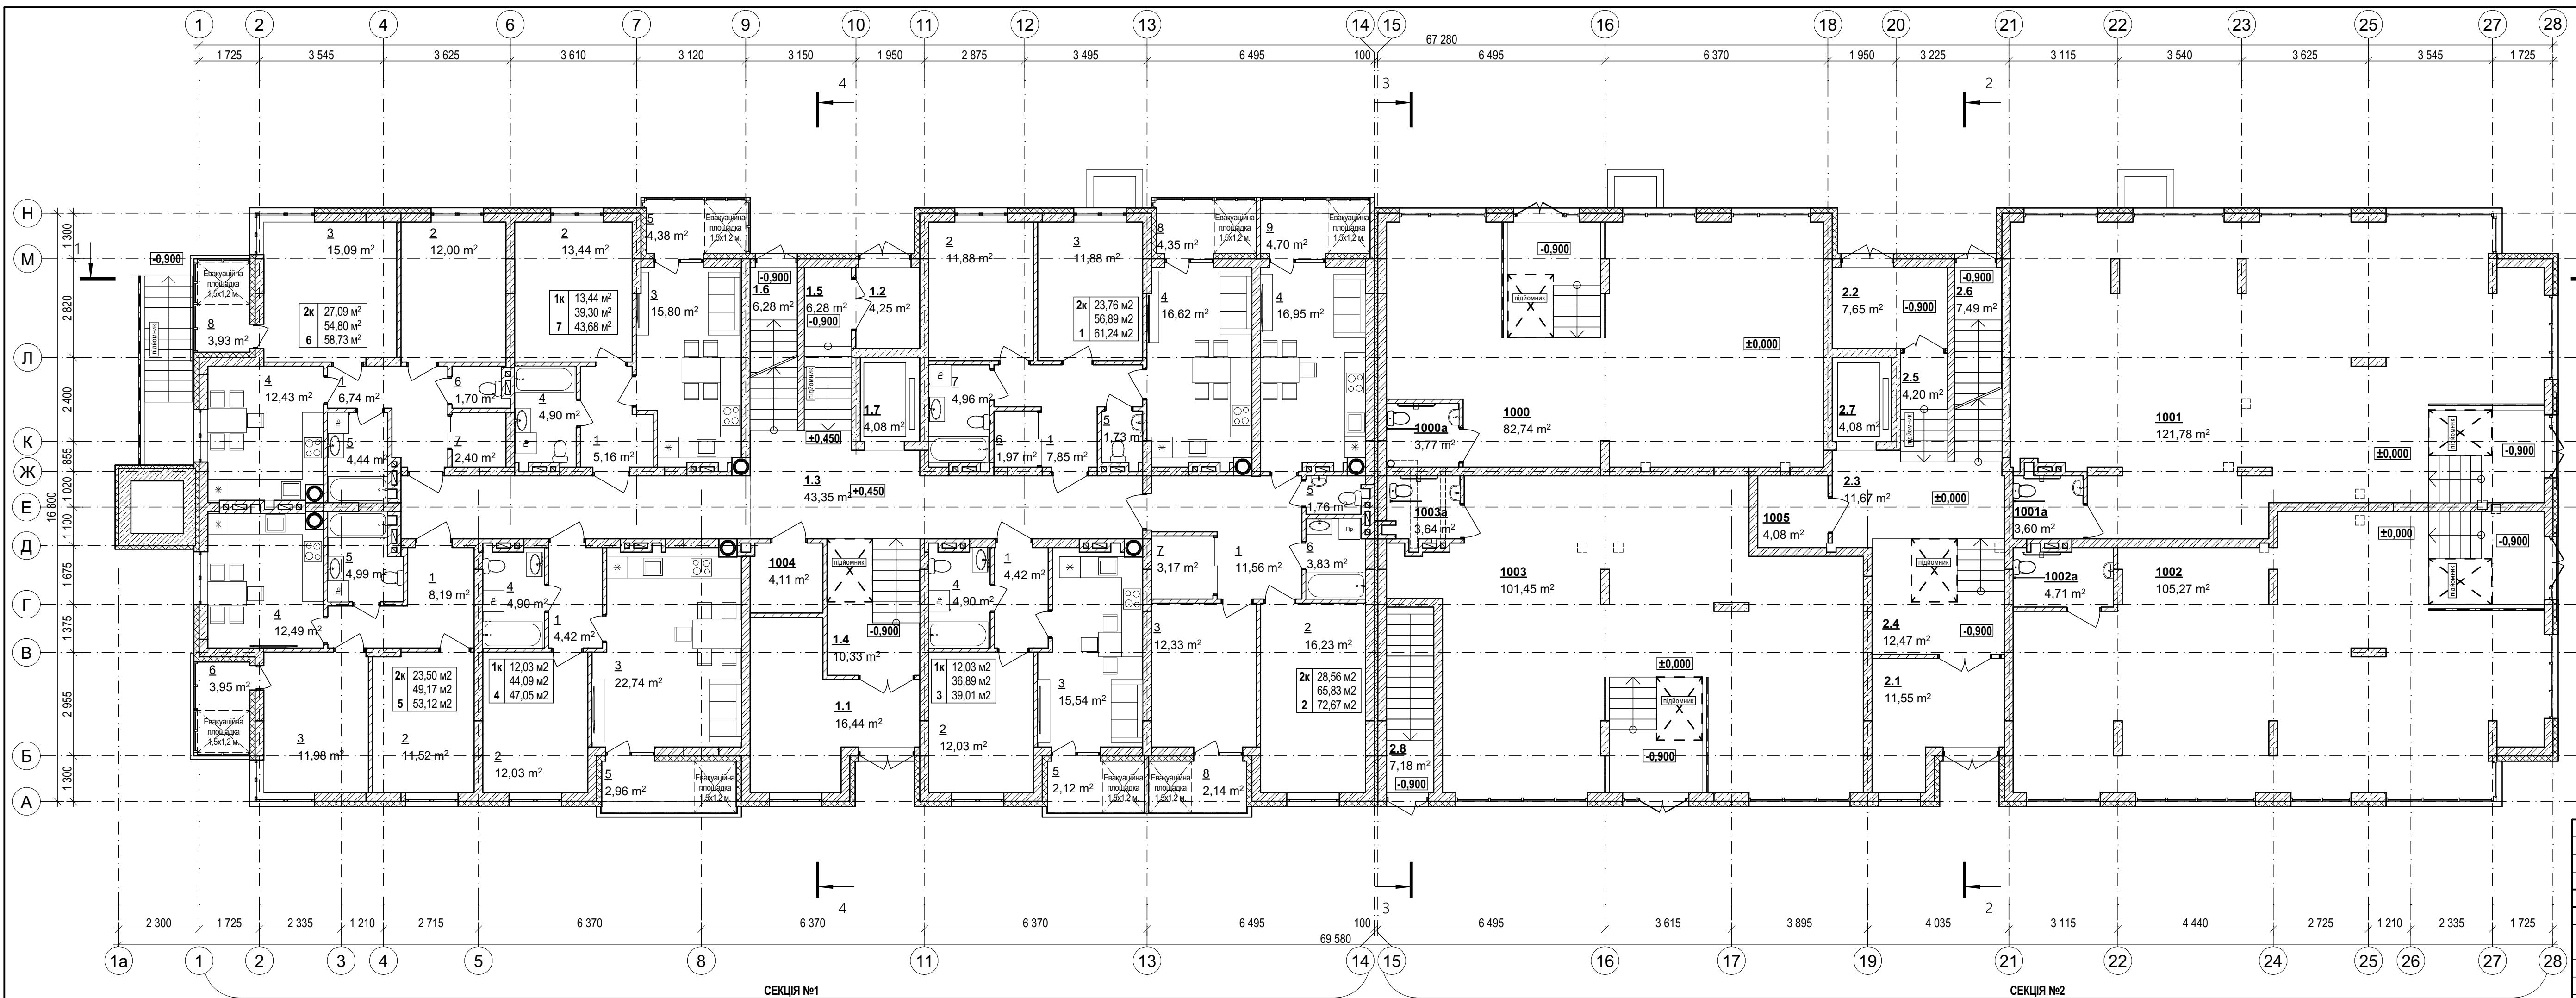

# Експлікація приміщень 1-го поверху

## Умовні позначення:

- з/б монолітна стіна з зовн. утепленням;
- з/б конструкції;
- Стіни з керамічної цегли з зовн. утепленням;
- Стіни з церамічної цегли.

| №   | Назва приміщення              | Площа        |
|---|-------------------------------|--------------|
| Приміщення загального користування                |                               |              |
| 1.1   | Тамбур-калясочна              | 100          |
| 1.2   | Тамбур                        | 40           |
| 1.3   | Коридор                       | 40           |
| 1.4   | Сходова клітка                | 100          |
| 1.5   | Сходова клітка                | 60           |
| 1.6   | Сходова клітка                | 60           |
| 1.7   | Шахта ліфта                   | 40           |
| <b>Разом по секції №1</b>                         |                               | <b>91,00</b> |
| 2.1   | Тамбур-калясочна              | 110          |
| 2.2   | Тамбур                        | 70           |
| 2.3   | Коридор                       | 110          |
| 2.4   | Сходова клітка                | 120          |
| 2.5   | Сходова клітка                | 40           |
| 2.6   | Сходова клітка                | 70           |
| 2.7   | Шахта ліфта                   | 40           |
| 2.8   | Сходова клітка                | 70           |
| <b>Разом по секції №2</b>                         |                               | <b>66,00</b> |
| 1004  | Підсобне приміщення Секція №1 | 40           |
| 1005  | Підсобне приміщення Секція №2 | 40           |
| Загальна площа приміщень загального користування  |                               |              |
| Загальна площа комор 1 поверху                    |                               |              |
| Загальна площа квартир 1 поверху                  |                               |              |
| Загальна площа приміщень громадського призначення |                               |              |
| <b>Загальна площа приміщень 1 поверху</b>         |                               |              |

## Примітки:

- Основні техніко-економічні показники та загальні дані див. арк. 2.
- За умовну відмітку 0,000 прийнято рівень чистої підлоги першого поверху (Секція №2).
- Фасади див. аркуш 24-26.
- Розрізи див. аркуш 27-30.
- Розгортки по вентиляційних каналах див. аркуш 31-36.
- Зовн. та внутрішні стіни виконані з керамічної цегли товщ. 250мм.
- Перегородки виконані з керамічної цегли товщ. 120мм.

04-01/24

Нове будівництво багатоквартирного житлового будинку  
приміщеннями громадського призначення, за адресою: пл.  
19б, м. Новий Калинів, Самбірський район, Львівська обл.

Багатоквартирний житловий будинок  
м. Новий Калинів, Львівська область.  
1 черга будівництва.

стадія аркуш аркуш

П

6

змін кільк. арк. №док. підпис дата

ГІП Зіньків А.Б.

ГАП Головецький Н.

Виконав Попелястий Р.

Перевірив Зіньків А.Б.

План первого поверху на відм. ±0,000. М1:100


ФОП Никифоров



Експлікація приміщень (Секція №2)

| №   | Назва приміщення      | Площа, м <sup>2</sup>       |
|---|-----------------------|-----------------------------|
| Приміщення громадського призначення               |                       |                             |
| 1000  | Комерційне приміщення | 82,74                       |
| 1000a   | Санвузол              | 3,77                        |
| Загальна площа приміщення - 1000                  |                       | <b>86,51</b>                |
| 1001  | Комерційне приміщення | 121,78                      |
| 1001a   | Санвузол              | 3,60                        |
| Загальна площа приміщення - 1001                  |                       | <b>125,38</b>               |
| 1002  | Комерційне приміщення | 105,27                      |
| 1002a   | Санвузол              | 4,71                        |
| Загальна площа приміщення - 1002                  |                       | <b>109,98</b>               |
| 1003  | Комерційне приміщення | 101,45                      |
| 1003a   | Санвузол              | 3,64                        |
| Загальна площа приміщення - 1003                  |                       | <b>105,09</b>               |
| Загальна площа приміщень громадського призначення |                       | <b>426,96 м<sup>2</sup></b> |

|   |        |                |       |        |      |  |                     |
|---|--------|----------------|-------|--------|------|--|---------------------|
|   |        |                |       |        |      | 04-01/24                                       | АР                  |
| Нове будівництво багатоквартирного житлового будинку з приміщеннями громадського призначення, за адресою: пл. Авіації, 19б, м. Новий Калинів, Самбірський район, Львівська область. |        |                |       |        |      |  |                     |
| змін  | кільк. | арк.           | №док. | підпис | дата |  |                     |
| ГП  |        | Зіньків А.Б    |       |        |      | Багатоквартирний житловий будинок              | стадія              |
| ГАП   |        | Головецький Н. |       |        |      | м. Новий Калинів, Львівська область.           | аркуш               |
|   |        |                |       |        |      | 1 черга будівництва.                           | аркушів             |
| Виконав   |        | Попелястий Р.  |       |        |      |  |                     |
| Перевірив   |        | Зіньків А.Б    |       |        |      | Експлікація комерційних приміщень              | ФОП Никифорець І.І. |
|   |        |                |       |        |      | громадського призначення 1 поверху. Секція №2. |                     |

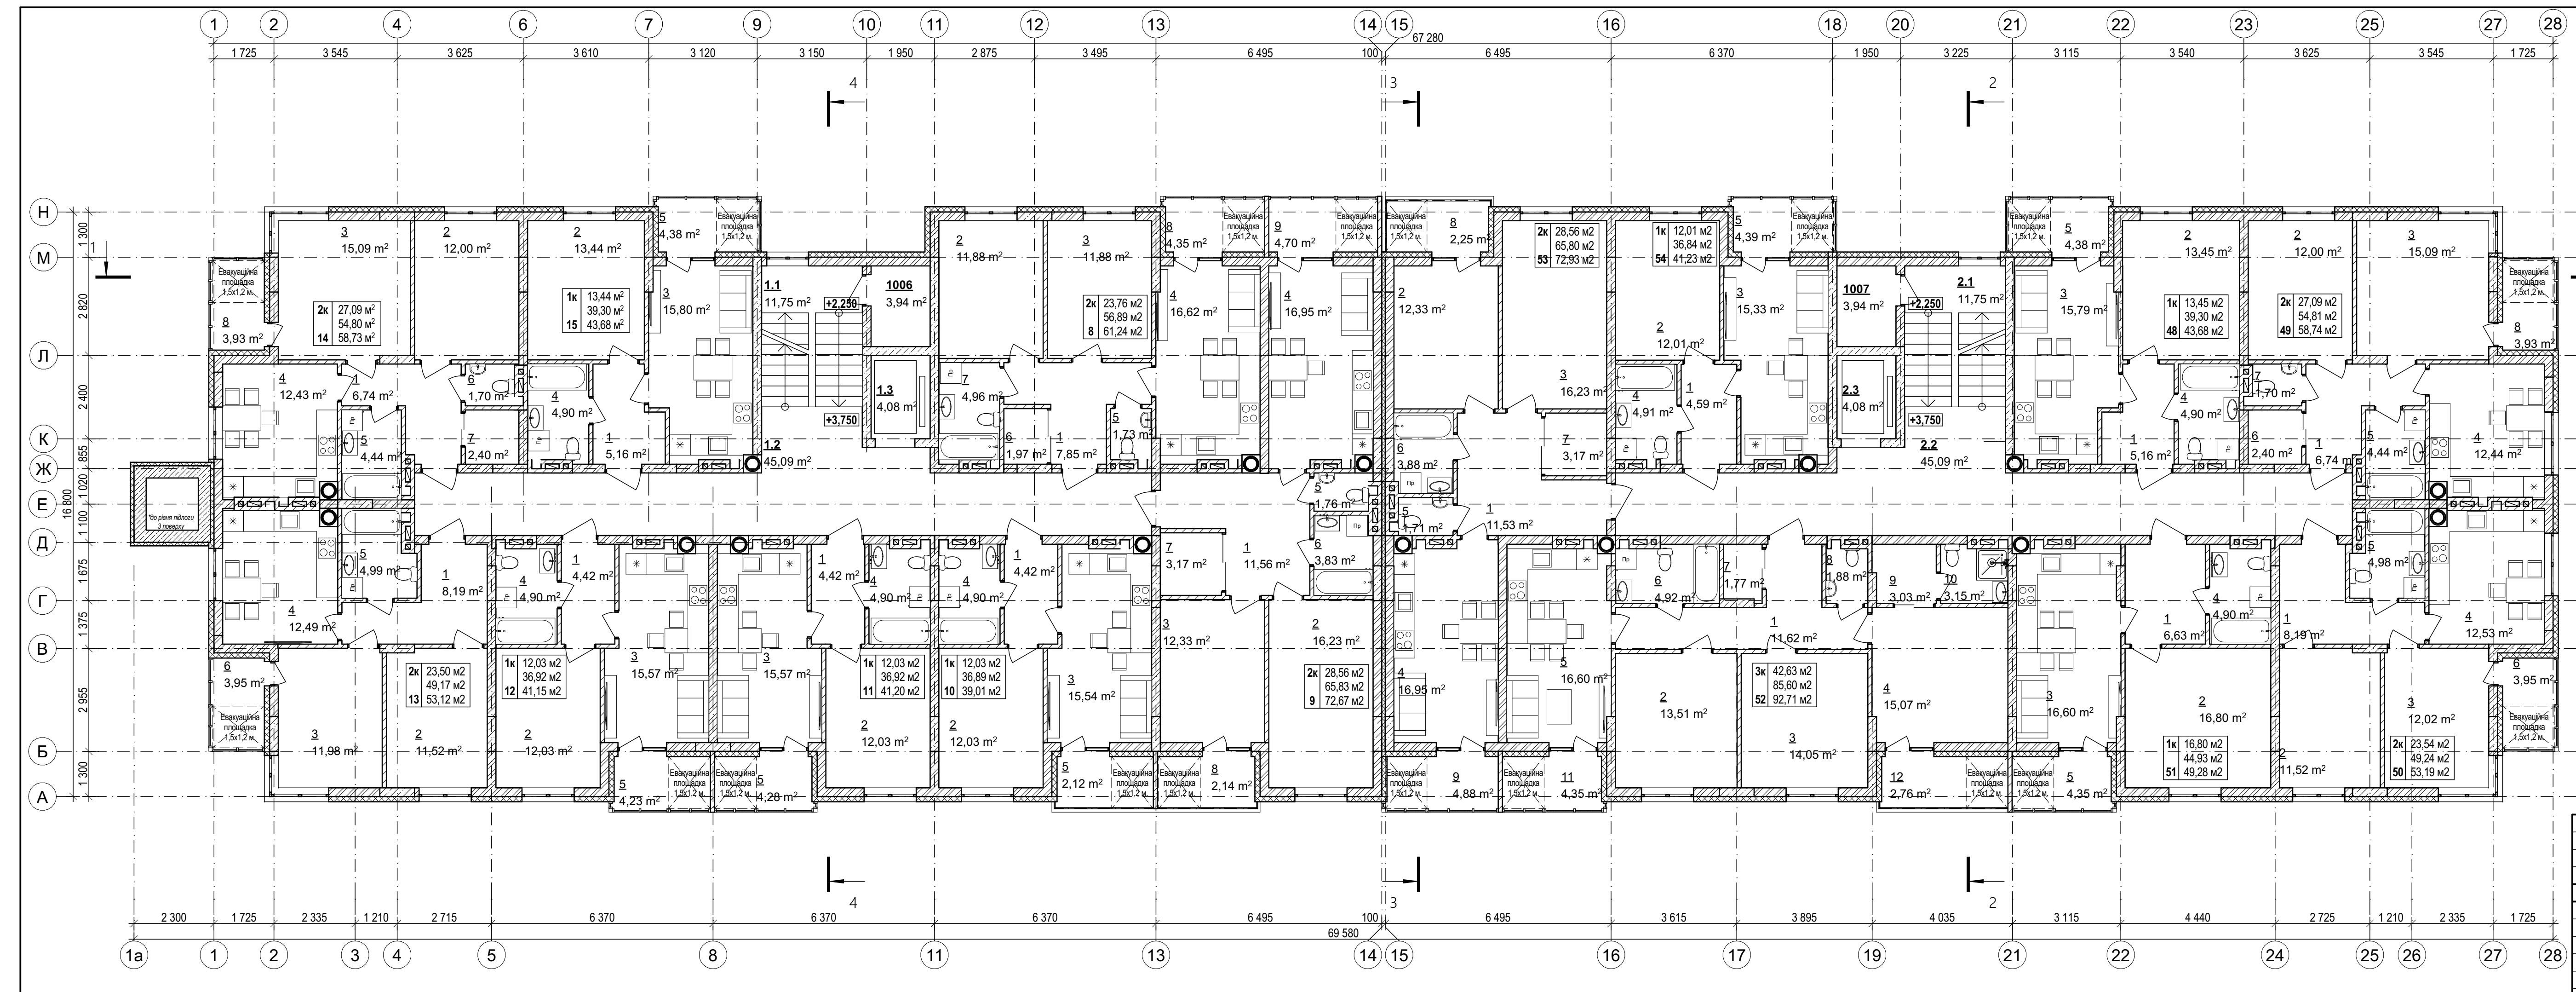

Експлікація при

| №   | Найменування                               | Площа, м <sup>2</sup>       |
|---|--|-----------------------------|
| <i>Приміщення загального користування</i>               |  |                             |
| 1.1   | Сходова клітка (Секція 1)                  | 11,75                       |
| 1.2   | Коридор загального користування (Секція 1) | 45,09                       |
| 1.3   | Шахта ліфта (Секція 1)                     | 4,08                        |
| <i>Разом по секції №1</i>                               |  | <b>60,92 м<sup>2</sup></b>  |
| 2.1   | Сходова клітка (Секція 2)                  | 11,75                       |
| 2.2   | Коридор загального користування (Секція 2) | 45,09                       |
| 2.3   | Шахта ліфта (Секція 2)                     | 4,08                        |
| <i>Разом по секції №2</i>                               |  | <b>60,92 м<sup>2</sup></b>  |
| 1006  | Підсобне приміщення (Секція 1)             | 3,94                        |
| 1007  | Підсобне приміщення (Секція 2)             | 3,94                        |
| <i>Загальна площа приміщень загального користування</i> |  | <b>121,84 м<sup>2</sup></b> |
| <i>Загальна площа комор поверху</i>                     |  | <b>7,88 м<sup>2</sup></b>   |
| <i>Загальна площа квартир на поверсі</i>                |  | <b>822,56 м<sup>2</sup></b> |
| <i>Загальна площа приміщень поверху</i>                 |  | <b>952,28 м<sup>2</sup></b> |


і:  
і техніко-економічні показники та загальні да-  
2.  
вну відмітку 0,000 прийнято рівень чистої під-  
поверху (Секція №2).  
див. аркуш 24-26.  
див. аркуш 27-30.  
гки по вентиляційних каналах див. аркуш 31-  
а внутрішні стіни виконані з керамічної цегли

|     |      |   |        |                     |         |
|-----|------|---|--------|---------------------|---------|
|     |      | 04-01/24  | АР     |                     |         |
|     |      | Нове будівництво багатоквартирного житлового будинку з приміщеннями громадського призначення, за адресою: пл. Авіації, 19б, м. Новий Калинів, Самбірський район, Львівська область. |        |                     |         |
| пис | дата | Багатоквартирний житловий будинок<br>м. Новий Калинів, Львівська область.<br>1 черга будівництва.   | стадія | аркуш               | аркушів |
|     |      |   | П      | 8                   |         |
|     |      | План 2 поверху на відм. +3,750. М1:100  |        | ФОП Никифорець І.І. |         |



| №<br>Кв-ри. | №<br>Експл. | Назва приміщення        | Площа, м <sup>2</sup> | №<br>Кв-ри. | №<br>Експл. | Назва приміщення        | Площа, м <sup>2</sup> | №<br>Кв-ри. | №<br>Експл. | Назва приміщення        | Площа, м <sup>2</sup> |
|-------------|-------------|-------------------------|-----------------------|-------------|-------------|-------------------------|-----------------------|-------------|-------------|-------------------------|-----------------------|
| 48          | 1           | Коридор                 | 5,16                  | 51          | 1           | Коридор                 | 6,63                  | 53          | 1           | Коридор                 | 11,53                 |
| 1К          | 2           | Спальня                 | 13,45                 | 1К          | 2           | Спальня                 | 16,80                 | 2К          | 2           | Спальня                 | 12,33                 |
|             | 3           | Кухня                   | 15,79                 |             | 3           | Кухня                   | 16,60                 |             | 3           | Спальня                 | 16,23                 |
|             | 4           | Ванна кімната           | 4,90                  |             | 4           | Санвузол                | 4,90                  |             | 4           | Кухня                   | 16,95                 |
|             | 5           | Лоджія                  | 4,38                  |             | 5           | Лоджія                  | 4,35                  |             | 5           | Туалет                  | 1,71                  |
|             |             | Житлова площа квартири  | 13,45 м <sup>2</sup>  |             |             | Житлова площа квартири  | 16,80 м <sup>2</sup>  |             | 6           | Ванна кімната           | 3,88                  |
|             |             | Площа квартири          | 39,30 м <sup>2</sup>  |             |             | Площа квартири          | 44,93 м <sup>2</sup>  |             | 7           | Гардероб                | 3,17                  |
|             |             | Загальна площа квартири | 43,68 м <sup>2</sup>  |             |             | Загальна площа квартири | 49,28 м <sup>2</sup>  |             | 8           | Балкон                  | 2,25                  |
|             |             |                         |                       |             |             |                         |                       |             | 9           | Лоджія                  | 4,88                  |
| 49          | 1           | Коридор                 | 6,74                  | 52          | 1           | Коридор                 | 11,62                 |             |             | Житлова площа квартири  | 28,56 м <sup>2</sup>  |
| 2К          | 2           | Спальня                 | 12,00                 | 3К          | 2           | Спальня                 | 13,51                 |             |             | Площа квартири          | 65,80 м <sup>2</sup>  |
|             | 3           | Спальня                 | 15,09                 |             | 3           | Спальня                 | 14,05                 |             |             | Загальна площа квартири | 72,93 м <sup>2</sup>  |
|             | 4           | Кухня                   | 12,44                 |             | 4           | Спальня                 | 15,07                 |             |             |                         |                       |
|             | 5           | Ванна кімната           | 4,44                  |             | 5           | Кухня                   | 16,60                 | 54          | 1           | Коридор                 | 4,59                  |
|             | 6           | Гардероб                | 2,40                  |             | 6           | Ванна кімната           | 4,92                  | 1К          | 2           | Спальня                 | 12,01                 |
|             | 7           | Туалет                  | 1,70                  |             | 7           | Гардероб                | 1,77                  |             | 3           | Кухня                   | 15,33                 |
|             | 8           | Лоджія                  | 3,93                  |             | 8           | Туалет                  | 1,88                  |             | 4           | Санвузол                | 4,91                  |
|             |             | Житлова площа квартири  | 27,09 м <sup>2</sup>  |             | 9           | Гардероб                | 3,03                  |             | 5           | Лоджія                  | 4,39                  |
|             |             | Площа квартири          | 54,81 м <sup>2</sup>  |             | 10          | Санвузол                | 3,15                  |             |             | Житлова площа квартири  | 12,01 м <sup>2</sup>  |
|             |             | Загальна площа квартири | 58,74 м <sup>2</sup>  |             | 11          | Лоджія                  | 4,35                  |             |             | Площа квартири          | 36,84 м <sup>2</sup>  |
|             |             |                         |                       |             | 12          | Балкон                  | 2,76                  |             |             | Загальна площа квартири | 41,23 м <sup>2</sup>  |
| 50          | 1           | Коридор                 | 8,19                  |             |             | Житлова площа квартири  | 42,63 м <sup>2</sup>  |             |             |                         |                       |
| 2К          | 2           | Спальня                 | 11,52                 |             |             | Площа квартири          | 85,60 м <sup>2</sup>  |             |             |                         |                       |
|             | 3           | Спальня                 | 12,02                 |             |             | Загальна площа квартири | 92,71 м <sup>2</sup>  |             |             |                         |                       |
|             | 4           | Кухня                   | 12,53                 |             |             |                         |                       |             |             |                         |                       |
|             | 5           | Санвузол                | 4,98                  |             |             |                         |                       |             |             |                         |                       |
|             | 6           | Лоджія                  | 3,95                  |             |             |                         |                       |             |             |                         |                       |
|             |             | Житлова площа квартири  | 23,54 м <sup>2</sup>  |             |             |                         |                       |             |             |                         |                       |
|             |             | Площа квартири          | 49,24 м <sup>2</sup>  |             |             |                         |                       |             |             |                         |                       |
|             |             | Загальна площа квартири | 53,19 м <sup>2</sup>  |             |             |                         |                       |             |             |                         |                       |

|           |                |      |       |        |      |   |         |                     |  |
|-----------|----------------|------|-------|--------|------|---|---------|---------------------|--|
| змін      | кільк.         | арк. | №док. | підпис | дата | 04-01/24  | АР      |                     |  |
| ГП        | Зіньків А.Б.   |      |       |        |      | Нове будівництво багатоквартирного житлового будинку з приміщеннями громадського призначення, за адресою: пл. Авіації, 196, м. Новий Калинів, Самбірський район, Львівська область. |         |                     |  |
| ГАП       | Головецький Н. |      |       |        |      | Багатоквартирний житловий будинок м. Новий Калинів, Львівська область. 1 черга будівництва.   |         |                     |  |
| Виконав   | Попелястий Р.  |      |       |        |      | стадія  | аркуш   |                     |  |
| Перевірив | Зіньків А.Б.   |      |       |        |      | П   | аркушів |                     |  |
|           |                |      |       |        |      | 10  |         |                     |  |
|           |                |      |       |        |      | Експлуатація квартир 2 поверху. Секція №2 (Квартири 48-82)  |         | ФОП Никифорець І.І. |  |

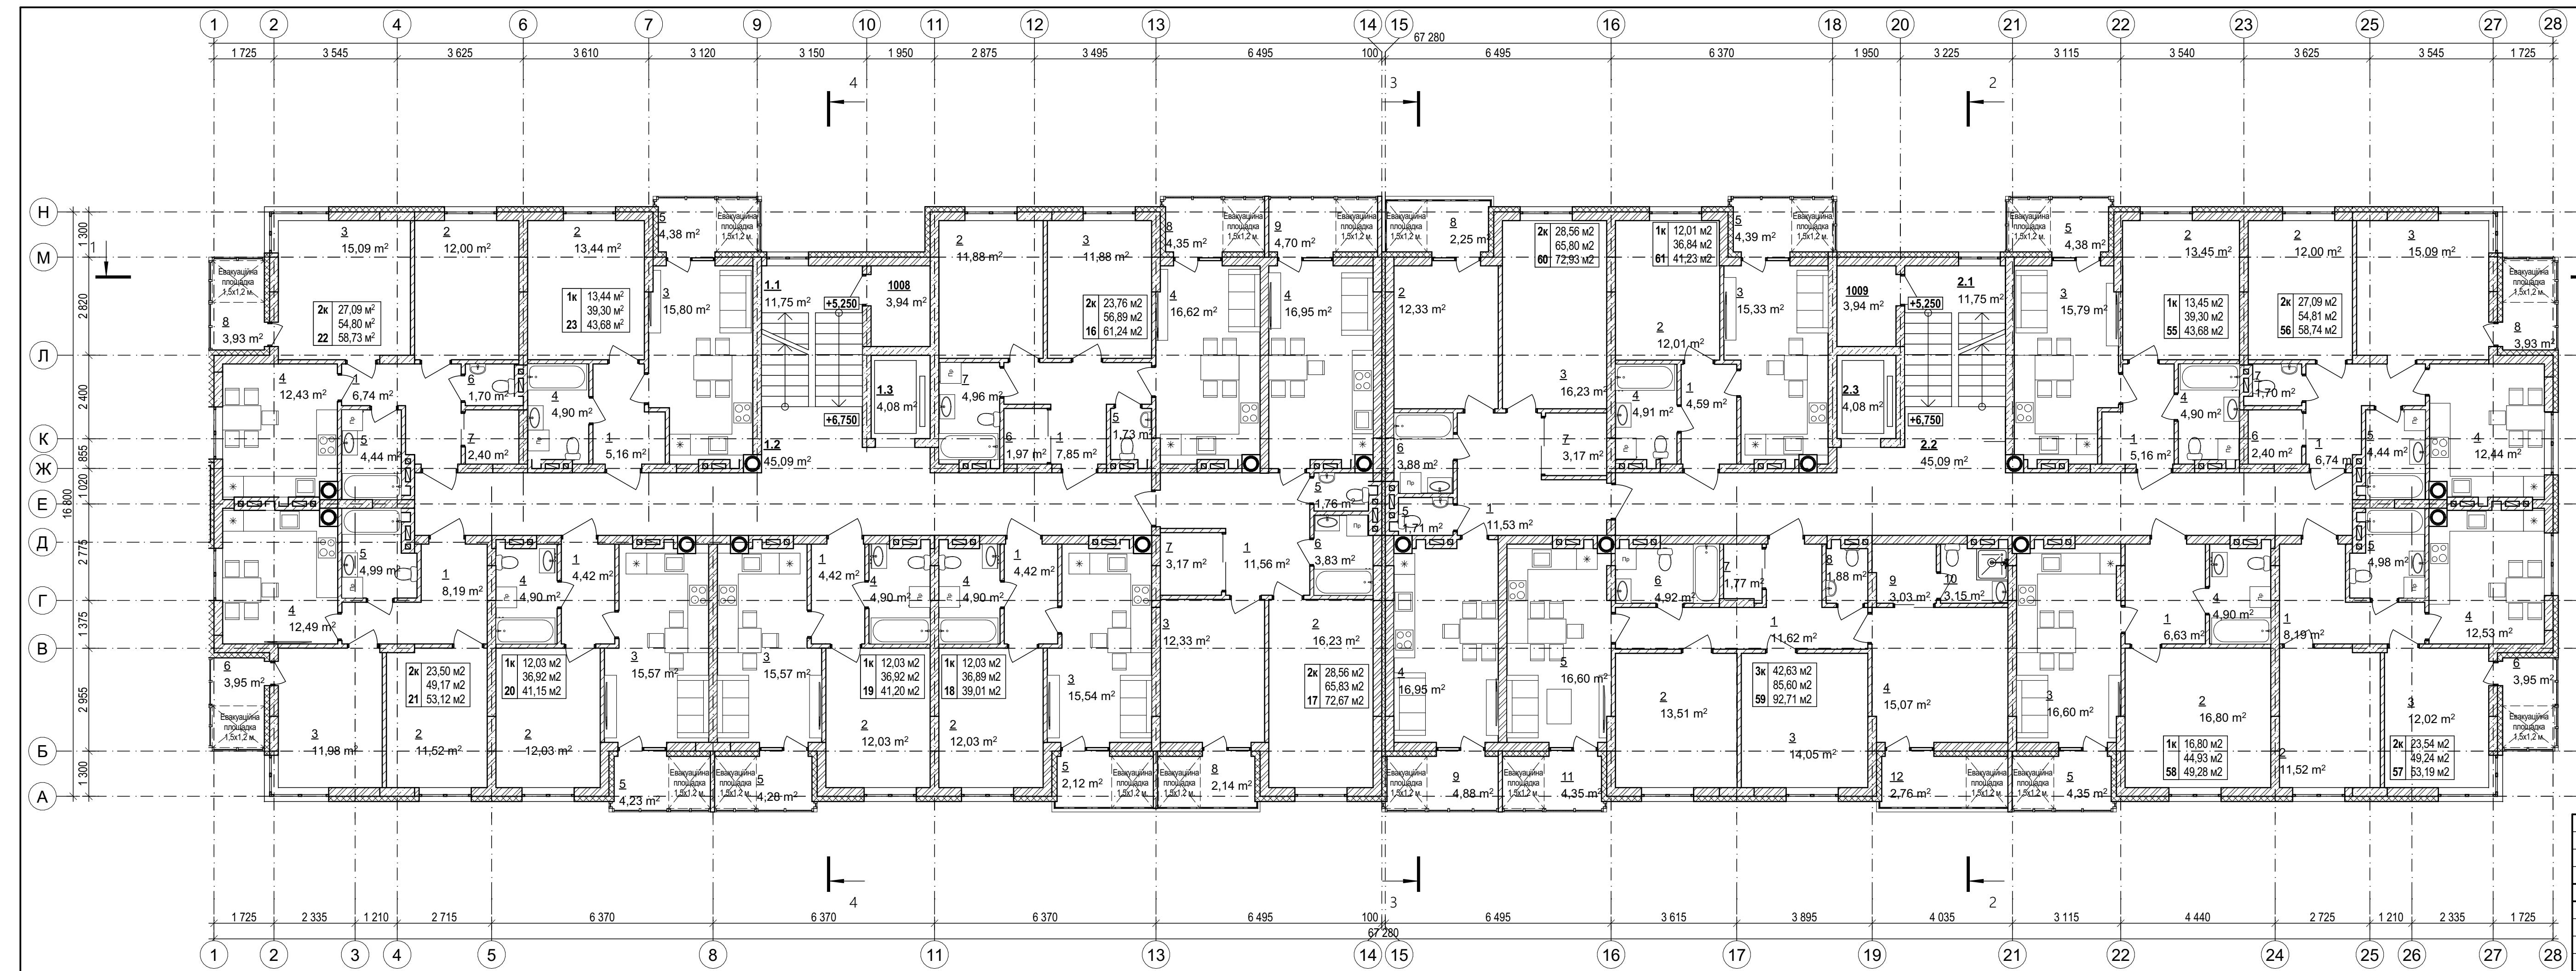

Експлікація пр

| №   | Найменування                               | Площа, м <sup>2</sup>       |
|---|--|-----------------------------|
| <i>Приміщення загального користування</i>               |  |                             |
| 1.1   | Сходова клітка (Секція 1)                  | 11,75                       |
| 1.2   | Коридор загального користування (Секція 1) | 45,09                       |
| 1.3   | Шахта ліфта (Секція 1)                     | 4,08                        |
| <i>Разом по секції №1</i>                               |  | <b>60,92 м<sup>2</sup></b>  |
| 2.1   | Сходова клітка (Секція 2)                  | 11,75                       |
| 2.2   | Коридор загального користування (Секція 2) | 45,09                       |
| 2.3   | Шахта ліфта (Секція 2)                     | 4,08                        |
| <i>Разом по секції №2</i>                               |  | <b>60,92 м<sup>2</sup></b>  |
| 1008  | Підсобне приміщення (Секція 1)             | 3,94                        |
| 1009  | Підсобне приміщення (Секція 2)             | 3,94                        |
| <i>Загальна площа приміщень загального користування</i> |  | <b>121,84 м<sup>2</sup></b> |
| <i>Загальна площа комор поверху</i>                     |  | <b>7,88 м<sup>2</sup></b>   |
| <i>Загальна площа квартир на поверхі</i>                |  | <b>822,56 м<sup>2</sup></b> |
| <i>Загальна площа приміщень поверху</i>                 |  | <b>952,28 м<sup>2</sup></b> |


**Умітки:**  
Основні техніко-економічні показники та загальні данини див. арк. 2.  
За умовну відмітку 0,000 прийнято рівень чистої підлоги земного поверху (Секція №2).  
Фасади див. аркуш 24-26.  
Розрізи див. аркуш 27-30.  
Розгортки по вентиляційних каналах див. аркуш 30.  
Зовн. та внутрішні стіни виконані з керамічної цегли.

|        |      |   |                     |       |         |
|--------|------|---|---------------------|-------|---------|
|        |      | 04-01/24  | АР                  |       |         |
|        |      | Нове будівництво багатоквартирного житлового будинку з приміщеннями громадського призначення, за адресою: пл. Авіації, 19б, м. Новий Калинів, Самбірський район, Львівська область. |                     |       |         |
| підпис | дата | Багатоквартирний житловий будинок<br>м. Новий Калинів, Львівська область.<br>1 черга будівництва.   | стадія              | аркуш | аркушів |
|        |      |   | П                   | 11    |         |
|        |      | План 3 поверху на відм. +6,750. М1:100  | ФОП Никифорець І.І. |       |         |

|           |                |      |       |        |  |                     |
|-----------|----------------|------|-------|--------|--|---------------------|
|           |                |      |       |        | 04-01/24   | АР                  |
|           |                |      |       |        | Нове будівництво багатоквартирного житлового будинку з приміщеннями громадського призначення, за адресою: пл. Авіації 196, м. Новий Калинів, Самбірський район, Львівська область. |                     |
| змін      | кільк.         | арк. | №док. | підпис | дата   |                     |
| ГП        | Зіньків А.Б    |      |       |        | Багатоквартирний житловий будинок<br>м. Новий Калинів, Львівська область.<br>1 черга будівництва.  | стадія              |
| ГАП       | Головецький Н. |      |       |        |  | аркуш               |
|           |                |      |       |        |  | аркуші              |
| П         | 12             |      |       |        |  |                     |
| Виконав   | Попелястий Р.  |      |       |        |  |                     |
| Перевірив | Зіньків А.Б    |      |       |        | Експлікація квартир 3 поверху. Секція №1<br>(Квартири 1-47)  | ФОП Никифорець І.І. |

| №<br>Кв-ри. | №<br>Експл. | Назва приміщення        | Площа, м <sup>2</sup> | №<br>Кв-ри. | №<br>Експл. | Назва приміщення        | Площа, м <sup>2</sup> | №<br>Кв-ри. | №<br>Експл. | Назва приміщення        | Площа, м <sup>2</sup> |
|-------------|-------------|-------------------------|-----------------------|-------------|-------------|-------------------------|-----------------------|-------------|-------------|-------------------------|-----------------------|
| 55          | 1           | Коридор                 | 5,16                  | 58          | 1           | Коридор                 | 6,63                  | 60          | 1           | Коридор                 | 11,53                 |
| 1К          | 2           | Спальня                 | 13,45                 | 1К          | 2           | Спальня                 | 16,80                 | 2К          | 2           | Спальня                 | 12,33                 |
|             | 3           | Кухня                   | 15,79                 |             | 3           | Кухня                   | 16,60                 |             | 3           | Спальня                 | 16,23                 |
|             | 4           | Ванна кімната           | 4,90                  |             | 4           | Санвузол                | 4,90                  |             | 4           | Кухня                   | 16,95                 |
|             | 5           | Лоджія                  | 4,38                  |             | 5           | Лоджія                  | 4,35                  |             | 5           | Туалет                  | 1,71                  |
|             |             | Житлова площа квартири  | 13,45 м <sup>2</sup>  |             |             | Житлова площа квартири  | 16,80 м <sup>2</sup>  |             | 6           | Ванна кімната           | 3,88                  |
|             |             | Площа квартири          | 39,30 м <sup>2</sup>  |             |             | Площа квартири          | 44,93 м <sup>2</sup>  |             | 7           | Гардероб                | 3,17                  |
|             |             | Загальна площа квартири | 43,68 м <sup>2</sup>  |             |             | Загальна площа квартири | 49,28 м <sup>2</sup>  |             | 8           | Балкон                  | 2,25                  |
|             |             |                         |                       |             |             |                         |                       |             | 9           | Лоджія                  | 4,88                  |
| 56          | 1           | Коридор                 | 6,74                  | 59          | 1           | Коридор                 | 11,62                 |             |             | Житлова площа квартири  | 28,56 м <sup>2</sup>  |
| 2К          | 2           | Спальня                 | 12,00                 | 3К          | 2           | Спальня                 | 13,51                 |             |             | Площа квартири          | 65,80 м <sup>2</sup>  |
|             | 3           | Спальня                 | 15,09                 |             | 3           | Спальня                 | 14,05                 |             |             | Загальна площа квартири | 72,93 м <sup>2</sup>  |
|             | 4           | Кухня                   | 12,44                 |             | 4           | Спальня                 | 15,07                 |             |             |                         |                       |
|             | 5           | Ванна кімната           | 4,44                  |             | 5           | Кухня                   | 16,60                 | 61          | 1           | Коридор                 | 4,59                  |
|             | 6           | Гардероб                | 2,40                  |             | 6           | Ванна кімната           | 4,92                  | 1К          | 2           | Спальня                 | 12,01                 |
|             | 7           | Туалет                  | 1,70                  |             | 7           | Гардероб                | 1,77                  |             | 3           | Кухня                   | 15,33                 |
|             | 8           | Лоджія                  | 3,93                  |             | 8           | Туалет                  | 1,88                  |             | 4           | Санвузол                | 4,91                  |
|             |             | Житлова площа квартири  | 27,09 м <sup>2</sup>  |             | 9           | Гардероб                | 3,03                  |             | 5           | Лоджія                  | 4,39                  |
|             |             | Площа квартири          | 54,81 м <sup>2</sup>  |             | 10          | Санвузол                | 3,15                  |             |             | Житлова площа квартири  | 12,01 м <sup>2</sup>  |
|             |             | Загальна площа квартири | 58,74 м <sup>2</sup>  |             | 11          | Лоджія                  | 4,35                  |             |             | Площа квартири          | 36,84 м <sup>2</sup>  |
|             |             |                         |                       |             | 12          | Балкон                  | 2,76                  |             |             | Загальна площа квартири | 41,23 м <sup>2</sup>  |
| 57          | 1           | Коридор                 | 8,19                  |             |             | Житлова площа квартири  | 42,63 м <sup>2</sup>  |             |             |                         |                       |
| 2К          | 2           | Спальня                 | 11,52                 |             |             | Площа квартири          | 85,60 м <sup>2</sup>  |             |             |                         |                       |
|             | 3           | Спальня                 | 12,02                 |             |             | Загальна площа квартири | 92,71 м <sup>2</sup>  |             |             |                         |                       |
|             | 4           | Кухня                   | 12,53                 |             |             |                         |                       |             |             |                         |                       |
|             | 5           | Санвузол                | 4,98                  |             |             |                         |                       |             |             |                         |                       |
|             | 6           | Лоджія                  | 3,95                  |             |             |                         |                       |             |             |                         |                       |
|             |             | Житлова площа квартири  | 23,54 м <sup>2</sup>  |             |             |                         |                       |             |             |                         |                       |
|             |             | Площа квартири          | 49,24 м <sup>2</sup>  |             |             |                         |                       |             |             |                         |                       |
|             |             | Загальна площа квартири | 53,19 м <sup>2</sup>  |             |             |                         |                       |             |             |                         |                       |


|           |                |      |       |        |      |   |         |                     |  |
|-----------|----------------|------|-------|--------|------|---|---------|---------------------|--|
| змін      | кільк.         | арк. | №док. | підпис | дата | 04-01/24  | АР      |                     |  |
| ГП        | Зіньків А.Б.   |      |       |        |      | Нове будівництво багатоквартирного житлового будинку з приміщеннями громадського призначення, за адресою: пл. Авіації, 196, м. Новий Калинів, Самбірський район, Львівська область. |         |                     |  |
| ГАП       | Головецький Н. |      |       |        |      | Багатоквартирний житловий будинок м. Новий Калинів, Львівська область. 1 черга будівництва.   |         |                     |  |
| Виконав   | Попелястий Р.  |      |       |        |      | стадія  | аркуш   |                     |  |
| Перевірив | Зіньків А.Б.   |      |       |        |      | П   | аркушів |                     |  |
|           |                |      |       |        |      | 13  |         |                     |  |
|           |                |      |       |        |      | Експлуатація квартир 3 поверху. Секція №2 (Квартири 48-82)  |         | ФОП Никифорець І.І. |  |

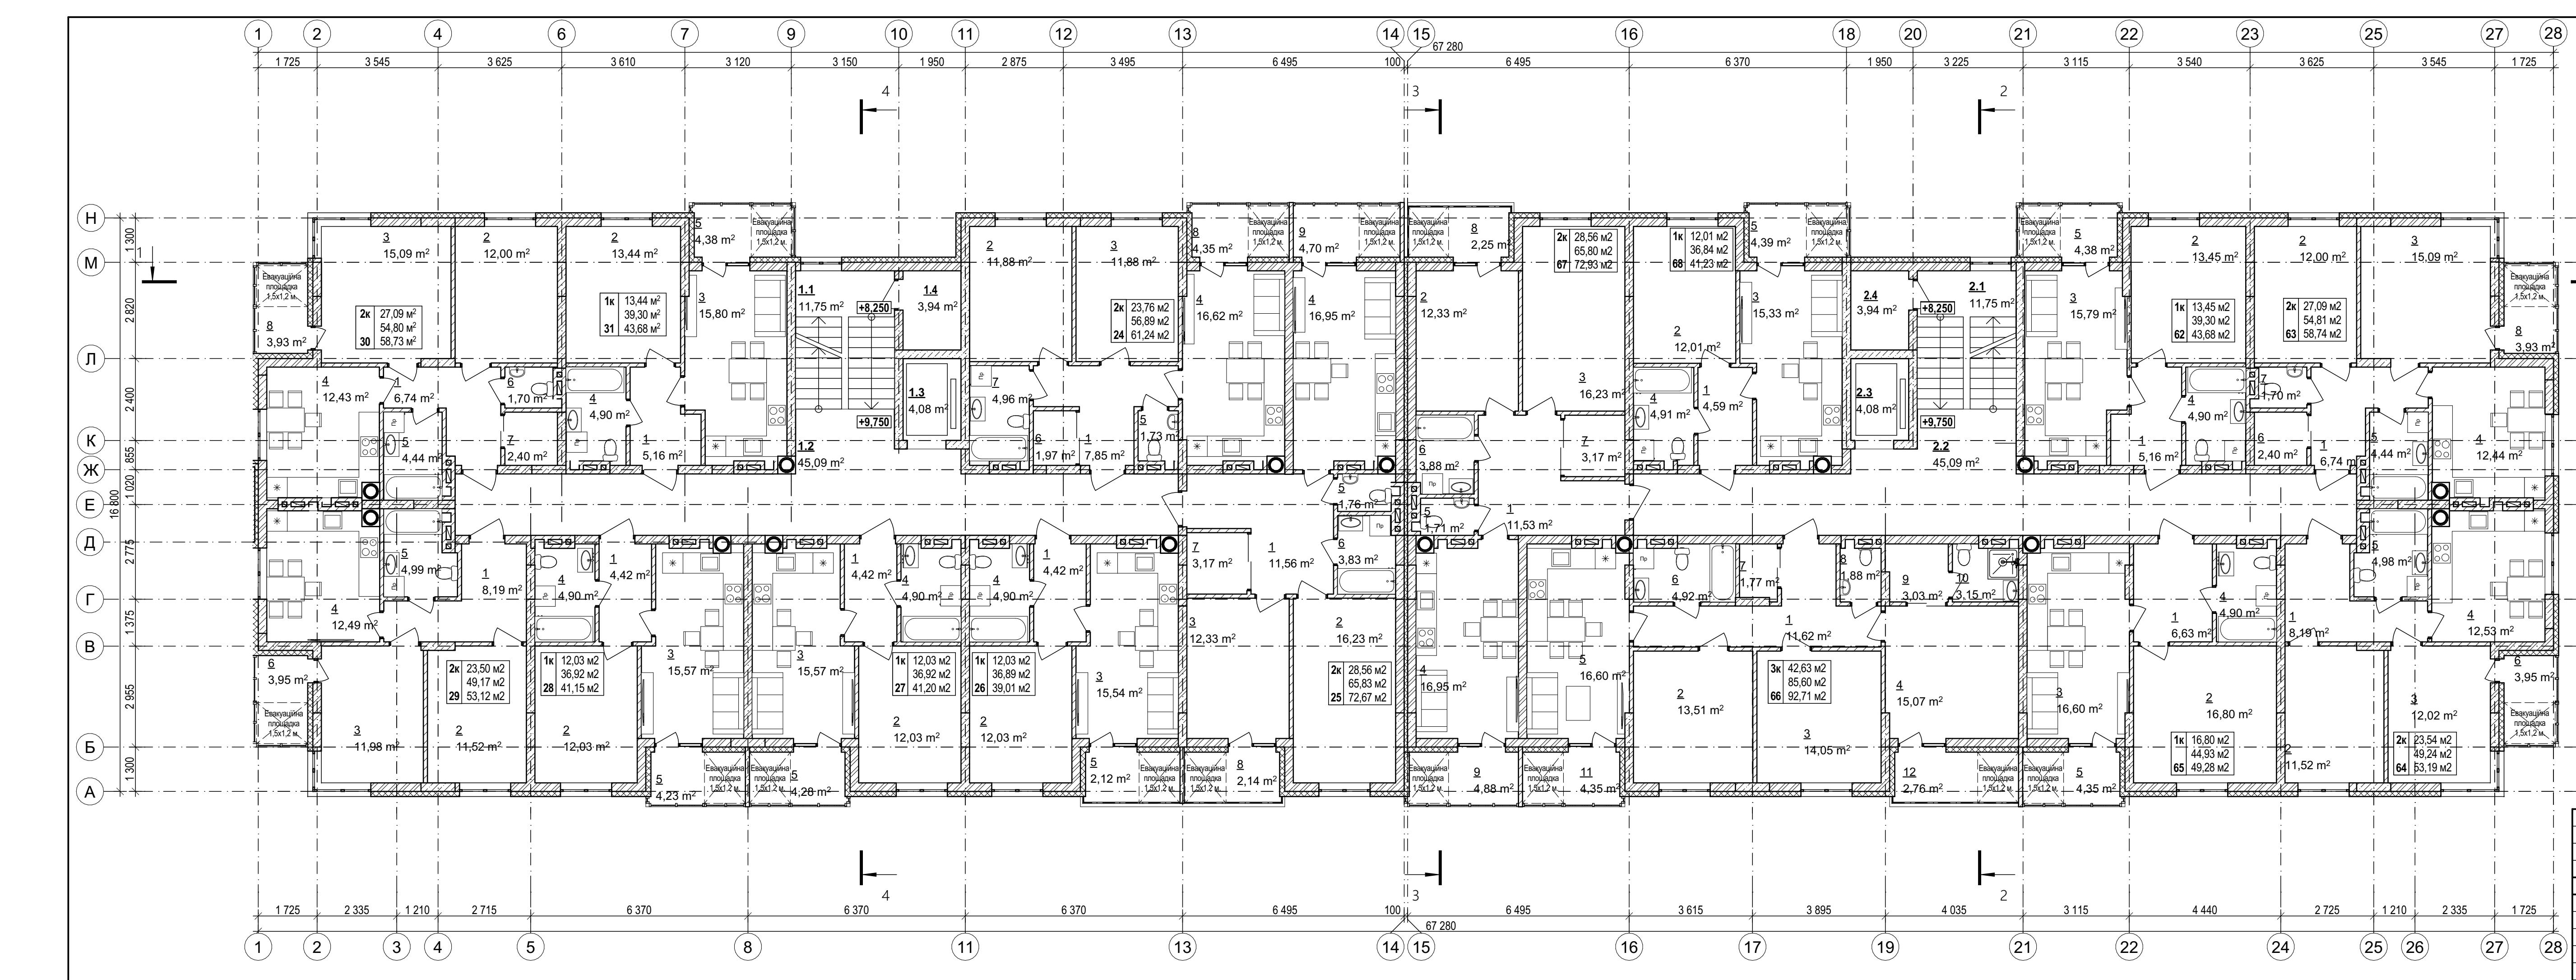



| №<br>Кв-ри. | №<br>Експл. | Назва приміщення        | Площа, м <sup>2</sup> | №<br>Кв-ри. | №<br>Експл. | Назва приміщення        | Площа, м <sup>2</sup> | №<br>Кв-ри. | №<br>Експл. | Назва приміщення        | Площа, м <sup>2</sup> |
|-------------|-------------|-------------------------|-----------------------|-------------|-------------|-------------------------|-----------------------|-------------|-------------|-------------------------|-----------------------|
| 62          | 1           | Коридор                 | 5,16                  | 65          | 1           | Коридор                 | 6,63                  | 67          | 1           | Коридор                 | 11,53                 |
| 1К          | 2           | Спальня                 | 13,45                 | 1К          | 2           | Спальня                 | 16,80                 | 2К          | 2           | Спальня                 | 12,33                 |
|             | 3           | Кухня                   | 15,79                 |             | 3           | Кухня                   | 16,60                 |             | 3           | Спальня                 | 16,23                 |
|             | 4           | Ванна кімната           | 4,90                  |             | 4           | Санвузол                | 4,90                  |             | 4           | Кухня                   | 16,95                 |
|             | 5           | Лоджія                  | 4,38                  |             | 5           | Лоджія                  | 4,35                  |             | 5           | Туалет                  | 1,71                  |
|             |             | Житлова площа квартири  | 13,45 м <sup>2</sup>  |             |             | Житлова площа квартири  | 16,80 м <sup>2</sup>  |             | 6           | Ванна кімната           | 3,88                  |
|             |             | Площа квартири          | 39,30 м <sup>2</sup>  |             |             | Площа квартири          | 44,93 м <sup>2</sup>  |             | 7           | Гардероб                | 3,17                  |
|             |             | Загальна площа квартири | 43,68 м <sup>2</sup>  |             |             | Загальна площа квартири | 49,28 м <sup>2</sup>  |             | 8           | Балкон                  | 2,25                  |
|             |             |                         |                       |             |             |                         |                       |             | 9           | Лоджія                  | 4,88                  |
| 63          | 1           | Коридор                 | 6,74                  | 66          | 1           | Коридор                 | 11,62                 |             |             | Житлова площа квартири  | 28,56 м <sup>2</sup>  |
| 2К          | 2           | Спальня                 | 12,00                 | 3К          | 2           | Спальня                 | 13,51                 |             |             | Площа квартири          | 65,80 м <sup>2</sup>  |
|             | 3           | Спальня                 | 15,09                 |             | 3           | Спальня                 | 14,05                 |             |             | Загальна площа квартири | 72,93 м <sup>2</sup>  |
|             | 4           | Кухня                   | 12,44                 |             | 4           | Спальня                 | 15,07                 |             |             |                         |                       |
|             | 5           | Ванна кімната           | 4,44                  |             | 5           | Кухня                   | 16,60                 | 68          | 1           | Коридор                 | 4,59                  |
|             | 6           | Гардероб                | 2,40                  |             | 6           | Ванна кімната           | 4,92                  | 1К          | 2           | Спальня                 | 12,01                 |
|             | 7           | Туалет                  | 1,70                  |             | 7           | Гардероб                | 1,77                  |             | 3           | Кухня                   | 15,33                 |
|             | 8           | Лоджія                  | 3,93                  |             | 8           | Туалет                  | 1,88                  |             | 4           | Санвузол                | 4,91                  |
|             |             | Житлова площа квартири  | 27,09 м <sup>2</sup>  |             | 9           | Гардероб                | 3,03                  |             | 5           | Лоджія                  | 4,39                  |
|             |             | Площа квартири          | 54,81 м <sup>2</sup>  |             | 10          | Санвузол                | 3,15                  |             |             | Житлова площа квартири  | 12,01 м <sup>2</sup>  |
|             |             | Загальна площа квартири | 58,74 м <sup>2</sup>  |             | 11          | Лоджія                  | 4,35                  |             |             | Площа квартири          | 36,84 м <sup>2</sup>  |
|             |             |                         |                       |             | 12          | Балкон                  | 2,76                  |             |             | Загальна площа квартири | 41,23 м <sup>2</sup>  |
| 64          | 1           | Коридор                 | 8,19                  |             |             | Житлова площа квартири  | 42,63 м <sup>2</sup>  |             |             |                         |                       |
| 2К          | 2           | Спальня                 | 11,52                 |             |             | Площа квартири          | 85,60 м <sup>2</sup>  |             |             |                         |                       |
|             | 3           | Спальня                 | 12,02                 |             |             | Загальна площа квартири | 92,71 м <sup>2</sup>  |             |             |                         |                       |
|             | 4           | Кухня                   | 12,53                 |             |             |                         |                       |             |             |                         |                       |
|             | 5           | Санвузол                | 4,98                  |             |             |                         |                       |             |             |                         |                       |
|             | 6           | Лоджія                  | 3,95                  |             |             |                         |                       |             |             |                         |                       |
|             |             | Житлова площа квартири  | 23,54 м <sup>2</sup>  |             |             |                         |                       |             |             |                         |                       |
|             |             | Площа квартири          | 49,24 м <sup>2</sup>  |             |             |                         |                       |             |             |                         |                       |
|             |             | Загальна площа квартири | 53,19 м <sup>2</sup>  |             |             |                         |                       |             |             |                         |                       |


|           |                |      |       |        |      |   |         |                     |  |
|-----------|----------------|------|-------|--------|------|---|---------|---------------------|--|
| змін      | кільк.         | арк. | №док. | підпис | дата | 04-01/24  | АР      |                     |  |
| ГП        | Зіньків А.Б.   |      |       |        |      | Нове будівництво багатоквартирного житлового будинку з приміщеннями громадського призначення, за адресою: пл. Авіації, 196, м. Новий Калинів, Самбірський район, Львівська область. |         |                     |  |
| ГАП       | Головецький Н. |      |       |        |      | Багатоквартирний житловий будинок м. Новий Калинів, Львівська область. 1 черга будівництва.   |         |                     |  |
| Виконав   | Попелястий Р.  |      |       |        |      | стадія  | аркуш   |                     |  |
| Перевірив | Зіньків А.Б.   |      |       |        |      | П   | аркушів |                     |  |
|           |                |      |       |        |      | 16  |         |                     |  |
|           |                |      |       |        |      | Експлікація квартир 4 поверху. Секція №2 (Квартири 48-82)   |         | ФОП Никифорець І.І. |  |

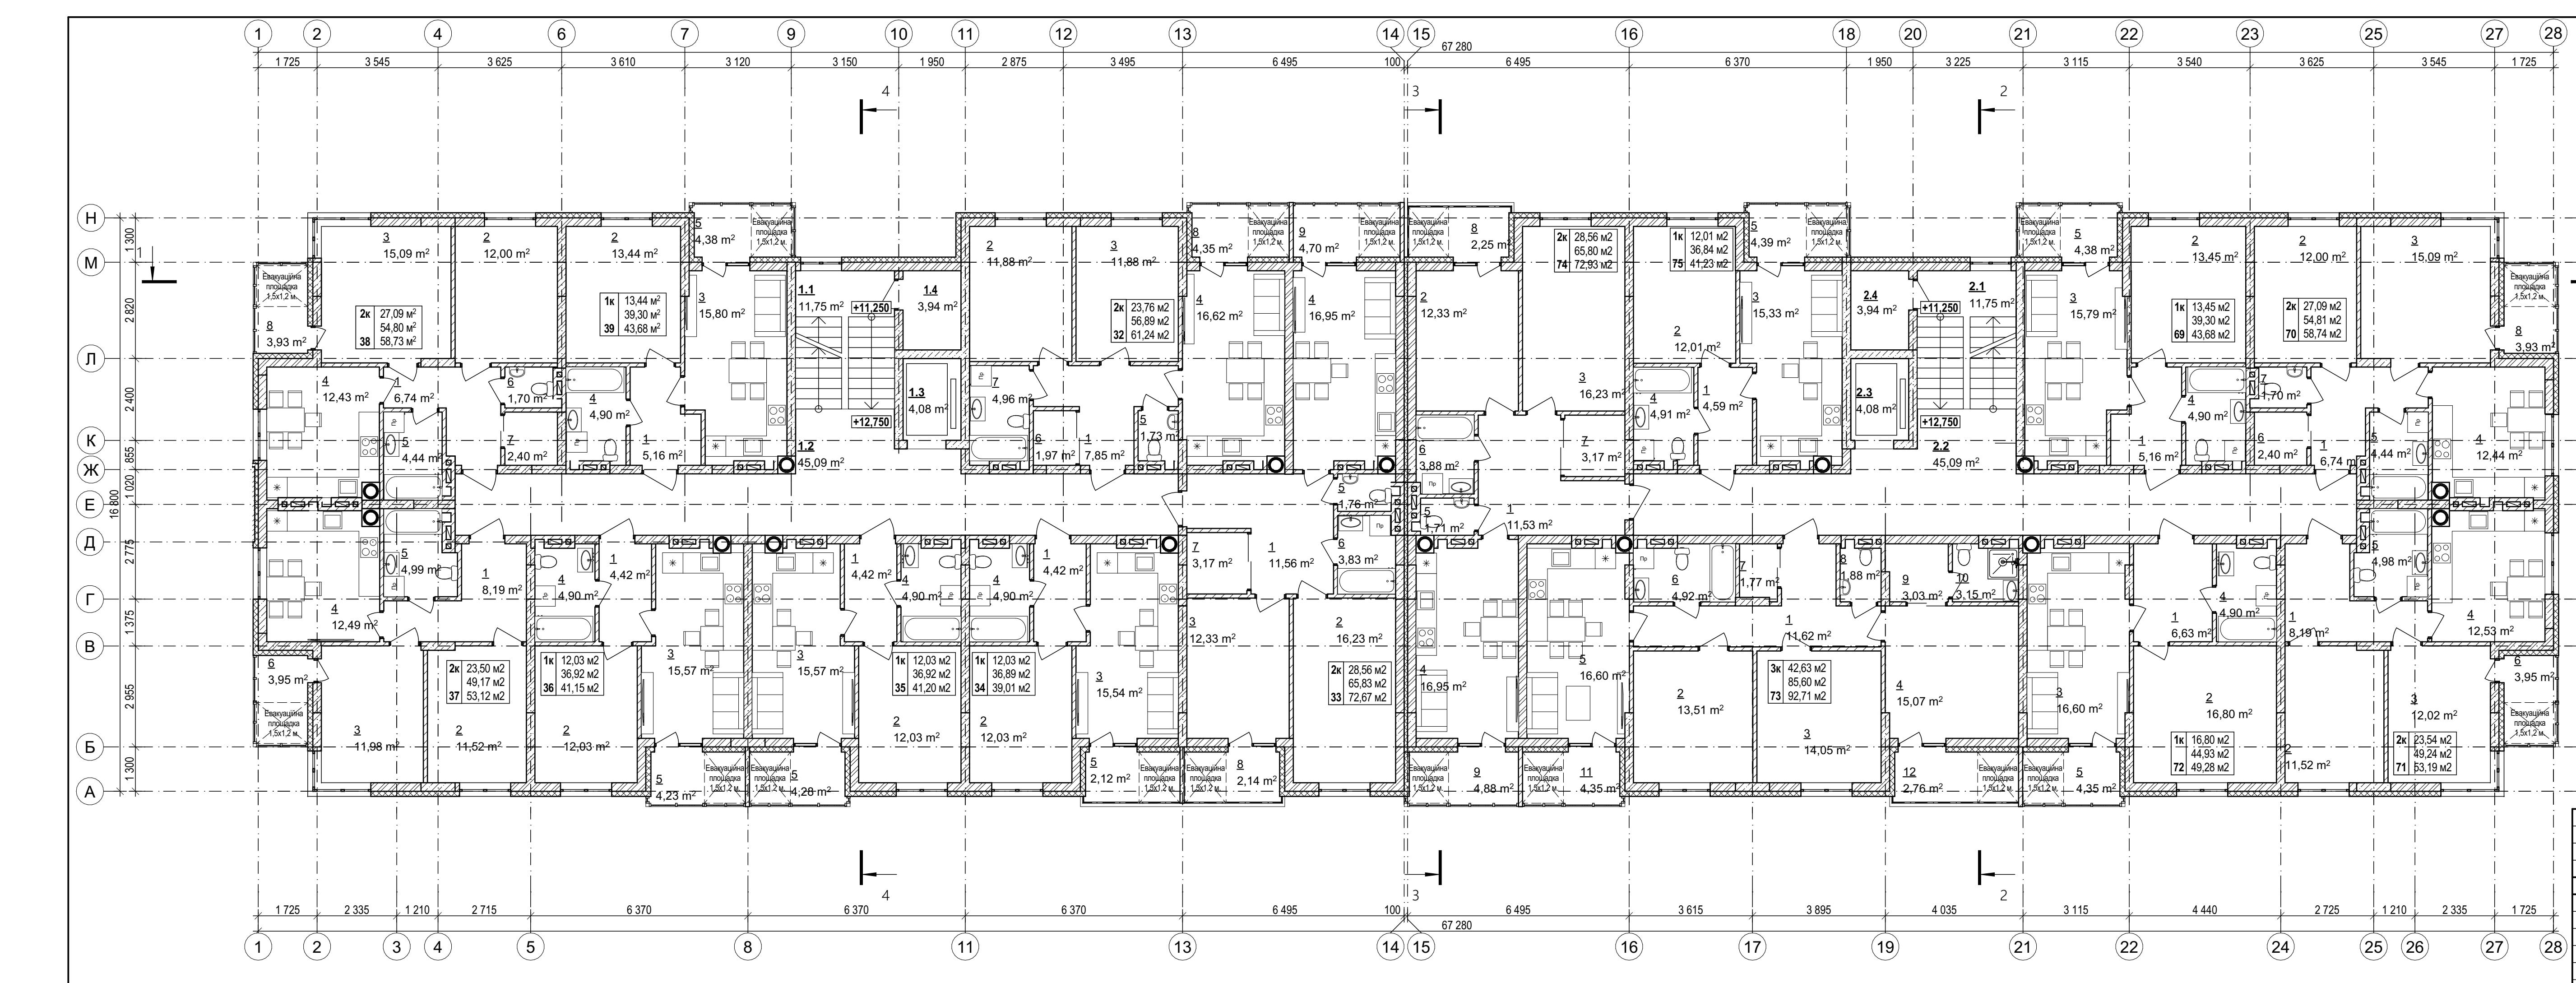



| №<br>Кв-ри. | №<br>Експл. | Назва приміщення        | Площа, м <sup>2</sup> | №<br>Кв-ри. | №<br>Експл. | Назва приміщення        | Площа, м <sup>2</sup> | №<br>Кв-ри. | №<br>Експл. | Назва приміщення        | Площа, м <sup>2</sup> |
|-------------|-------------|-------------------------|-----------------------|-------------|-------------|-------------------------|-----------------------|-------------|-------------|-------------------------|-----------------------|
| 69          | 1           | Коридор                 | 5,16                  | 72          | 1           | Коридор                 | 6,63                  | 74          | 1           | Коридор                 | 11,53                 |
| 1К          | 2           | Спальня                 | 13,45                 | 1К          | 2           | Спальня                 | 16,80                 | 2К          | 2           | Спальня                 | 12,33                 |
|             | 3           | Кухня                   | 15,79                 |             | 3           | Кухня                   | 16,60                 |             | 3           | Спальня                 | 16,23                 |
|             | 4           | Ванна кімната           | 4,90                  |             | 4           | Санвузол                | 4,90                  |             | 4           | Кухня                   | 16,95                 |
|             | 5           | Лоджія                  | 4,38                  |             | 5           | Лоджія                  | 4,35                  |             | 5           | Туалет                  | 1,71                  |
|             |             | Житлова площа квартири  | 13,45 м <sup>2</sup>  |             |             | Житлова площа квартири  | 16,80 м <sup>2</sup>  |             | 6           | Ванна кімната           | 3,88                  |
|             |             | Площа квартири          | 39,30 м <sup>2</sup>  |             |             | Площа квартири          | 44,93 м <sup>2</sup>  |             | 7           | Гардероб                | 3,17                  |
|             |             | Загальна площа квартири | 43,68 м <sup>2</sup>  |             |             | Загальна площа квартири | 49,28 м <sup>2</sup>  |             | 8           | Балкон                  | 2,25                  |
|             |             |                         |                       |             |             |                         |                       |             | 9           | Лоджія                  | 4,88                  |
| 70          | 1           | Коридор                 | 6,74                  | 73          | 1           | Коридор                 | 11,62                 |             |             | Житлова площа квартири  | 28,56 м <sup>2</sup>  |
| 2К          | 2           | Спальня                 | 12,00                 | 3К          | 2           | Спальня                 | 13,51                 |             |             | Площа квартири          | 65,80 м <sup>2</sup>  |
|             | 3           | Спальня                 | 15,09                 |             | 3           | Спальня                 | 14,05                 |             |             | Загальна площа квартири | 72,93 м <sup>2</sup>  |
|             | 4           | Кухня                   | 12,44                 |             | 4           | Спальня                 | 15,07                 |             |             |                         |                       |
|             | 5           | Ванна кімната           | 4,44                  |             | 5           | Кухня                   | 16,60                 | 75          | 1           | Коридор                 | 4,59                  |
|             | 6           | Гардероб                | 2,40                  |             | 6           | Ванна кімната           | 4,92                  | 1К          | 2           | Спальня                 | 12,01                 |
|             | 7           | Туалет                  | 1,70                  |             | 7           | Гардероб                | 1,77                  |             | 3           | Кухня                   | 15,33                 |
|             | 8           | Лоджія                  | 3,93                  |             | 8           | Туалет                  | 1,88                  |             | 4           | Санвузол                | 4,91                  |
|             |             | Житлова площа квартири  | 27,09 м <sup>2</sup>  |             | 9           | Гардероб                | 3,03                  |             | 5           | Лоджія                  | 4,39                  |
|             |             | Площа квартири          | 54,81 м <sup>2</sup>  |             | 10          | Санвузол                | 3,15                  |             |             | Житлова площа квартири  | 12,01 м <sup>2</sup>  |
|             |             | Загальна площа квартири | 58,74 м <sup>2</sup>  |             | 11          | Лоджія                  | 4,35                  |             |             | Площа квартири          | 36,84 м <sup>2</sup>  |
|             |             |                         |                       |             | 12          | Балкон                  | 2,76                  |             |             | Загальна площа квартири | 41,23 м <sup>2</sup>  |
| 71          | 1           | Коридор                 | 8,19                  |             |             | Житлова площа квартири  | 42,63 м <sup>2</sup>  |             |             |                         |                       |
| 2К          | 2           | Спальня                 | 11,52                 |             |             | Площа квартири          | 85,60 м <sup>2</sup>  |             |             |                         |                       |
|             | 3           | Спальня                 | 12,02                 |             |             | Загальна площа квартири | 92,71 м <sup>2</sup>  |             |             |                         |                       |
|             | 4           | Кухня                   | 12,53                 |             |             |                         |                       |             |             |                         |                       |
|             | 5           | Санвузол                | 4,98                  |             |             |                         |                       |             |             |                         |                       |
|             | 6           | Лоджія                  | 3,95                  |             |             |                         |                       |             |             |                         |                       |
|             |             | Житлова площа квартири  | 23,54 м <sup>2</sup>  |             |             |                         |                       |             |             |                         |                       |
|             |             | Площа квартири          | 49,24 м <sup>2</sup>  |             |             |                         |                       |             |             |                         |                       |
|             |             | Загальна площа квартири | 53,19 м <sup>2</sup>  |             |             |                         |                       |             |             |                         |                       |

|           |                |      |       |        |      |   |         |                     |  |
|-----------|----------------|------|-------|--------|------|---|---------|---------------------|--|
| змін      | кільк.         | арк. | №док. | підпис | дата | 04-01/24  | АР      |                     |  |
| ГП        | Зіньків А.Б.   |      |       |        |      | Нове будівництво багатоквартирного житлового будинку з приміщеннями громадського призначення, за адресою: пл. Авіації, 196, м. Новий Калинів, Самбірський район, Львівська область. |         |                     |  |
| ГАП       | Головецький Н. |      |       |        |      | Багатоквартирний житловий будинок м. Новий Калинів, Львівська область. 1 черга будівництва.   |         |                     |  |
| Виконав   | Попелястий Р.  |      |       |        |      | стадія  | аркуш   |                     |  |
| Перевірив | Зіньків А.Б.   |      |       |        |      | П   | аркушів |                     |  |
|           |                |      |       |        |      | 19  |         |                     |  |
|           |                |      |       |        |      | Експлуатація квартир 5 поверху. Секція №2 (Квартири 48-82)  |         | ФОП Никифорець І.І. |  |

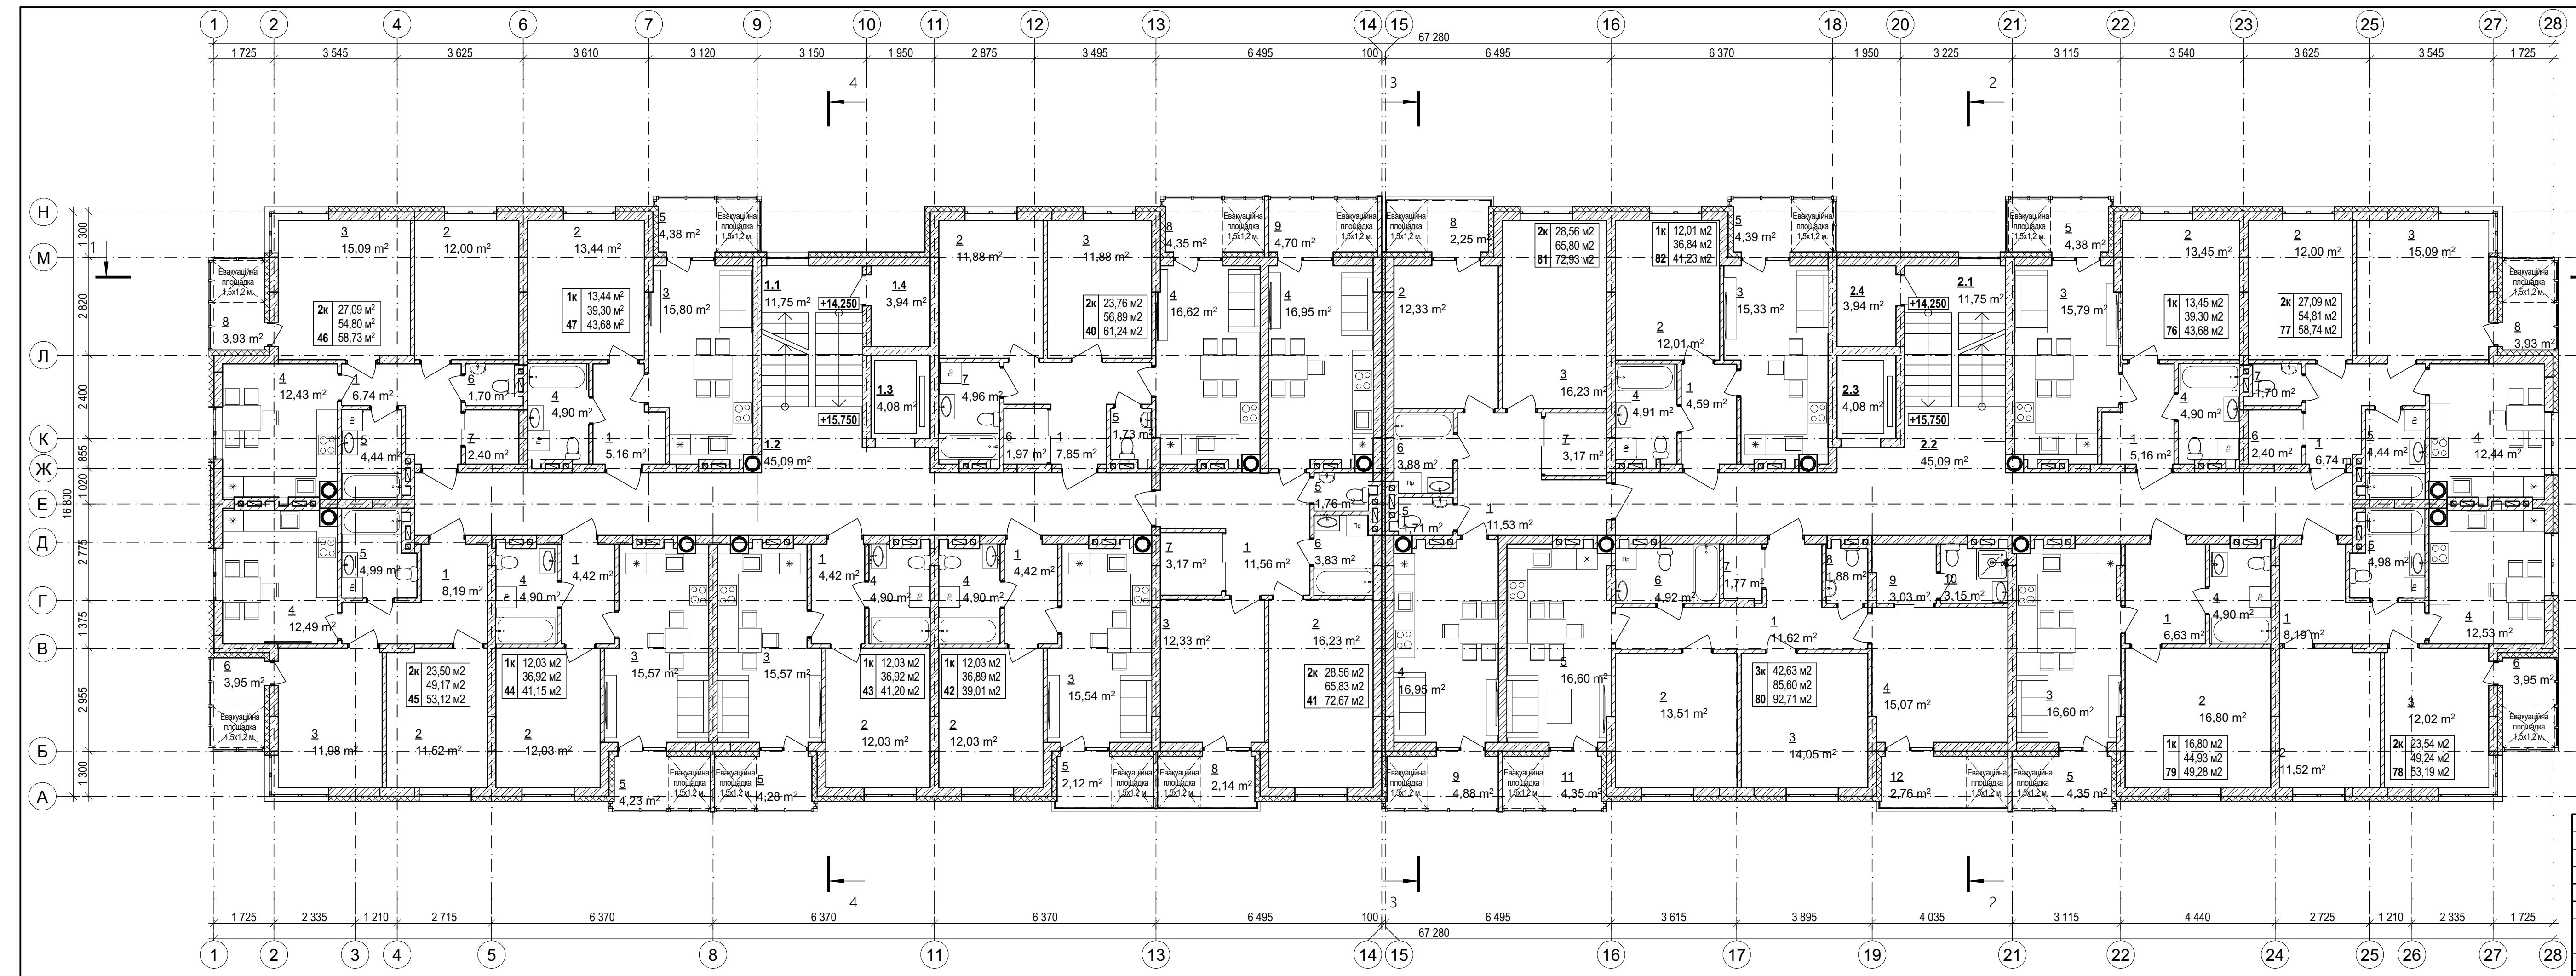

Експлікація при

| №   | Найменування                               | Площа, м <sup>2</sup>       |
|---|--|-----------------------------|
| <i>Приміщення загального користування</i>               |  |                             |
| 1.1   | Сходова клітка (Секція 1)                  | 11,75                       |
| 1.2   | Коридор загального користування (Секція 1) | 45,09                       |
| 1.3   | Шахта ліфта (Секція 1)                     | 4,08                        |
| 1.4   | Підсобне приміщення (Секція 1)             | 3,94                        |
| <i>Разом по секції №1</i>                               |  | <b>64,86 м<sup>2</sup></b>  |
| 2.1   | Сходова клітка (Секція 2)                  | 11,75                       |
| 2.2   | Коридор загального користування (Секція 2) | 45,09                       |
| 2.3   | Шахта ліфта (Секція 2)                     | 4,08                        |
| 2.4   | Підсобне приміщення (Секція 2)             | 3,94                        |
| <i>Разом по секції №2</i>                               |  | <b>64,86 м<sup>2</sup></b>  |
| <i>Загальна площа приміщень загального користування</i> |  | <b>129,72 м<sup>2</sup></b> |
| <i>Загальна площа квартир на поверхі</i>                |  | <b>822,56 м<sup>2</sup></b> |
| <i>Загальна площа приміщень поверху</i>                 |  | <b>952,28 м<sup>2</sup></b> |


**Іміткі:**  
Основні техніко-економічні показники та загальні да-  
з. арк. 2.  
За умовну відмітку 0,000 прийнято рівень чистої під-  
шого поверху (Секція №2).  
Фасади див. аркуш 24-26.  
Розрізи див. аркуш 27-30.  
Розгортки по вентиляційних каналах див. аркуш 31-32.  
Зовн. та внутрішні стіни виконані з керамічної цегли

|        |      |   |        |                     |
|--------|------|---|--------|---------------------|
|        |      | 04-01/24  | АР     |                     |
| підпис | дата | Нове будівництво багатоквартирного житлового будинку з приміщеннями громадського призначення, за адресою: пл. Авіації, 19б, м. Новий Калинів, Самбірський район, Львівська область. |        |                     |
|        |      | Багатоквартирний житловий будинок<br>м. Новий Калинів, Львівська область.<br>1 черга будівництва.   | стадія | аркуш               |
|        |      | П   | 20     |                     |
|        |      | План 6 поверху на відм. +15,750. М1:100   |        | ФОП Никифорець І.І. |



| №<br>Кв-ри. | №<br>Експл. | Назва приміщення        | Площа, м <sup>2</sup> | №<br>Кв-ри. | №<br>Експл. | Назва приміщення        | Площа, м <sup>2</sup> | №<br>Кв-ри. | №<br>Експл. | Назва приміщення        | Площа, м <sup>2</sup> |
|-------------|-------------|-------------------------|-----------------------|-------------|-------------|-------------------------|-----------------------|-------------|-------------|-------------------------|-----------------------|
| 76          | 1           | Коридор                 | 5,16                  | 79          | 1           | Коридор                 | 6,63                  | 81          | 1           | Коридор                 | 11,53                 |
| 1К          | 2           | Спальня                 | 13,45                 | 1К          | 2           | Спальня                 | 16,80                 | 2К          | 2           | Спальня                 | 12,33                 |
|             | 3           | Кухня                   | 15,79                 |             | 3           | Кухня                   | 16,60                 |             | 3           | Спальня                 | 16,23                 |
|             | 4           | Ванна кімната           | 4,90                  |             | 4           | Санвузол                | 4,90                  |             | 4           | Кухня                   | 16,95                 |
|             | 5           | Лоджія                  | 4,38                  |             | 5           | Лоджія                  | 4,35                  |             | 5           | Туалет                  | 1,71                  |
|             |             | Житлова площа квартири  | 13,45 м <sup>2</sup>  |             |             | Житлова площа квартири  | 16,80 м <sup>2</sup>  |             | 6           | Ванна кімната           | 3,88                  |
|             |             | Площа квартири          | 39,30 м <sup>2</sup>  |             |             | Площа квартири          | 44,93 м <sup>2</sup>  |             | 7           | Гардероб                | 3,17                  |
|             |             | Загальна площа квартири | 43,68 м <sup>2</sup>  |             |             | Загальна площа квартири | 49,28 м <sup>2</sup>  |             | 8           | Балкон                  | 2,25                  |
|             |             |                         |                       |             |             |                         |                       |             | 9           | Лоджія                  | 4,88                  |
| 77          | 1           | Коридор                 | 6,74                  | 80          | 1           | Коридор                 | 11,62                 |             |             | Житлова площа квартири  | 28,56 м <sup>2</sup>  |
| 2К          | 2           | Спальня                 | 12,00                 | 3К          | 2           | Спальня                 | 13,51                 |             |             | Площа квартири          | 65,80 м <sup>2</sup>  |
|             | 3           | Спальня                 | 15,09                 |             | 3           | Спальня                 | 14,05                 |             |             | Загальна площа квартири | 72,93 м <sup>2</sup>  |
|             | 4           | Кухня                   | 12,44                 |             | 4           | Спальня                 | 15,07                 |             |             |                         |                       |
|             | 5           | Ванна кімната           | 4,44                  |             | 5           | Кухня                   | 16,60                 | 82          | 1           | Коридор                 | 4,59                  |
|             | 6           | Гардероб                | 2,40                  |             | 6           | Ванна кімната           | 4,92                  | 1К          | 2           | Спальня                 | 12,01                 |
|             | 7           | Туалет                  | 1,70                  |             | 7           | Гардероб                | 1,77                  |             | 3           | Кухня                   | 15,33                 |
|             | 8           | Лоджія                  | 3,93                  |             | 8           | Туалет                  | 1,88                  |             | 4           | Санвузол                | 4,91                  |
|             |             | Житлова площа квартири  | 27,09 м <sup>2</sup>  |             | 9           | Гардероб                | 3,03                  |             | 5           | Лоджія                  | 4,39                  |
|             |             | Площа квартири          | 54,81 м <sup>2</sup>  |             | 10          | Санвузол                | 3,15                  |             |             | Житлова площа квартири  | 12,01 м <sup>2</sup>  |
|             |             | Загальна площа квартири | 58,74 м <sup>2</sup>  |             | 11          | Лоджія                  | 4,35                  |             |             | Площа квартири          | 36,84 м <sup>2</sup>  |
|             |             |                         |                       |             | 12          | Балкон                  | 2,76                  |             |             | Загальна площа квартири | 41,23 м <sup>2</sup>  |
| 78          | 1           | Коридор                 | 8,19                  |             |             | Житлова площа квартири  | 42,63 м <sup>2</sup>  |             |             |                         |                       |
| 2К          | 2           | Спальня                 | 11,52                 |             |             | Площа квартири          | 85,60 м <sup>2</sup>  |             |             |                         |                       |
|             | 3           | Спальня                 | 12,02                 |             |             | Загальна площа квартири | 92,71 м <sup>2</sup>  |             |             |                         |                       |
|             | 4           | Кухня                   | 12,53                 |             |             |                         |                       |             |             |                         |                       |
|             | 5           | Санвузол                | 4,98                  |             |             |                         |                       |             |             |                         |                       |
|             | 6           | Лоджія                  | 3,95                  |             |             |                         |                       |             |             |                         |                       |
|             |             | Житлова площа квартири  | 23,54 м <sup>2</sup>  |             |             |                         |                       |             |             |                         |                       |
|             |             | Площа квартири          | 49,24 м <sup>2</sup>  |             |             |                         |                       |             |             |                         |                       |
|             |             | Загальна площа квартири | 53,19 м <sup>2</sup>  |             |             |                         |                       |             |             |                         |                       |

|           |                |      |       |        |      |   |         |
|-----------|----------------|------|-------|--------|------|---|---------|
| змін      | кільк.         | арк. | №док. | підпис | дата | 04-01/24  | АР      |
| ГП        | Зіньків А.Б.   |      |       |        |      | Нове будівництво багатоквартирного житлового будинку з приміщеннями громадського призначення, за адресою: пл. Авіації, 196, м. Новий Калинів, Самбірський район, Львівська область. |         |
| ГАП       | Головецький Н. |      |       |        |      | Багатоквартирний житловий будинок м. Новий Калинів, Львівська область. 1 черга будівництва.   |         |
| Виконав   | Попелястий Р.  |      |       |        |      | стадія  | аркуш   |
| Перевірив | Зіньків А.Б.   |      |       |        |      | П   | аркушів |
|           |                |      |       |        |      | 22  |         |
|           |                |      |       |        |      | Експлікація квартир 6 поверху. Секція №2 (Квартири 48-82)   |         |
|           |                |      |       |        |      | ФОП Никифорець І.І.   |         |

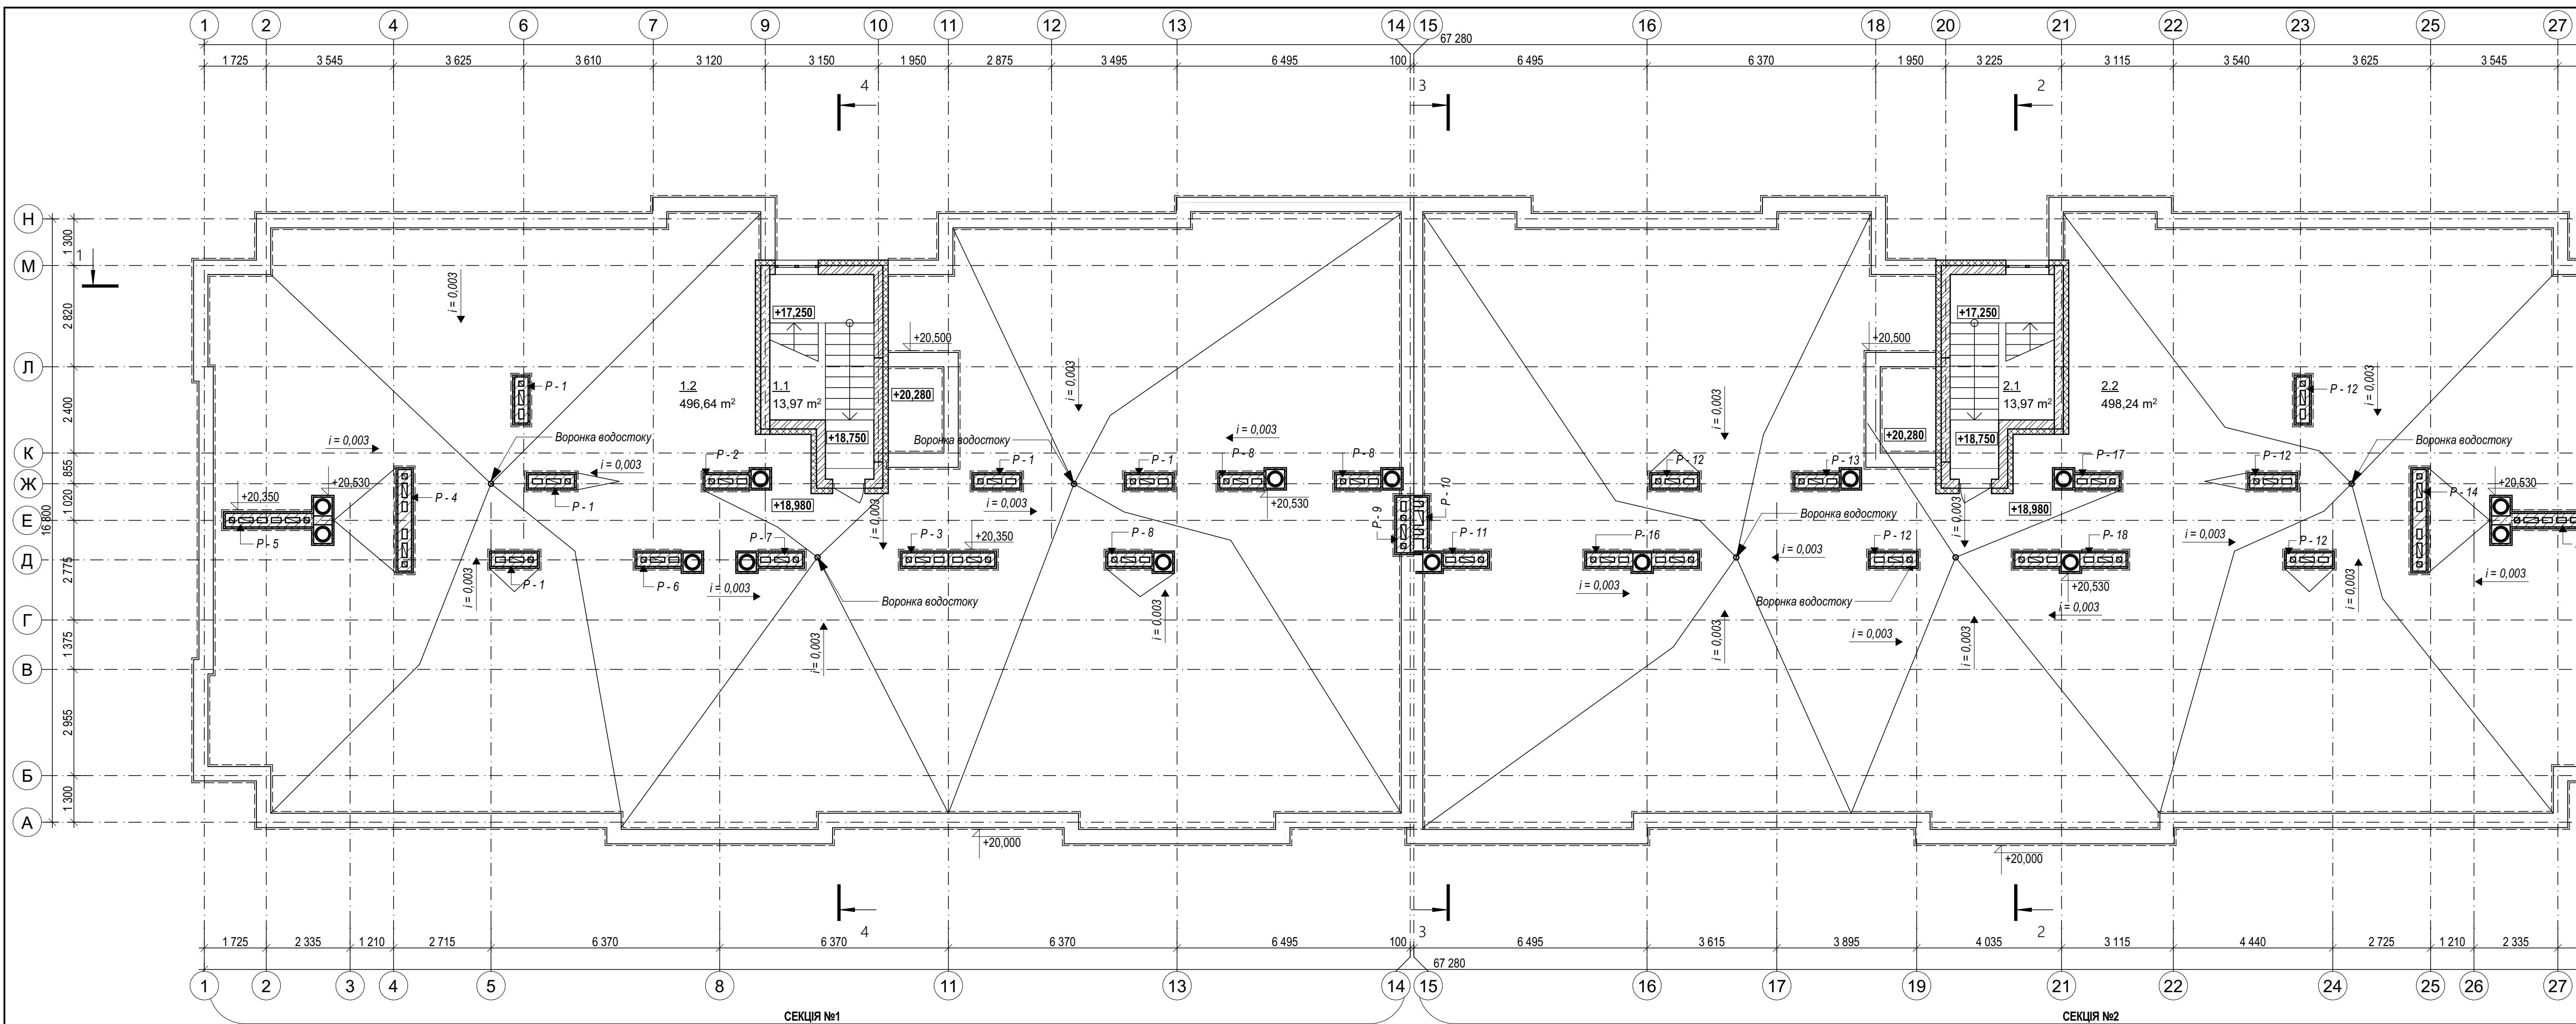

Експлікація приміщень

| №   | Найменування              | Площа, м <sup>2</sup> |
|-----|---------------------------|-----------------------|
| 1.1 | Сходова кітка (Секція №1) | 13,97                 |
| 2.1 | Сходова кітка (Секція №2) | 13,97                 |
|     | Загальна площа            | 2,94 м <sup>2</sup>   |
|     | Покриття даху (Секція №1) | 464 м <sup>2</sup>    |
|     | Покриття даху (Секція №2) | 498 м <sup>2</sup>    |
|     | Покриття даху. Всого      | 962 м <sup>2</sup>    |

Припис:

- Основні таємно-економічні позазнаки за залоги, див. арк. 2.
- Задовідмінні 0000 приняті реєнчісті підлоги першого поверху (Секція №2).
- Фасади ділянка 4-26.
- Розриви, ділянка 7-30.
- Розриви, ділянка 3-36.

|             |            |            |                   |
|-------------|------------|------------|-------------------|
| 0401 / 4    | Р          |            |                   |
| Зійків      | Арк № 0    | Лінії      | Дата              |
| П           | Лінії А.Б. | Г.П.       | Г.П. Голоцький Н. |
| Г.П.        | Лінії А.Б. | Лінії А.Б. | Лінії А.Б.        |
| Виконав     | Поміст Р.  | Поміст Р.  | Поміст Р.         |
| Перевірив   | Лінії А.Б. | Лінії А.Б. | Лінії А.Б.        |
| Планокрівля | 18.80      | 11.00      | Фото              |
|             |            |            | Фото              |






Приписки:

- Основні та коефіцієнти піказники залагні див. ар.
- Змінну відміну 0,00 принять рівною чистої підвищеної поверхні (Секція №2).
- Кольористика фасадів див. розділ "Організація фасадів".

0401 / 4

| Нове будівництво багатоквартирного житлового будинку з приміщеннями для соціального призначення, за адресою: г. Авдіївка, 16, вул. Новий Калінів, Сімферопольський район, Львівська область. |            | Багатоквартирний житловий будинок № 16, вул. Новий Калінів, Львівська область, і членів будівництва. |            |
|--|------------|--|------------|
| стад   | окуп       | стад   | окуп       |
| 1  | 2          | 1  | 2          |
| Фасад 28-1   | Фасад 28-1 | Фасад 28-1   | Фасад 28-1 |

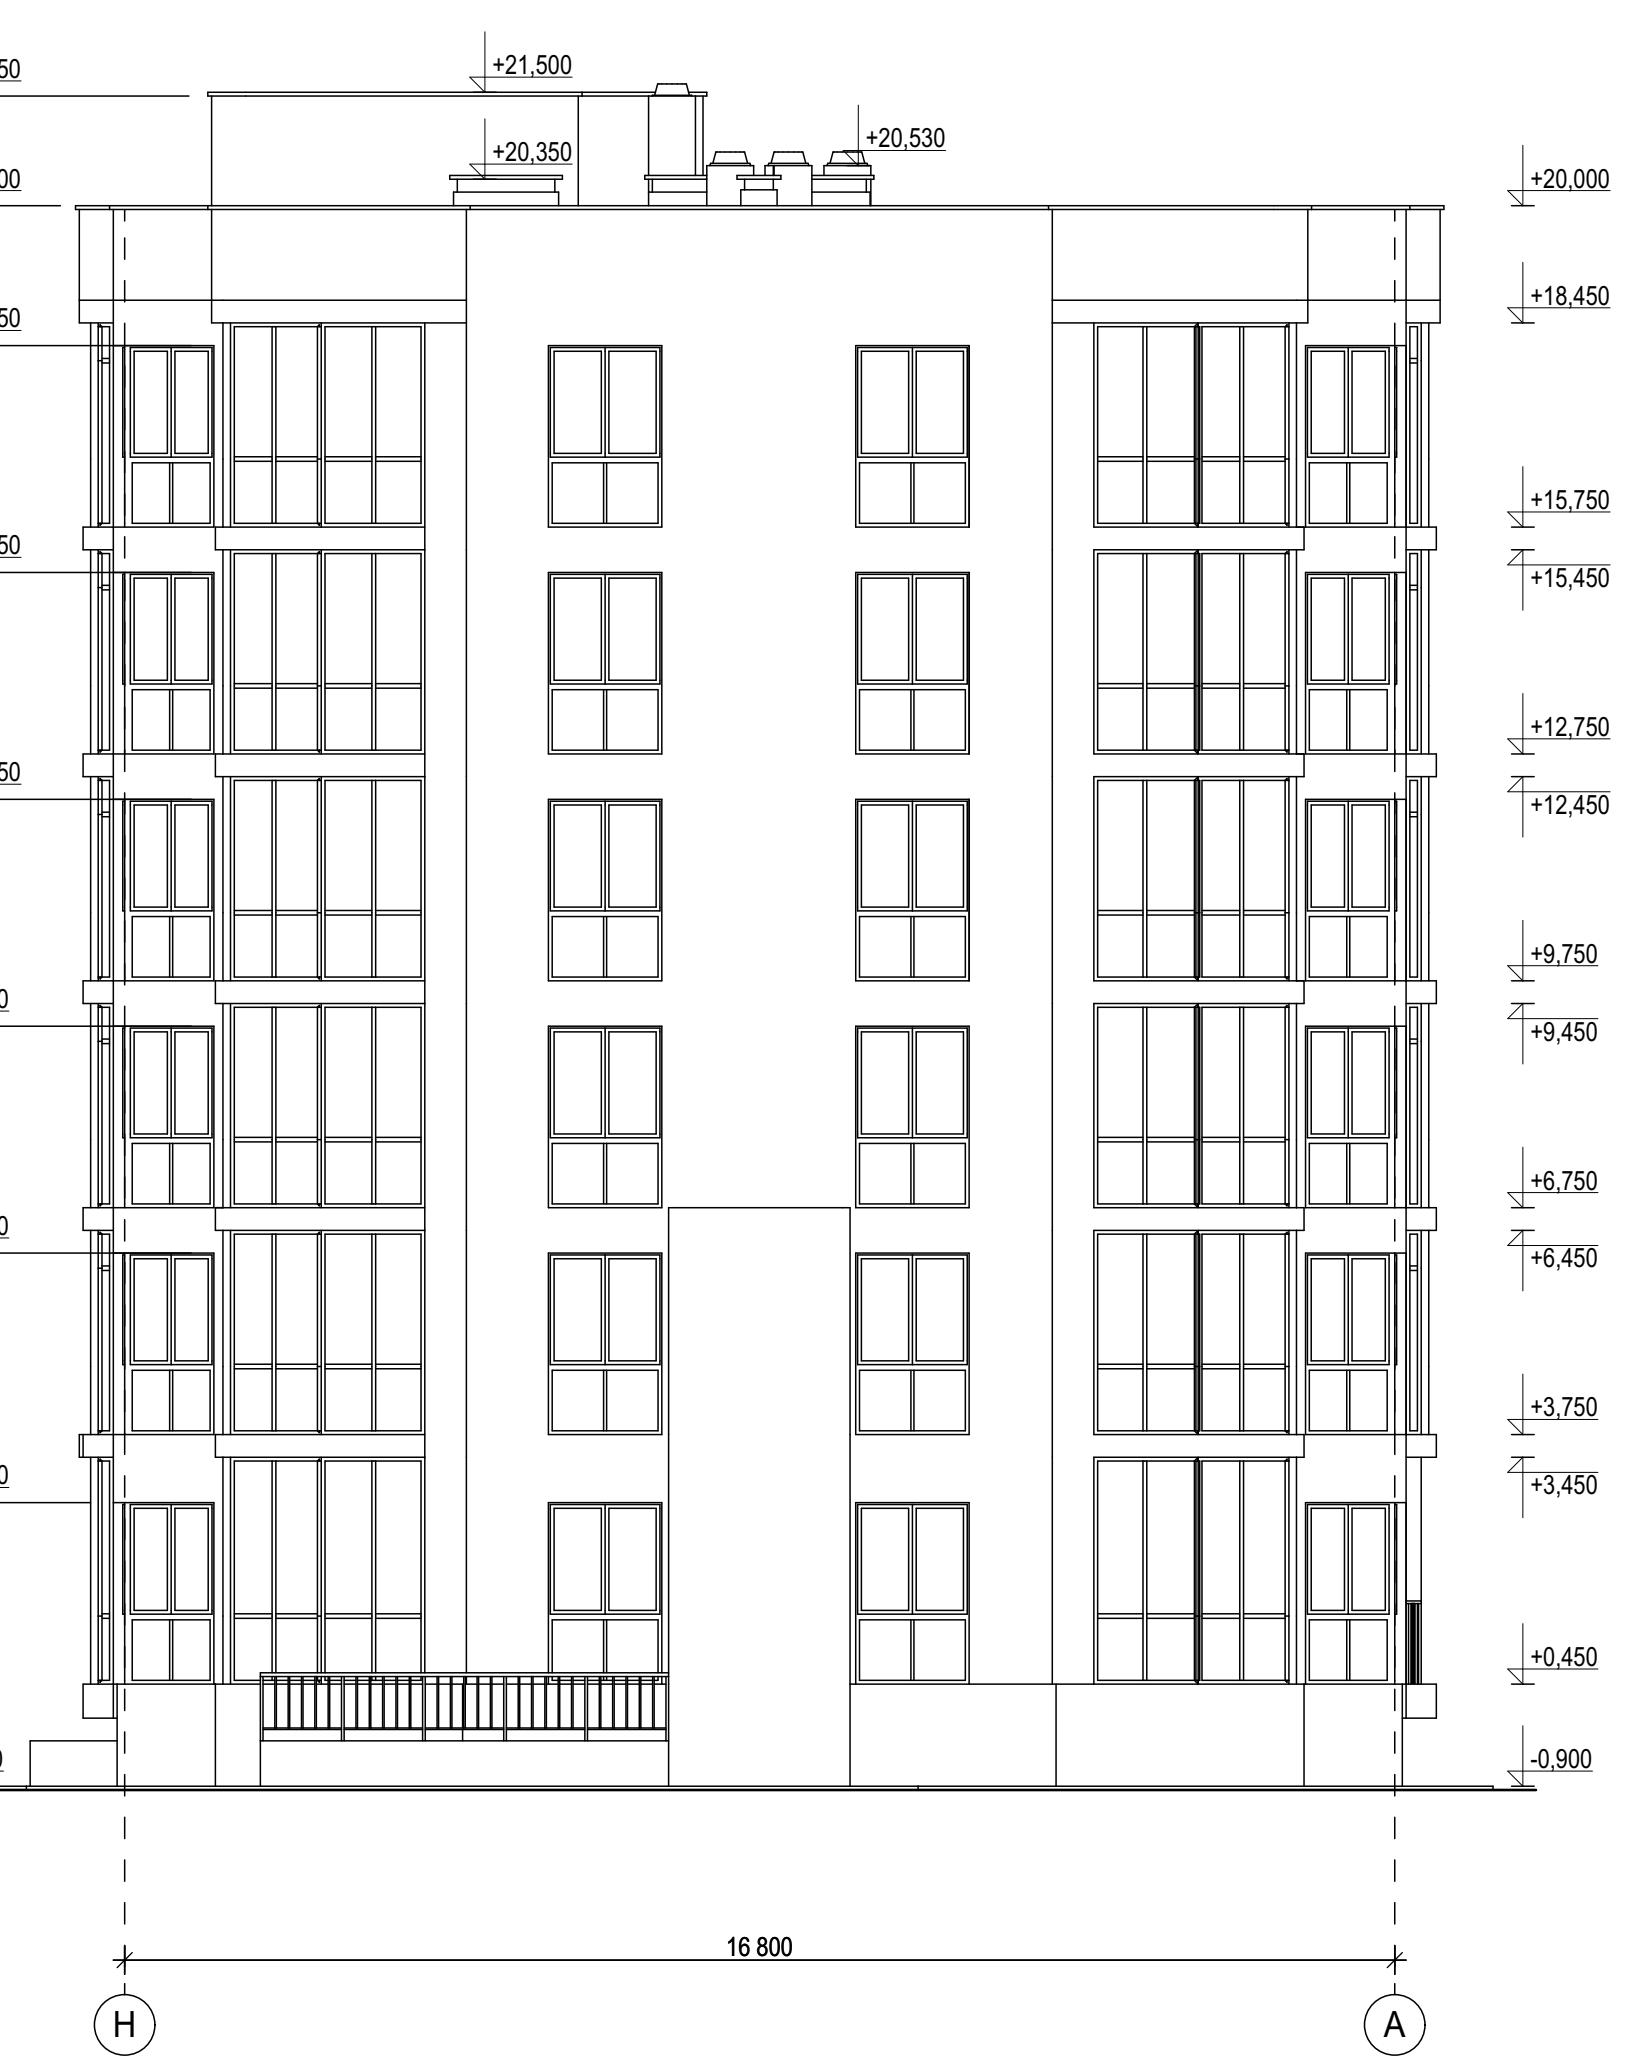

| змін  | кільк. | арк. | №док. | підпис | дата                  |
|---|--------|------|-------|--------|-----------------------|
| ПП  |        |      |       |        |                       |
| ГАП   |        |      |       |        |                       |
| Виконав                                     |        |      |       |        |                       |
| Перевірив                                   |        |      |       |        |                       |
| Фасад в осіах А-Н. Фасад в осіах Н-А М1:100 |        |      |       |        | Ф.О.Н.Никифорець І.І. |

**Примітки:**  
 1. Основні техніко-економічні показники та загальні дії див. арк. 2.  
 2. За умовну відмітку 0,000 прийнято рівень чистої підлоги первого поверху (Секція №2).  
 3. Кольористика фасадів див. розділ "Опорядження фасадів"

04-01/24

АР

Нове будівництво багатоквартирного житлового будинку з приміщеннями громадського призначення, за адресою: г. Аїзівщина, 196, м. Новий Калинів, Самбірський район, Львівська область.

Багатоквартирний житловий будинок м. Новий Калинів, Львівська область. 1 черга будівництва.

стадія аркуш аркуш

1 26




**Примітки:**  
1. Основні техніко-економічні показники та загальні дані див. арк. 2.  
2. За умовну відмітку 0,000 прийнято рівень чистої підлогочного поверху (Секція №2).

00  
00

|          |  |
|----------|--|
| 04-01/24 | Нове будівництво багатоквартирного житлового будинку з приміщеннями громадського призначення, за адресою: вул. Івана Франка, 196, м. Новий Калинів, Самбірський район, Львівська область |
|----------|--|

багатоквартирний житловий будинок  
м. Новий Калинів, Львівська область.  
1 черга будівництва.


Розріз 1-1 М1:100

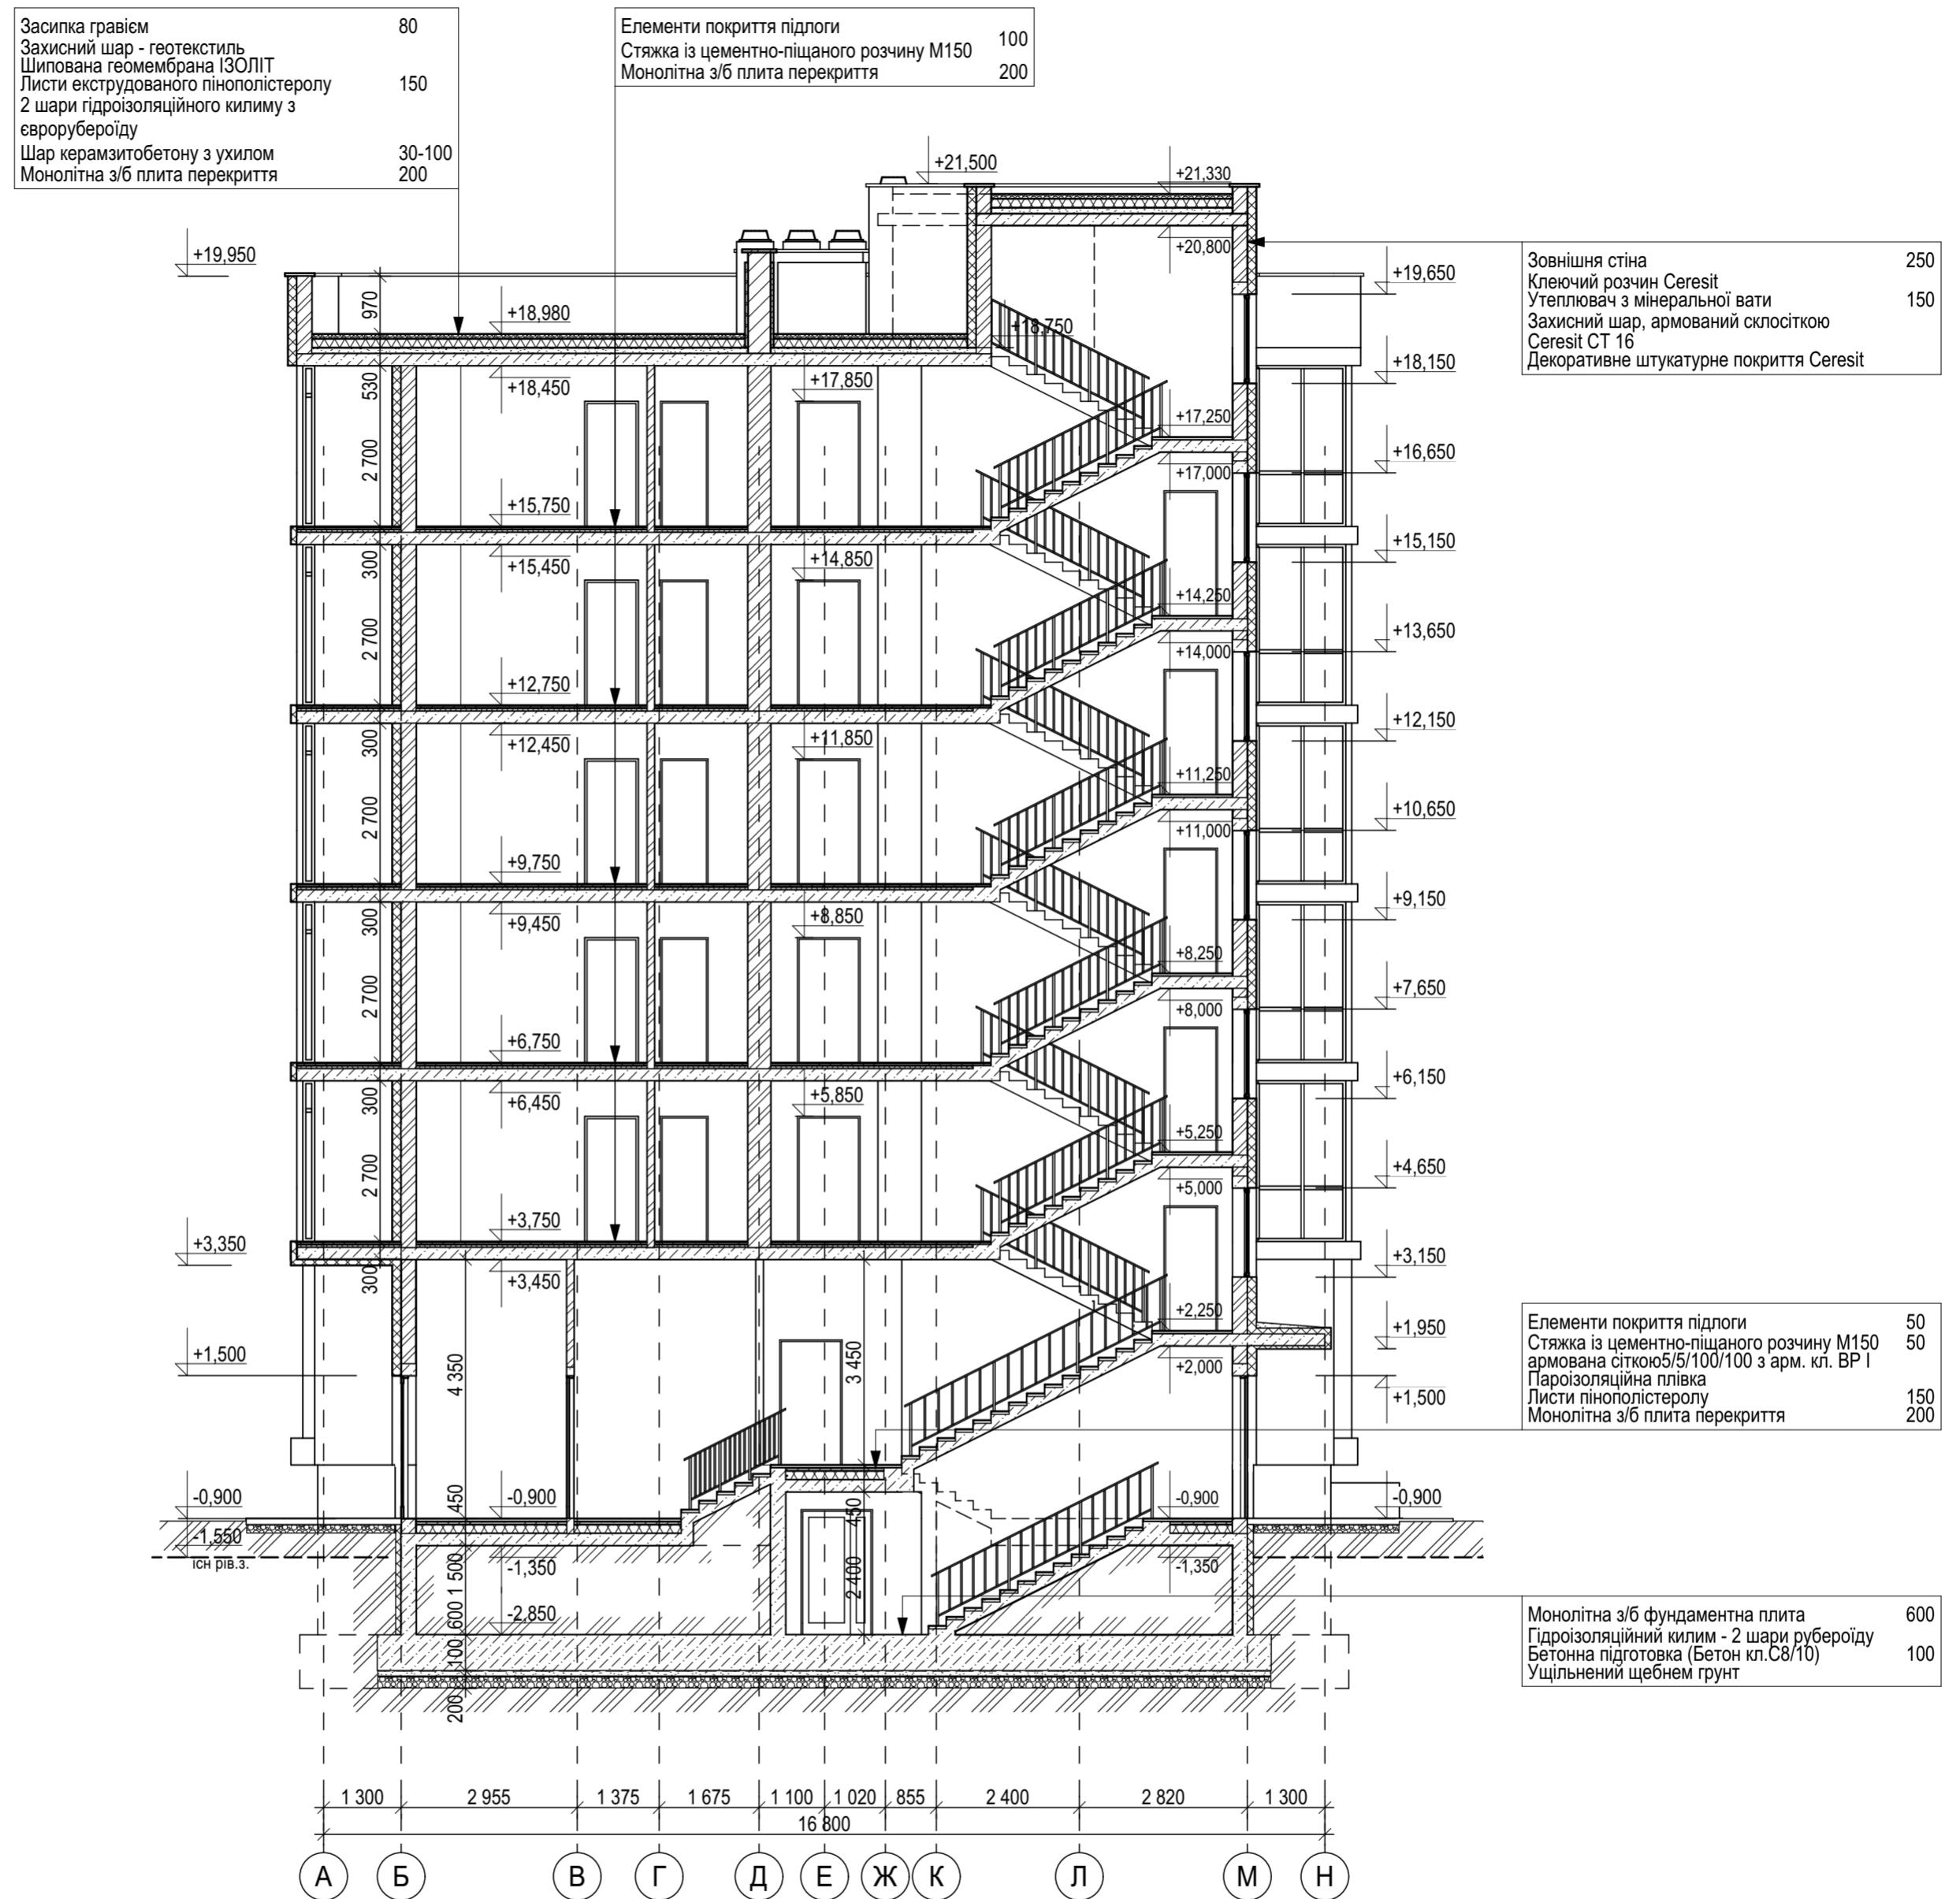

### Примітки:

1. Основні техніко-економічні показники та загальні дані див. арк. 2.
  2. За умовну відмітку 0,000 прийнято рівень чистої підлоги першого поверху (Секція №2).
  3. Лінії розрізів показані на планах поверхів.


|           |                |      |       |        |   |                     |
|-----------|----------------|------|-------|--------|---|---------------------|
|           |                |      |       |        | 04-01/24  | АР                  |
|           |                |      |       |        | Нове будівництво багатоквартирного житлового будинку з приміщеннями громадського призначення, за адресою: пл. Авіації, 19б, м. Новий Калинів, Самбірський район, Львівська область. |                     |
| змін      | кільк.         | арк. | №док. | підпис | дата  |                     |
| ГП        | Зіньків А.Б    |      |       |        | Багатоквартирний житловий будинок<br>м. Новий Калинів, Львівська область.<br>1 черга будівництва.   | стадія              |
| ГАП       | Головецький Н. |      |       |        |   | аркуш               |
| Виконав   | Попелястий Р.  |      |       |        |   | аркушів             |
| Перевірив | Зіньків А.Б    |      |       |        | Розріз 2-2 М1:100   | ФОП Никифорець І.І. |

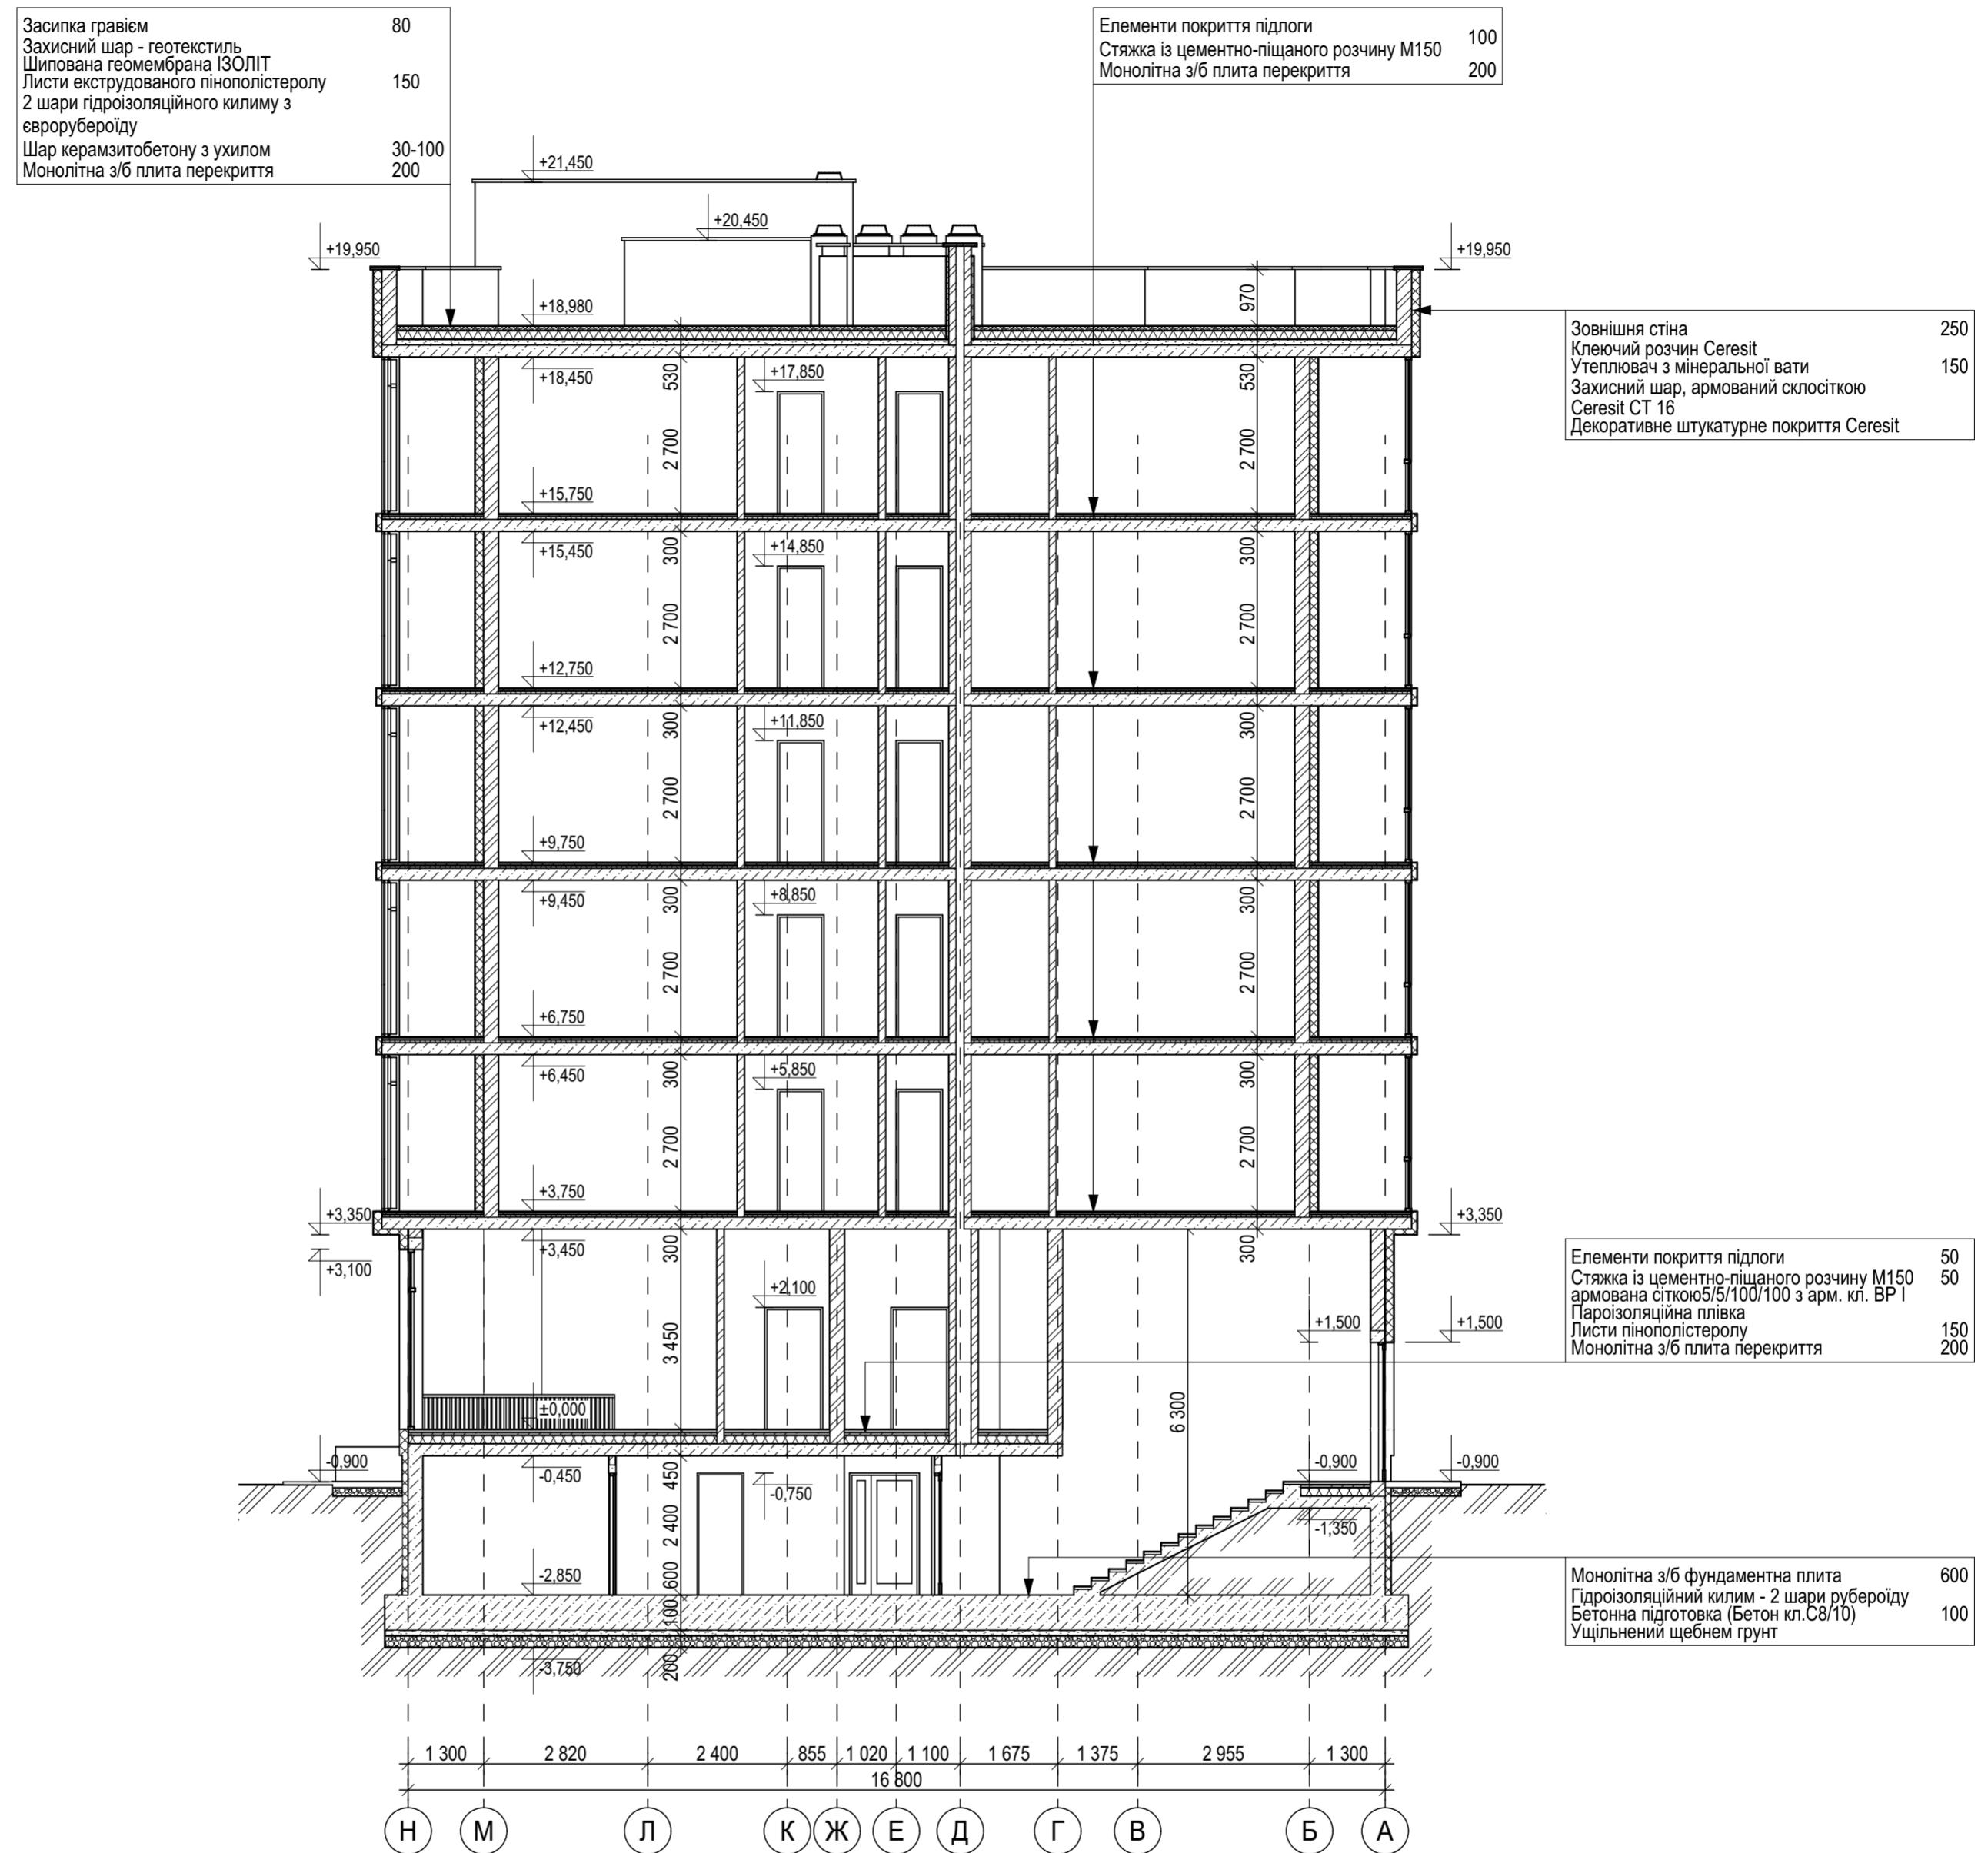

### Примітки:

1. Основні техніко-економічні показники та загальні дані див. арк. 2.
  2. За умовну відмітку 0,000 прийнято рівень чистої підлоги першого поверху (Секція №2).
  3. Лінії розрізів показані на планах поверхів.

|           |                |      |       |        |   |         |
|-----------|----------------|------|-------|--------|---|---------|
|           |                |      |       |        | 04-01/24  | АР      |
|           |                |      |       |        | Нове будівництво багатоквартирного житлового будинку з приміщеннями громадського призначення, за адресою: пл. Авіації, 196, м. Новий Калинів, Самбірський район, Львівська область. |         |
| змін      | кільк.         | арк. | №док. | підпис | дата  |         |
| ГП        | Зіньків А.Б    |      |       |        | Багатоквартирний житловий будинок<br>м. Новий Калинів, Львівська область.<br>1 черга будівництва.   | стадія  |
| ГАП       | Головецький Н. |      |       |        |   | аркуш   |
| Виконав   | Попелястий Р.  |      |       |        |   | аркушів |
| Перевірив | Зіньків А.Б    |      |       |        | Розріз 3-3 М1:100   |         |
|           |                |      |       |        | ФОП Никифорець І.І.   |         |

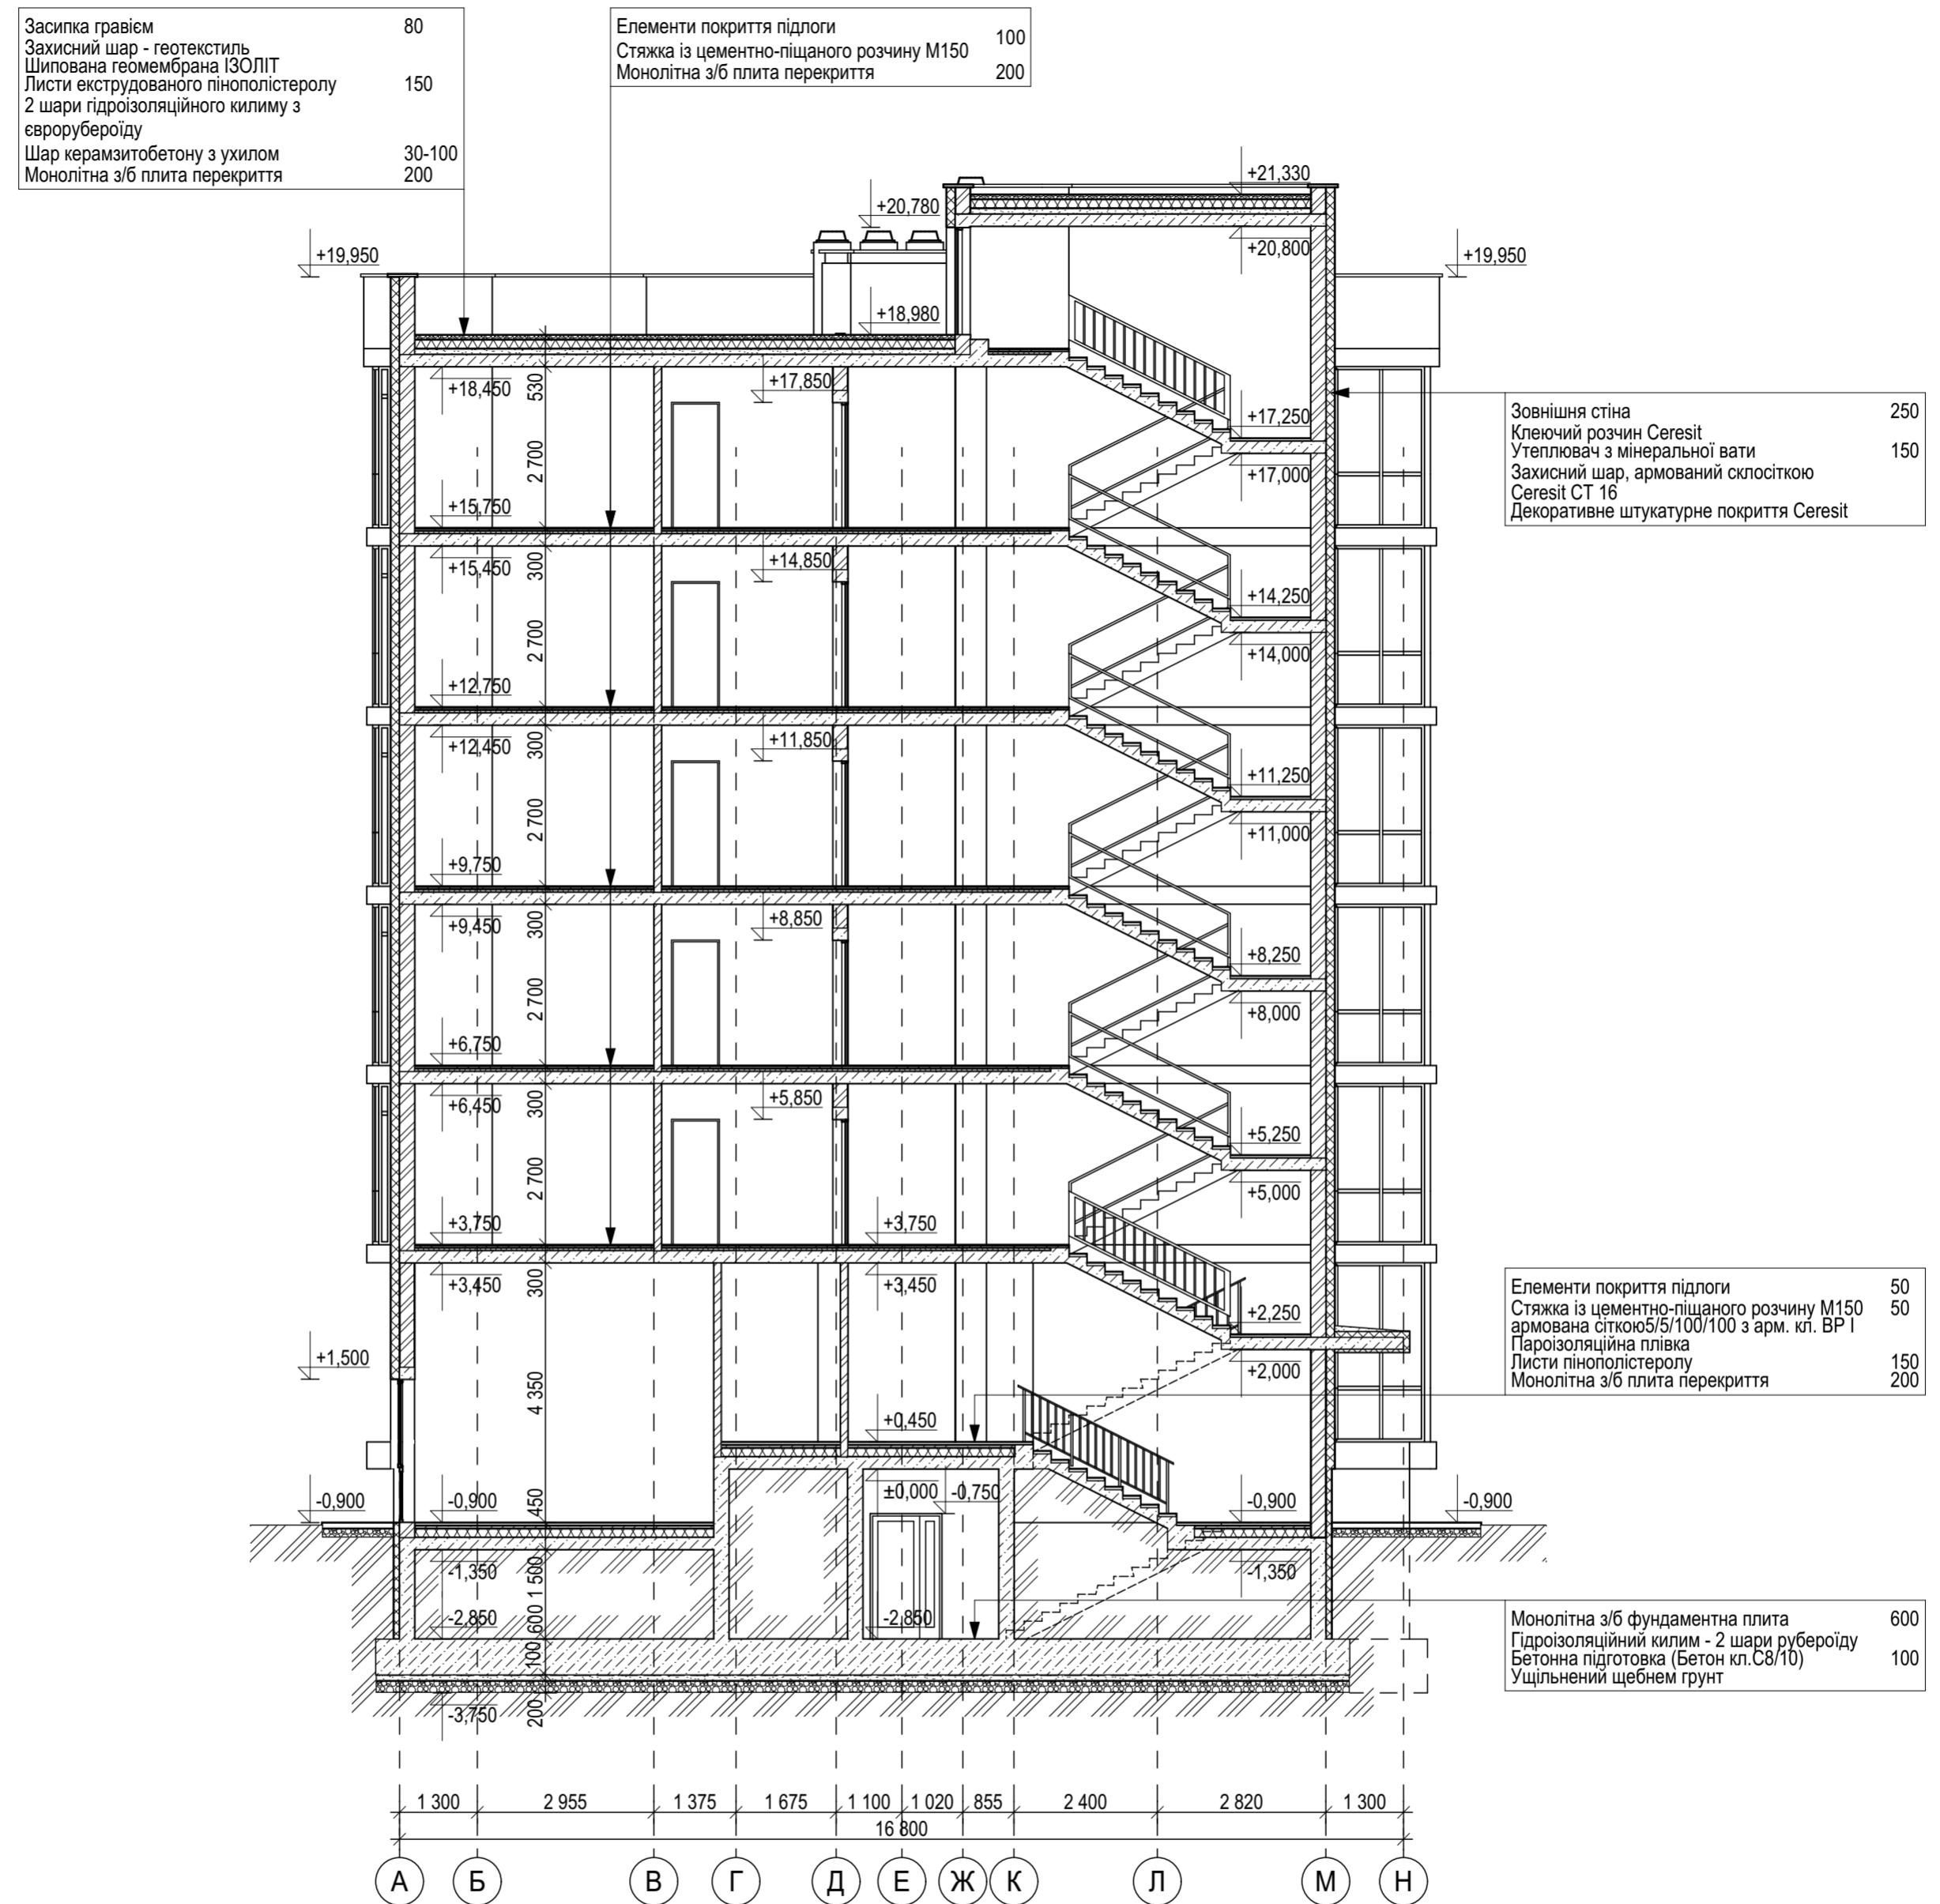


### Примітки:


1. Основні техніко-економічні показники та загальні дані див. арк. 2.
  2. За умовну відмітку 0,000 прийнято рівень чистої підлоги першого поверху (Секція №2).
  3. Лінії розрізів показані на планах поверхів.

|           |                |      |       |        |   |         |
|-----------|----------------|------|-------|--------|---|---------|
|           |                |      |       |        | 04-01/24  | АР      |
|           |                |      |       |        | Нове будівництво багатоквартирного житлового будинку з приміщеннями громадського призначення, за адресою: пл. Авіації, 196, м. Новий Калинів, Самбірський район, Львівська область. |         |
| змін      | кільк.         | арк. | №док. | підпис | дата  |         |
| ГП        | Зіньків А.Б    |      |       |        | Багатоквартирний житловий будинок<br>м. Новий Калинів, Львівська область.<br>1 черга будівництва.   | стадія  |
| ГАП       | Головецький Н. |      |       |        |   | аркуш   |
| Виконав   | Попелястий Р.  |      |       |        |   | аркушів |
| Перевірив | Зіньків А.Б    |      |       |        | Розріз 4-4 М1:100   |         |
|           |                |      |       |        | ФОП Никифорець І.І.   |         |


## Розгорта P-1

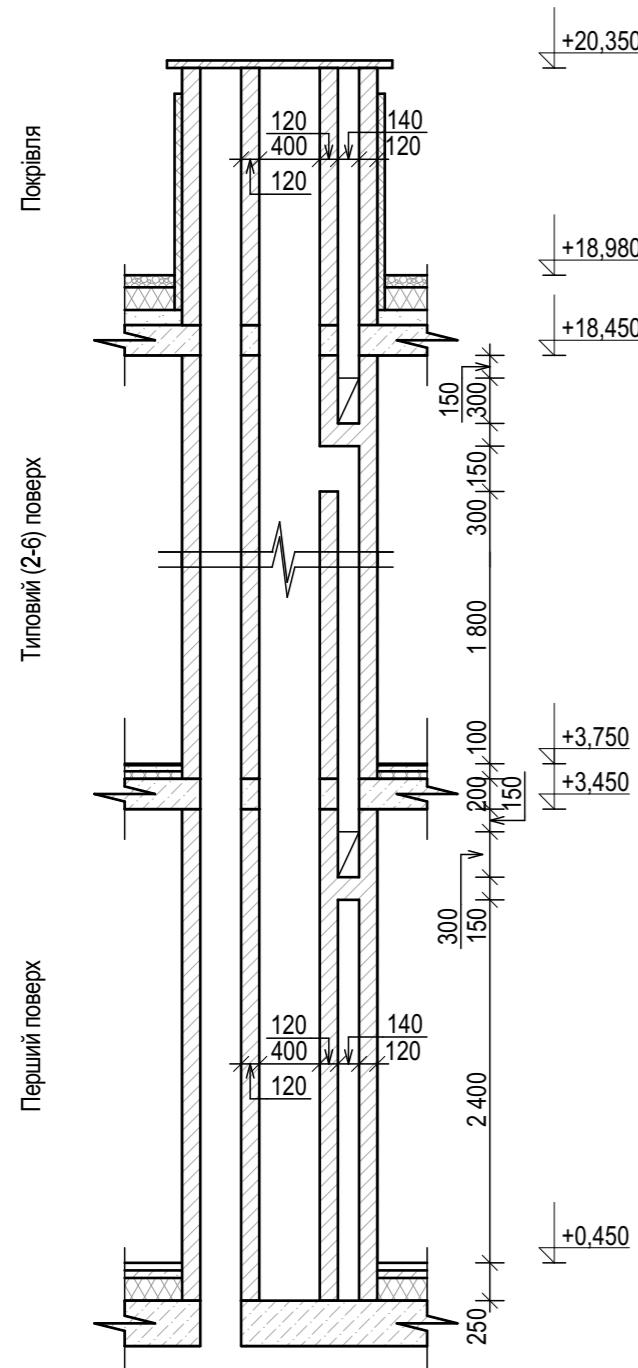

## Розгорта P-2

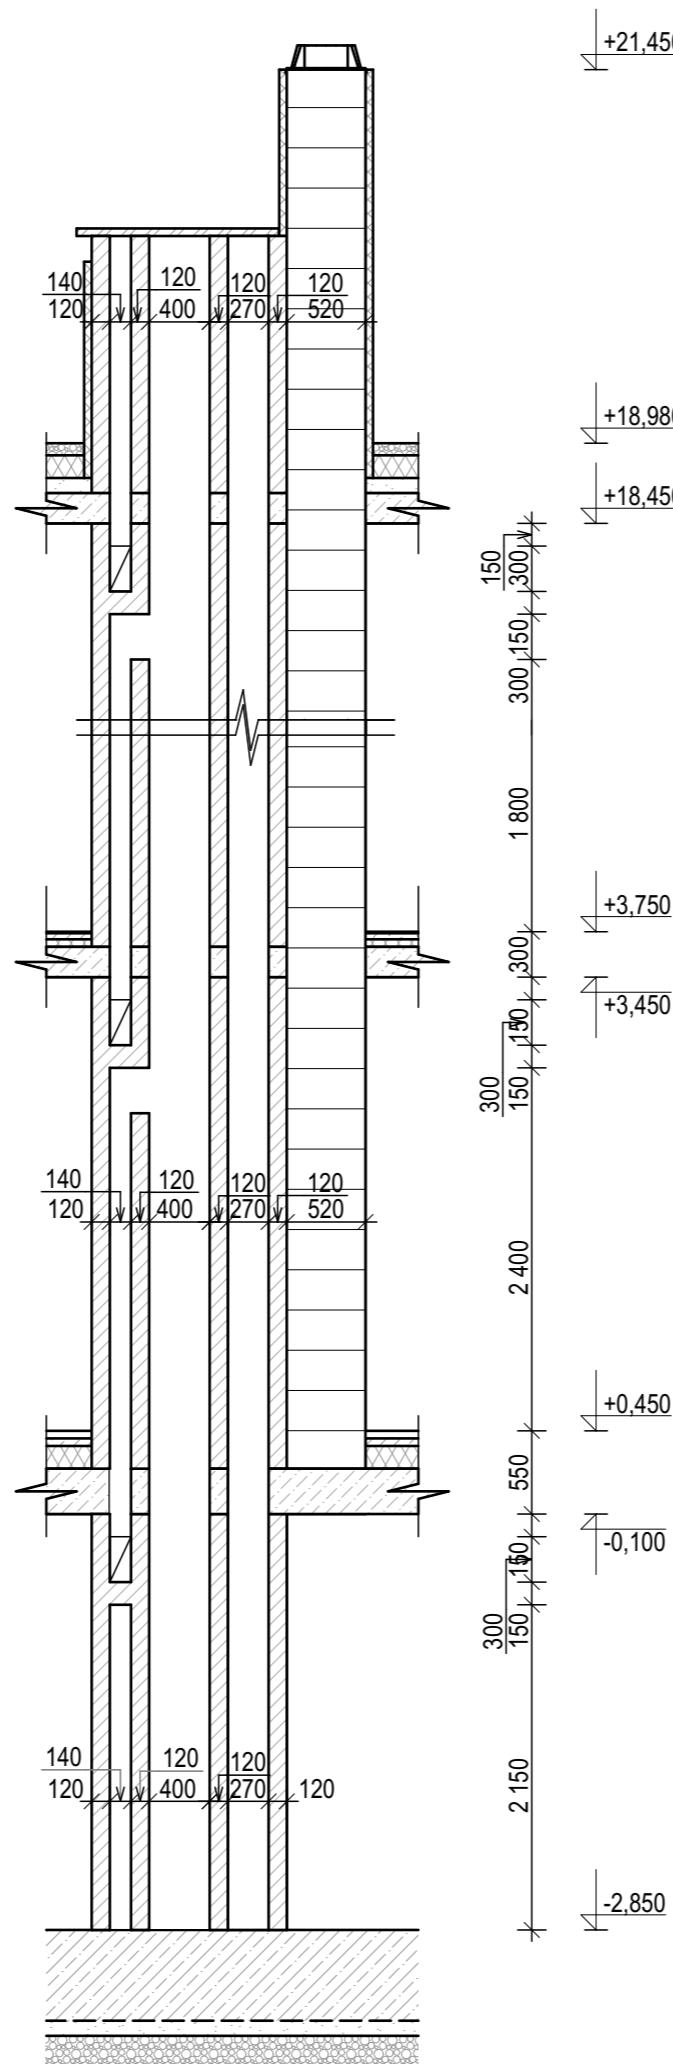

### Розгорта P-3

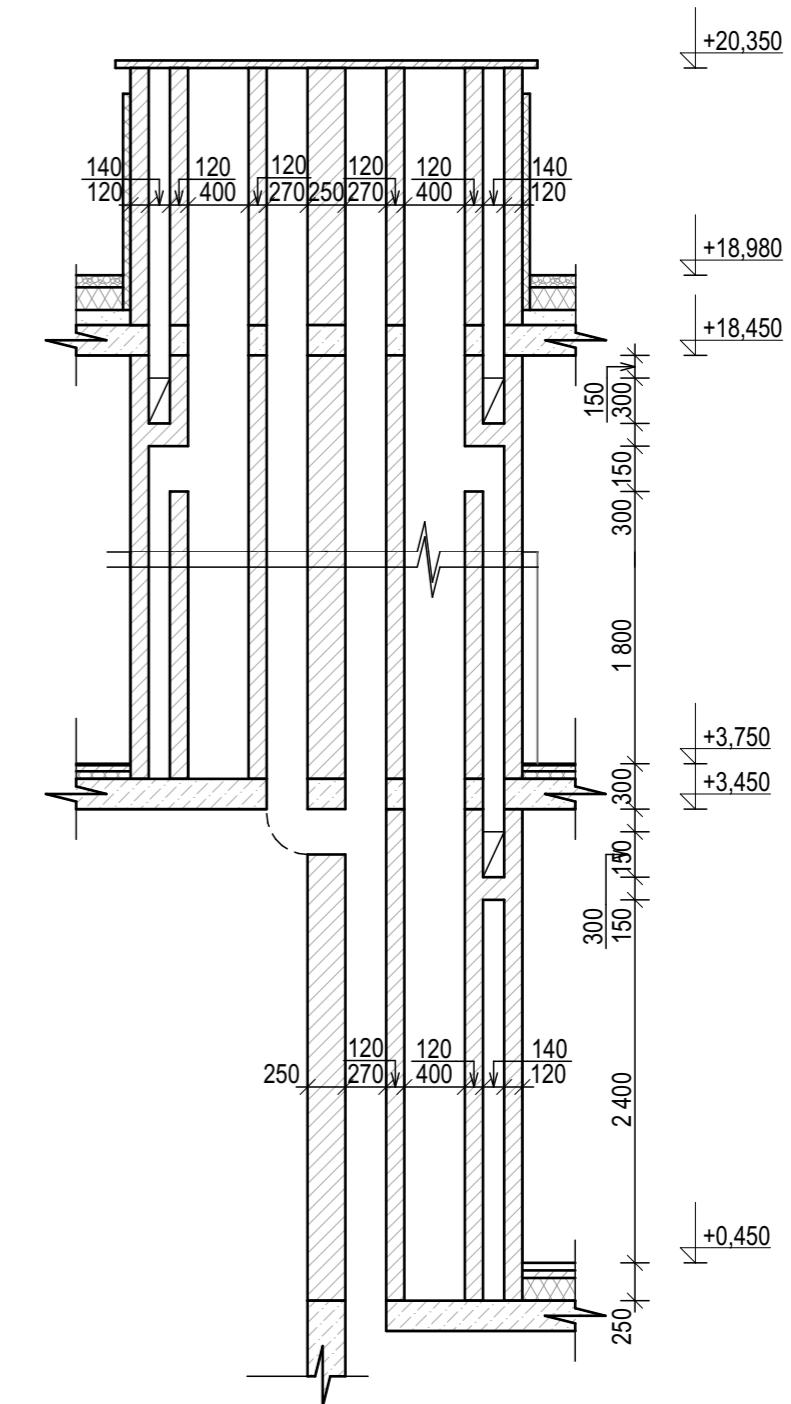


### Примітки:


1. Поквартирне опалення опалення здійснюється системою колективного димовидалення. Див. розділ ОВ (Опалення та вентиляція).
  2. Вентиляція приміщень здійснюється через вентиляційні шахти - виконані з керамічної цегли.

|           |                |      |       |        |   |                     |
|-----------|----------------|------|-------|--------|---|---------------------|
|           |                |      |       |        | 04-01/24  | АР                  |
|           |                |      |       |        | Нове будівництво багатоквартирного житлового будинку з приміщеннями громадського призначення, за адресою: пл. Авіації, 19б, м. Новий Калинів, Самбірський район, Львівська область. |                     |
| змін      | кільк.         | арк. | №док. | підпис | дата  |                     |
| ГП        | Зіньків А.Б    |      |       |        | Багатоквартирний житловий будинок<br>м. Новий Калинів, Львівська область.<br>1 черга будівництва.   | стадія              |
| ГАП       | Головецький Н. |      |       |        |   | аркуш               |
| Виконав   | Попелястий Р.  |      |       |        |   | аркушів             |
| Перевірив | Зіньків А.Б    |      |       |        | Розгортка вентиляційних каналів М1:50   | ФОП Никифорець І.І. |


## Розгортка Р-6

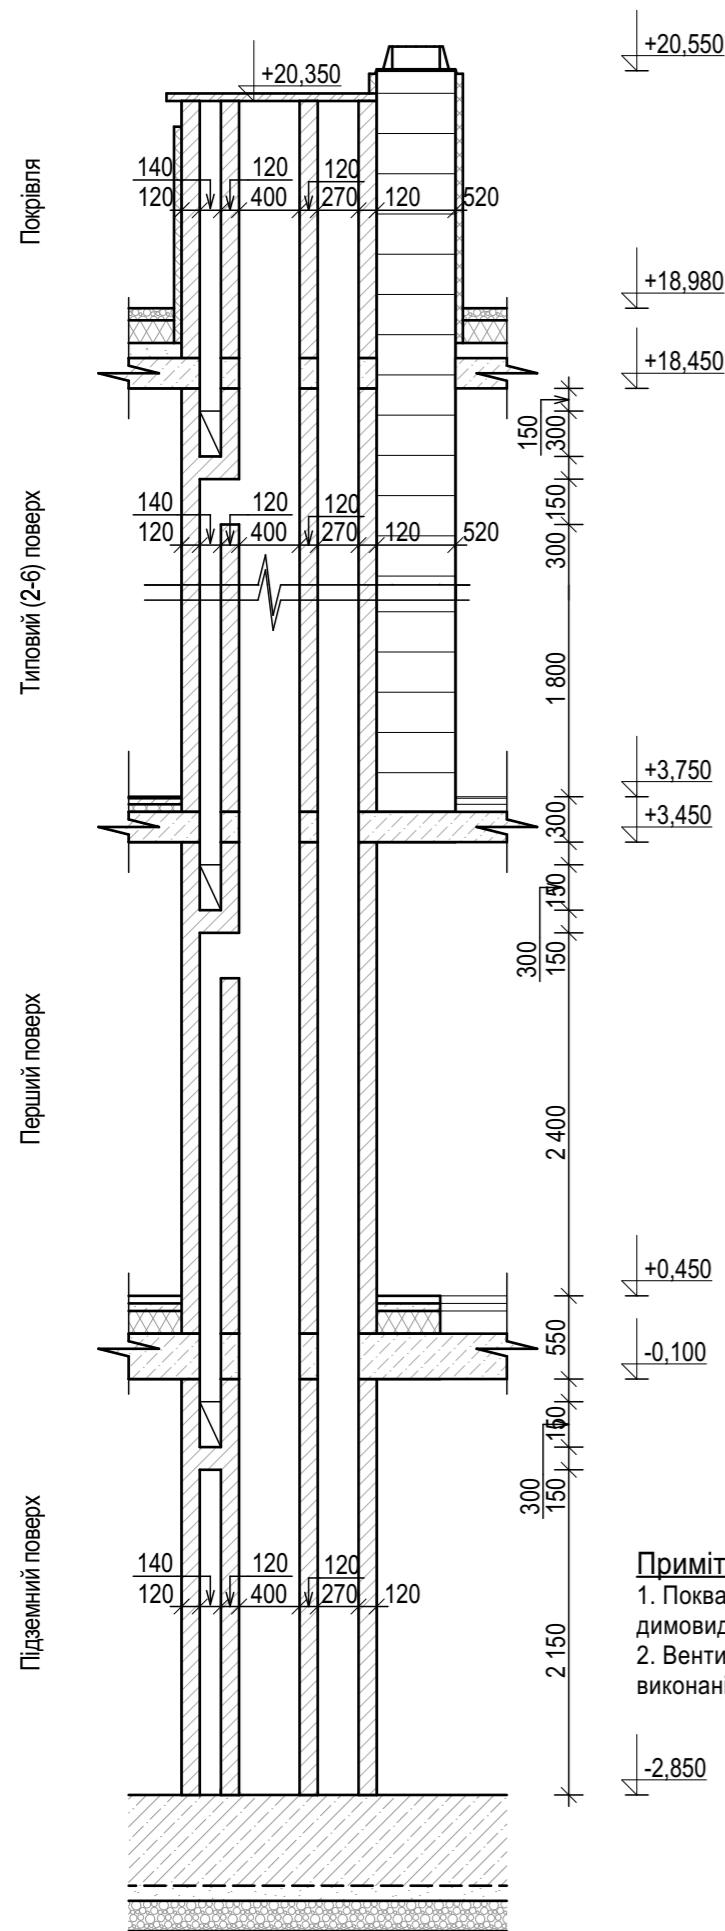

## Розгорта Р-4

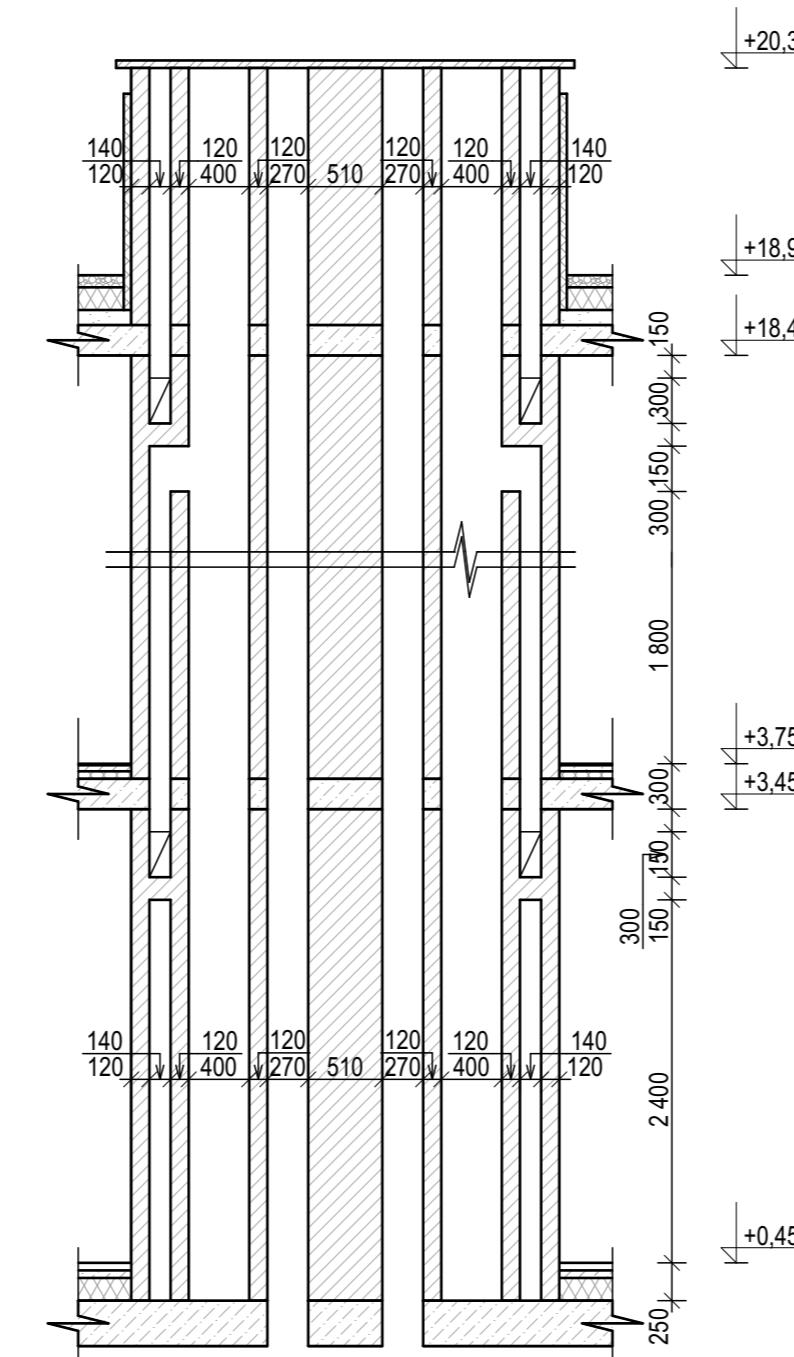

## Розгорта P-5

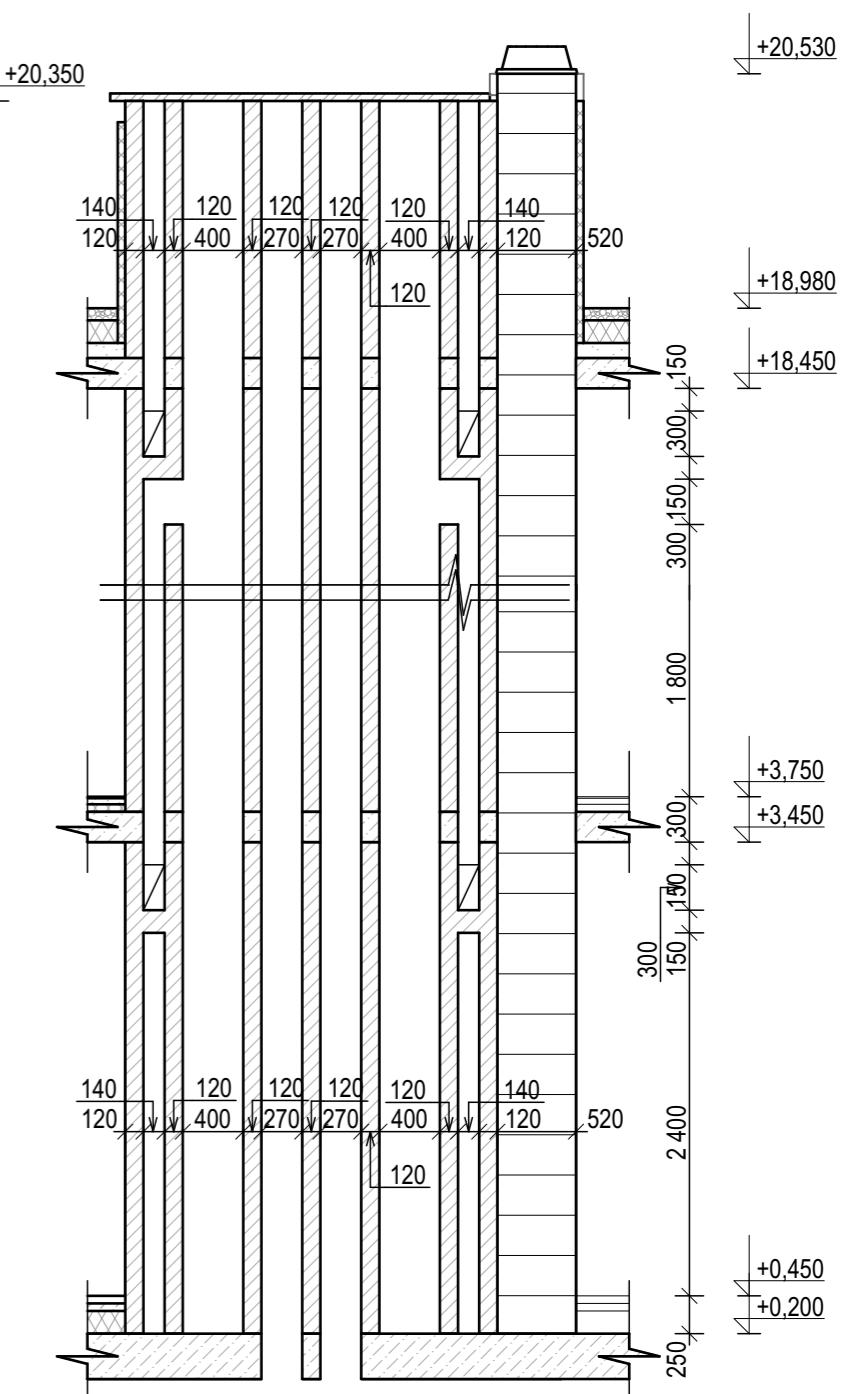


## Примітки


1. Поквартирне опалення опалення здійснюється системою колективного димовидалення. Див. розділ ОВ (Опалення та вентиляція).
  2. Вентиляція приміщень здійснюється через вентиляційні шахти - виконані з керамічної цегли.

|           |        |                |       |   |      |   |         |
|-----------|--------|----------------|-------|---|------|---|---------|
|           |        |                |       |   |      | 04-01/24  | АР      |
|           |        |                |       |   |      | Нове будівництво багатоквартирного житлового будинку з приміщеннями громадського призначення, за адресою: пл. Авіації, 196, м. Новий Калинів, Самбірський район, Львівська область. |         |
| змін      | кільк. | арк.           | №док. | підпис  | дата |   |         |
| ГП        |        | Зіньків А.Б    |       |  |      | Багатоквартирний житловий будинок<br>м. Новий Калинів, Львівська область.<br>1 черга будівництва.   | стадія  |
| ГАП       |        | Головецький Н. |       |  |      |   | аркуш   |
| Виконав   |        | Попелястий Р.  |       |  |      | Розгортка вентиляційних каналів М1:50   | аркушів |
| Перевірив |        | Зіньків А.Б    |       |  |      |   |         |


## Розгорта P-7

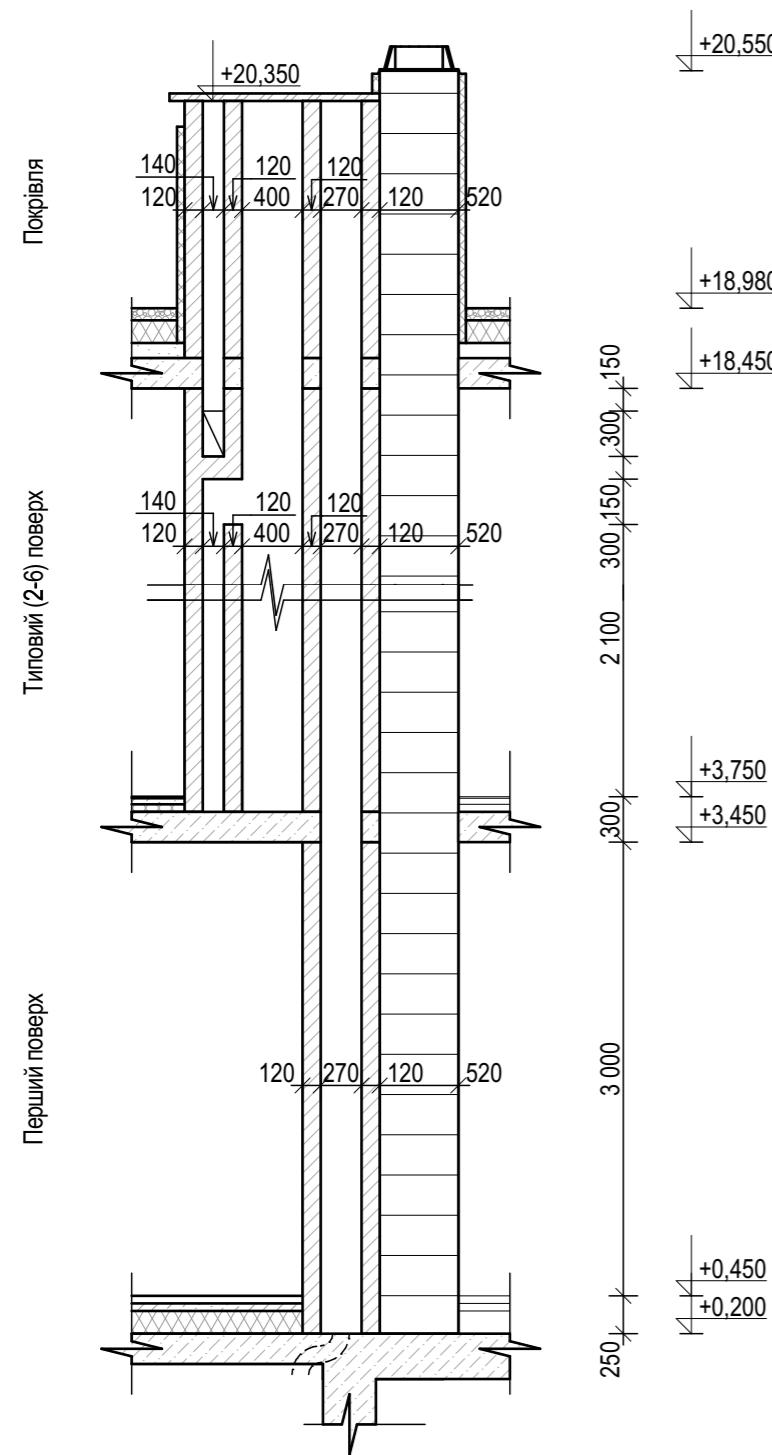

## Розгорта P-8

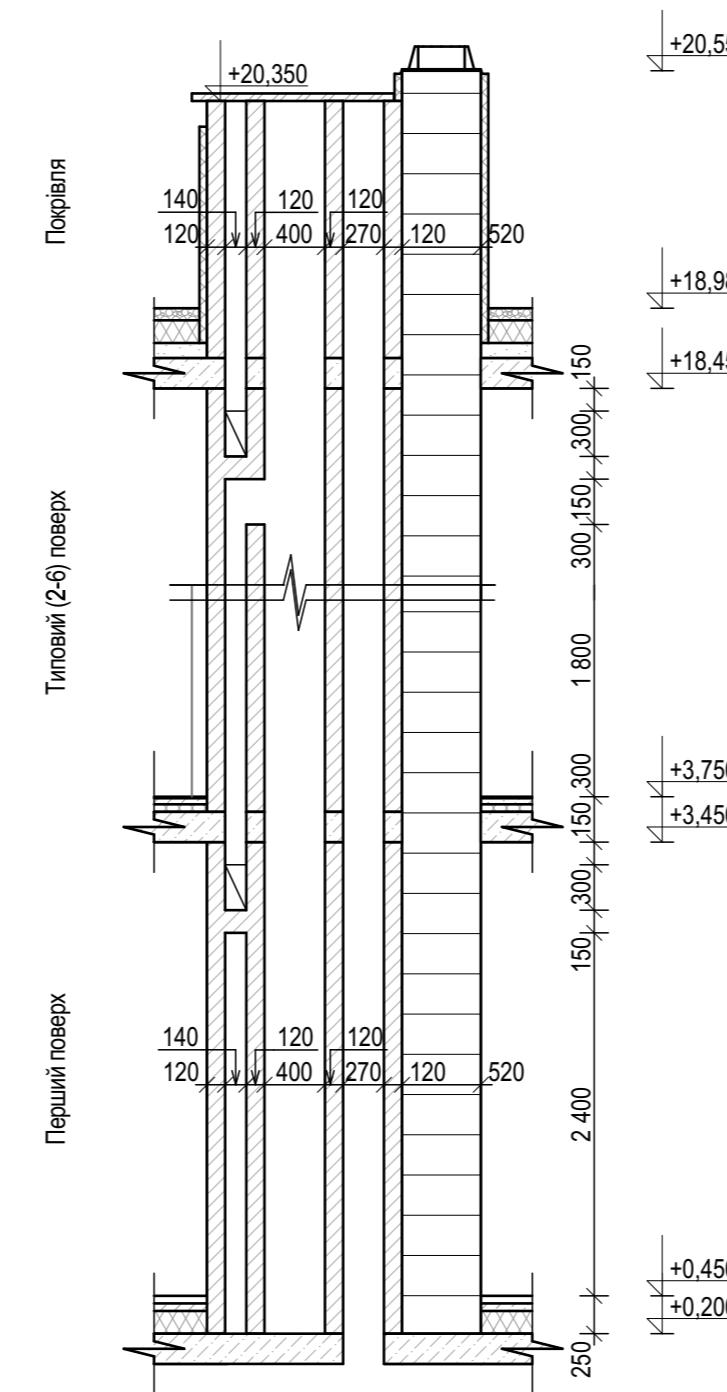

## Розгорта P-9

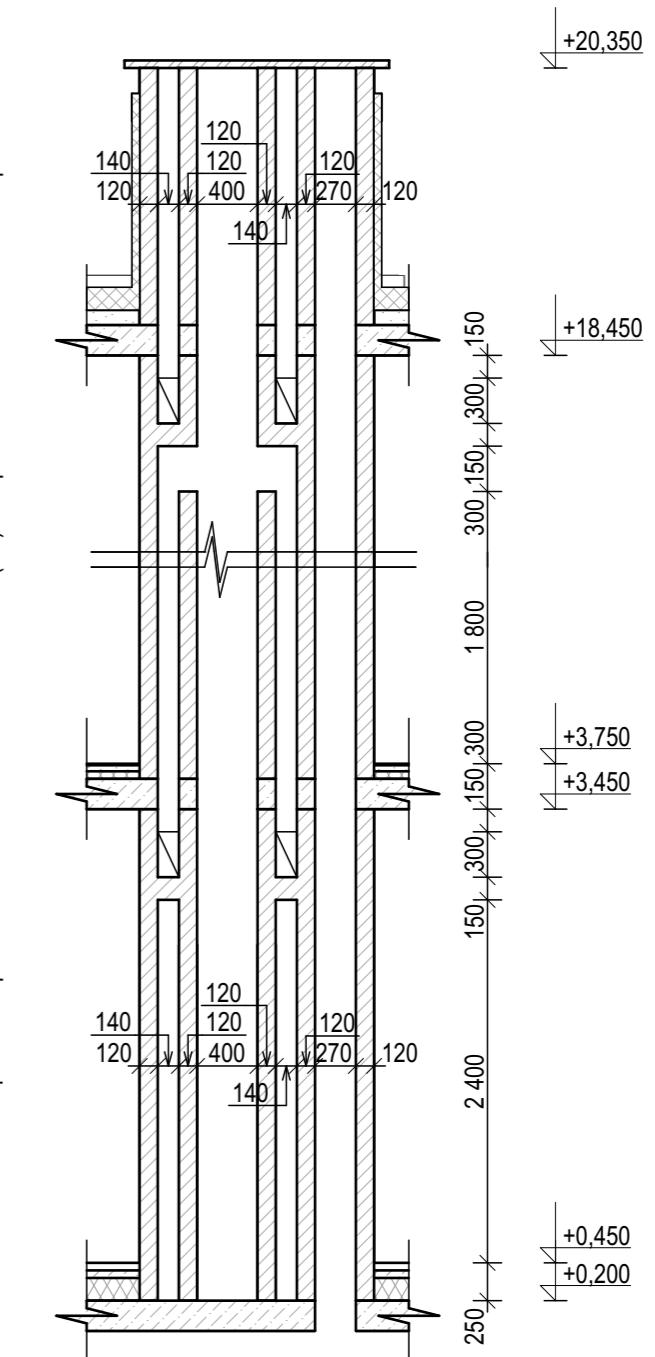


### Примітки:


1. Поквартирне опалення опалення здійснюється системою колективного димовидалення. Див. розділ ОВ (Опалення та вентиляція).
  2. Вентиляція приміщень здійснюється через вентиляційні шахти - виконані з керамічної цегли.

|           |                |      |       |        |   |                     |
|-----------|----------------|------|-------|--------|---|---------------------|
|           |                |      |       |        | 04-01/24  | АР                  |
|           |                |      |       |        | Нове будівництво багатоквартирного житлового будинку з приміщеннями громадського призначення, за адресою: пл. Авіації, 196, м. Новий Калинів, Самбірський район, Львівська область. |                     |
| змін      | кільк.         | арк. | №док. | підпис | дата  |                     |
| ГП        | Зіньків А.Б    |      |       |        | Багатоквартирний житловий будинок<br>м. Новий Калинів, Львівська область.<br>1 черга будівництва.   | стадія              |
| ГАП       | Головецький Н. |      |       |        |   | аркуш               |
| Виконав   | Попелястий Р.  |      |       |        |   | аркушів             |
| Перевірив | Зіньків А.Б    |      |       |        | Розгортка вентиляційних каналів М1:50   | ФОП Никифорець І.І. |


## Розгорта P-10

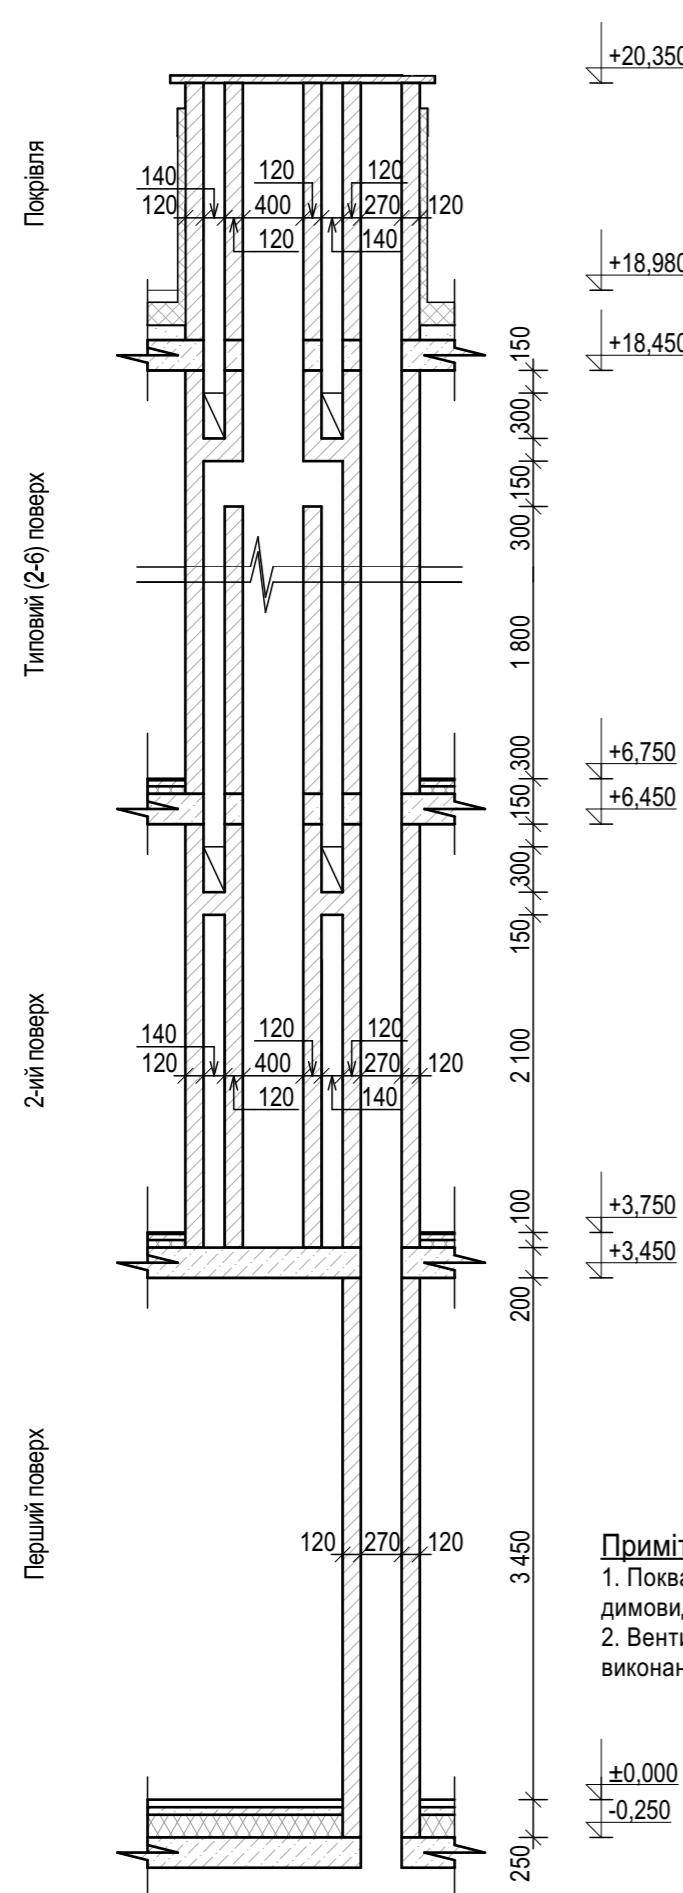

## Розгорта Р-1

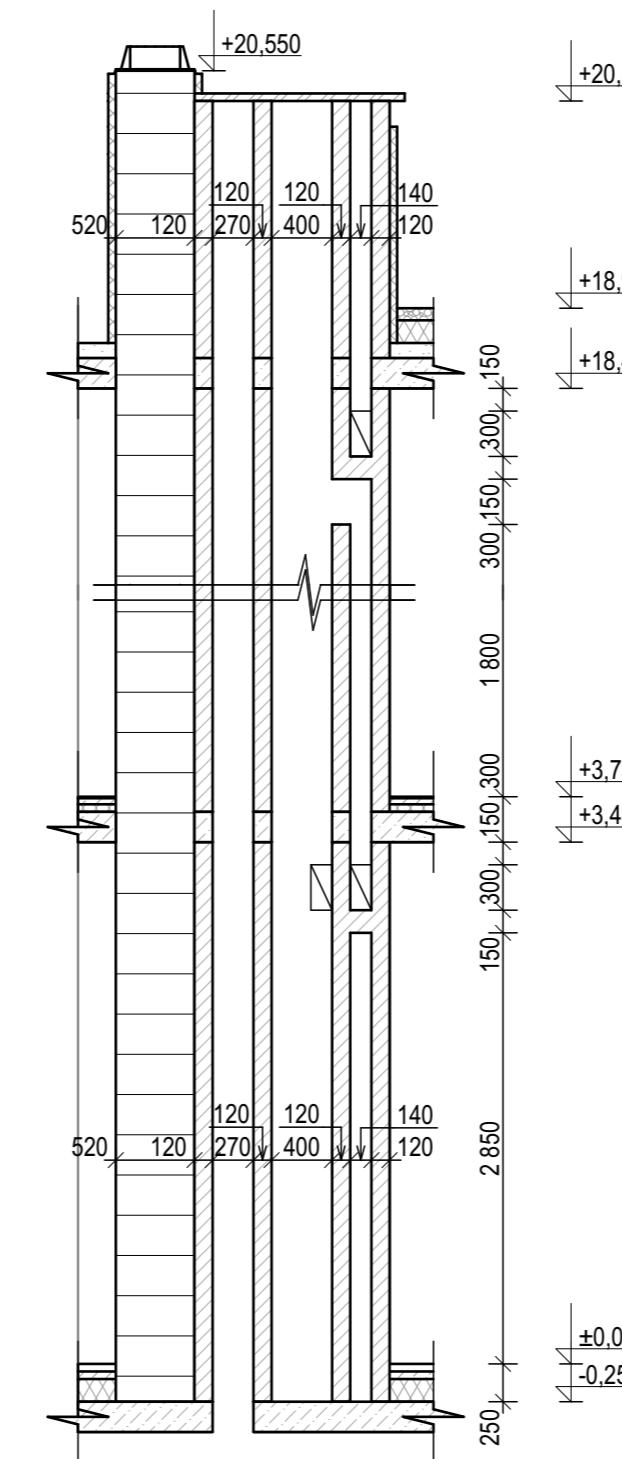

## Розгортка Р-12

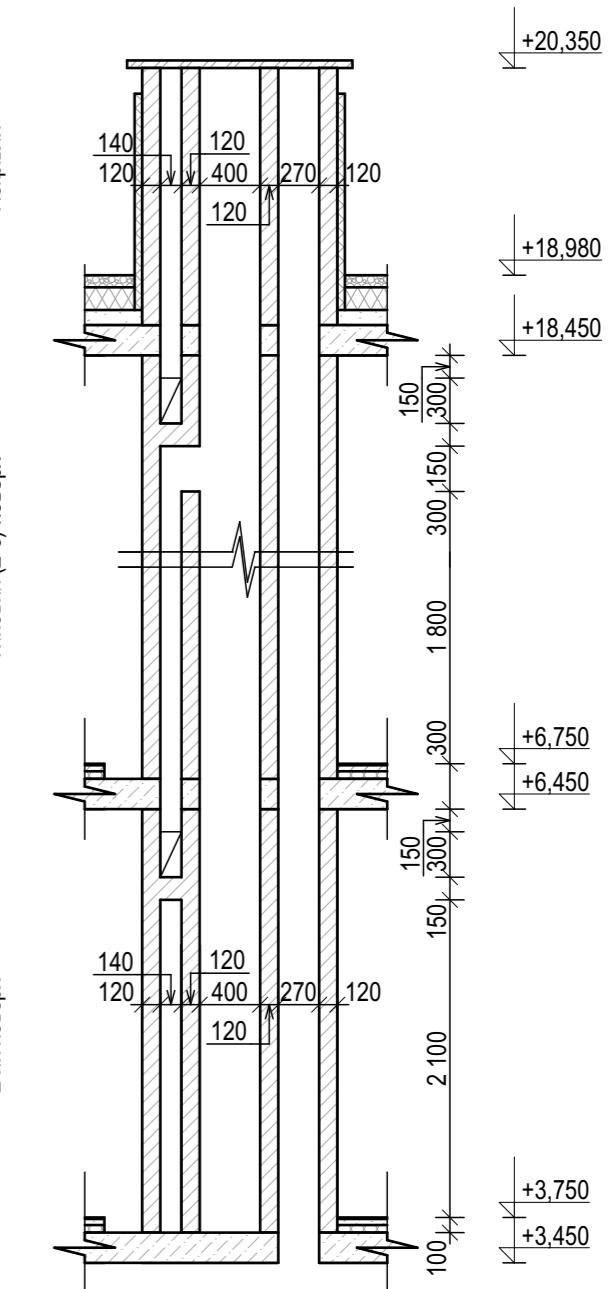


## Примітки


1. Поквартирне опалення опалення здійснюється системою колективного димовидалення. Див. розділ ОВ (Опалення та вентиляція).
  2. Вентиляція приміщень здійснюється через вентиляційні шахти - виконані з керамічної цегли.

|           |        |                |       |   |      |   |                     |
|-----------|--------|----------------|-------|---|------|---|---------------------|
|           |        |                |       |   |      | 04-01/24  | АР                  |
|           |        |                |       |   |      | Нове будівництво багатоквартирного житлового будинку з приміщеннями громадського призначення, за адресою: пл. Авіації, 196, м. Новий Калинів, Самбірський район, Львівська область. |                     |
| змін      | кільк. | аркн.          | №док. | підпис  | дата |   |                     |
| ГП        |        | Зіньків А.Б    |       |  |      | Багатоквартирний житловий будинок<br>м. Новий Калинів, Львівська область.<br>1 черга будівництва.   | стадія              |
| ГАП       |        | Головецький Н. |       |  |      |   | аркуш               |
| Виконав   |        | Попелястий Р.  |       |  |      |   | аркушів             |
| Перевірив |        | Зіньків А.Б    |       |  |      | Розгортка вентиляційних каналів М1:50   | ФОП Никифорець І.І. |


## Розгорта P-13

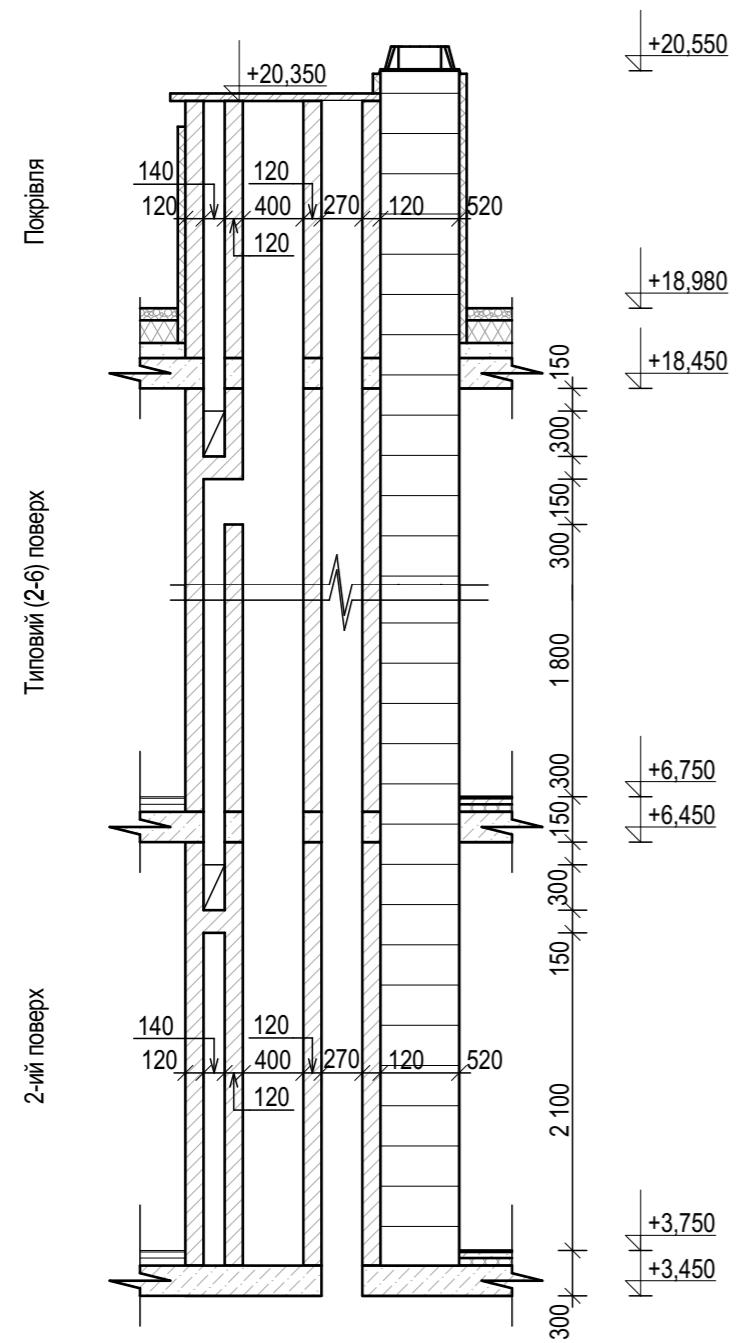

## Розгорта P-14

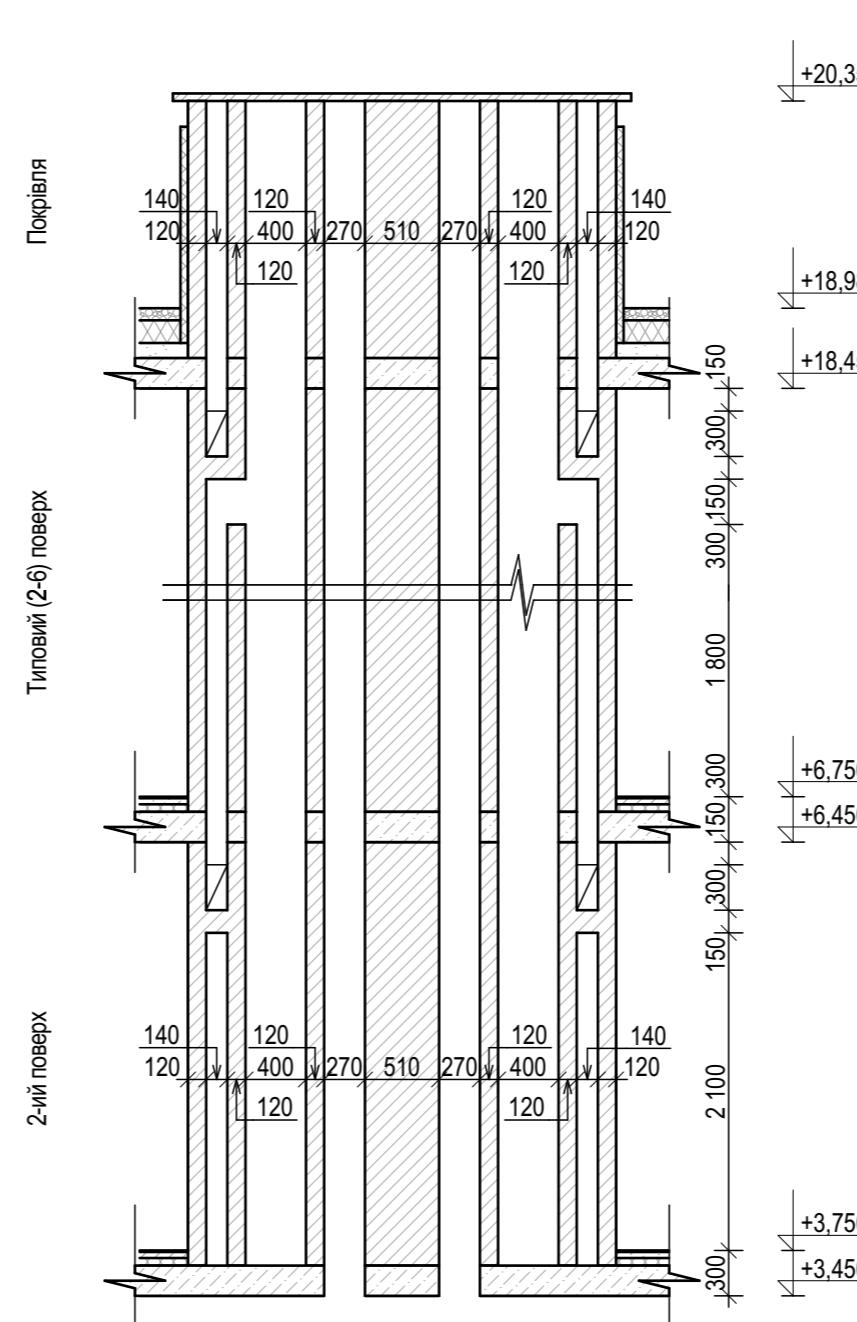

## Розгорта P-15

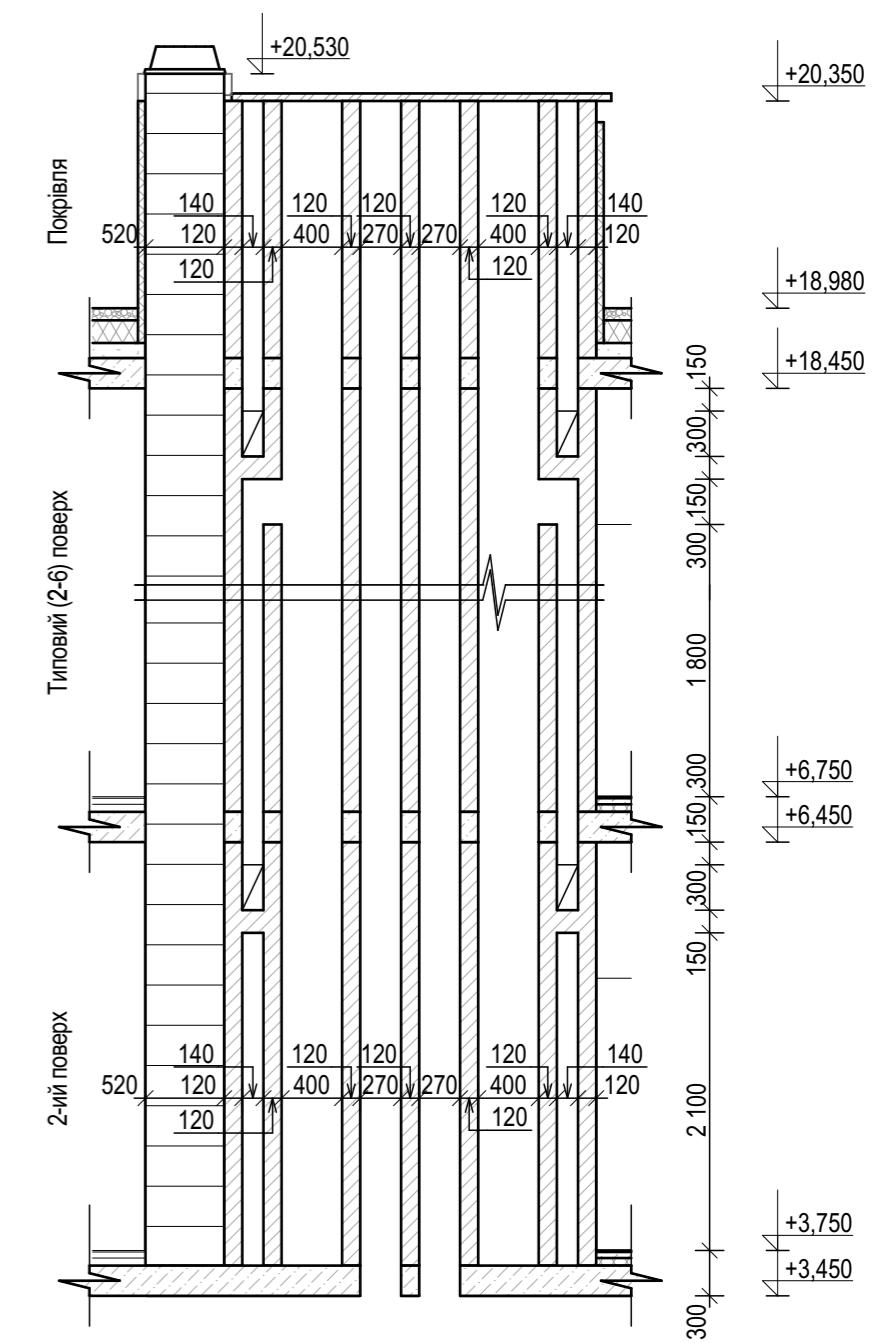


### Примітки:


1. Поквартирне опалення опалення здійснюється системою колективного димовидалення. Див. розділ ОВ (Опалення та вентиляція).
  2. Вентиляція приміщень здійснюється через вентиляційні шахти - виконані з керамічної цегли.

|           |        |                |       |   |  |                     |       |         |
|-----------|--------|----------------|-------|---|--|---------------------|-------|---------|
|           |        |                |       |   | 04-01/24   | АР                  |       |         |
|           |        |                |       |   | Нове будівництво багатоквартирного житлового будинку з приміщеннями громадського призначення, за адресою: пл. Авіації 196, м. Новий Калинів, Самбірський район, Львівська область. |                     |       |         |
| змін      | кільк. | арк.           | №док. | підпис  | дата   |                     |       |         |
| ГП        |        | Зіньків А.Б    |       |  |  |                     |       |         |
| ГАП       |        | Головецький Н. |       |  |  |                     |       |         |
| Виконав   |        | Попелястий Р.  |       |  |  |                     |       |         |
| Перевірив |        | Зіньків А.Б    |       |  |  |                     |       |         |
|           |        |                |       |   | Багатоквартирний житловий будинок<br>м. Новий Калинів, Львівська область.<br>1 черга будівництва.  | стадія              | аркуш | аркушів |
|           |        |                |       |   |  | П                   | 35    |         |
|           |        |                |       |   | Розгортка вентиляційних каналів М1:50  | ФОП Никифорець І.І. |       |         |


## Розгортка Р-16

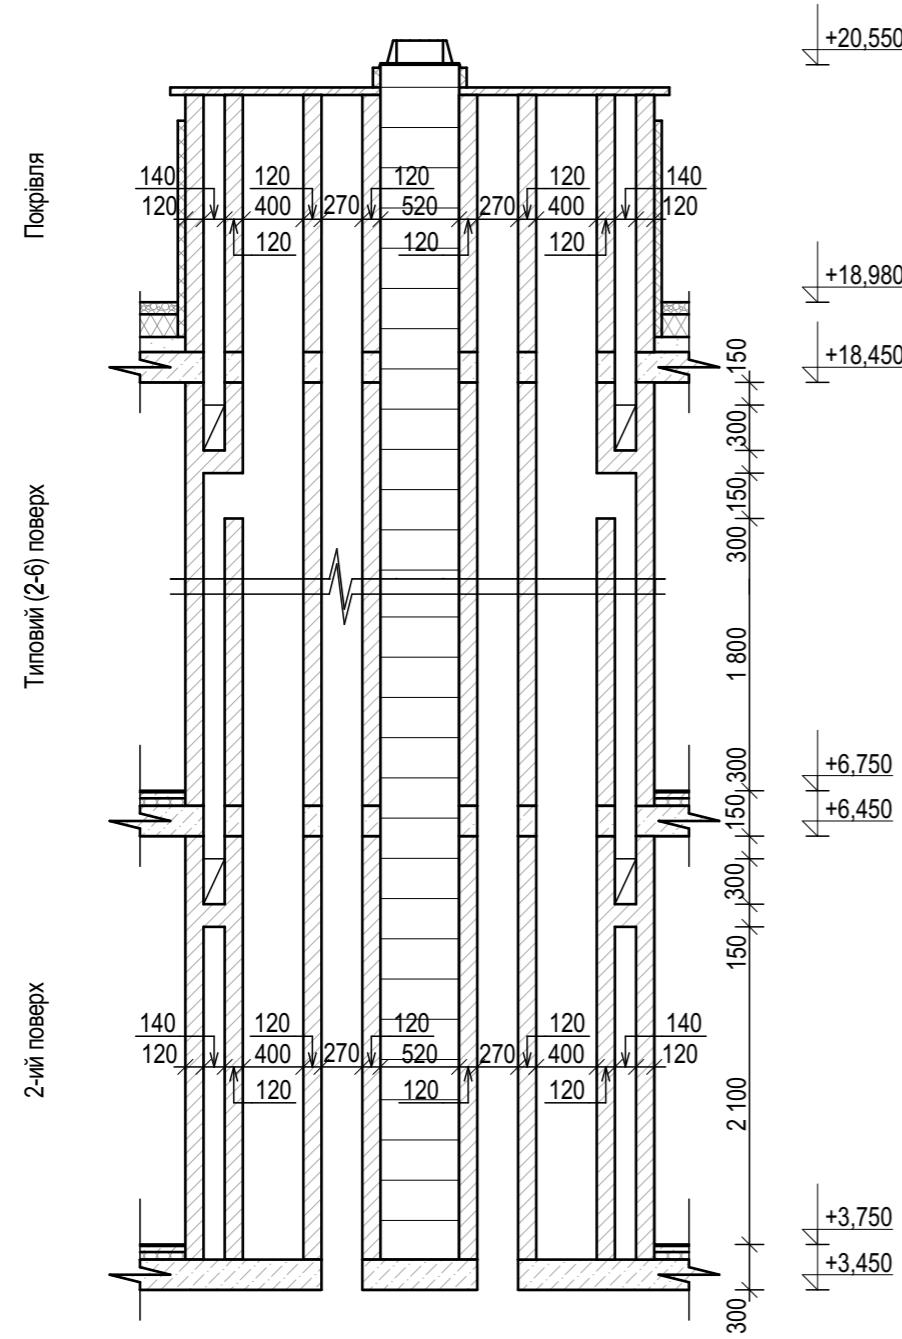

## Розгорта P-17

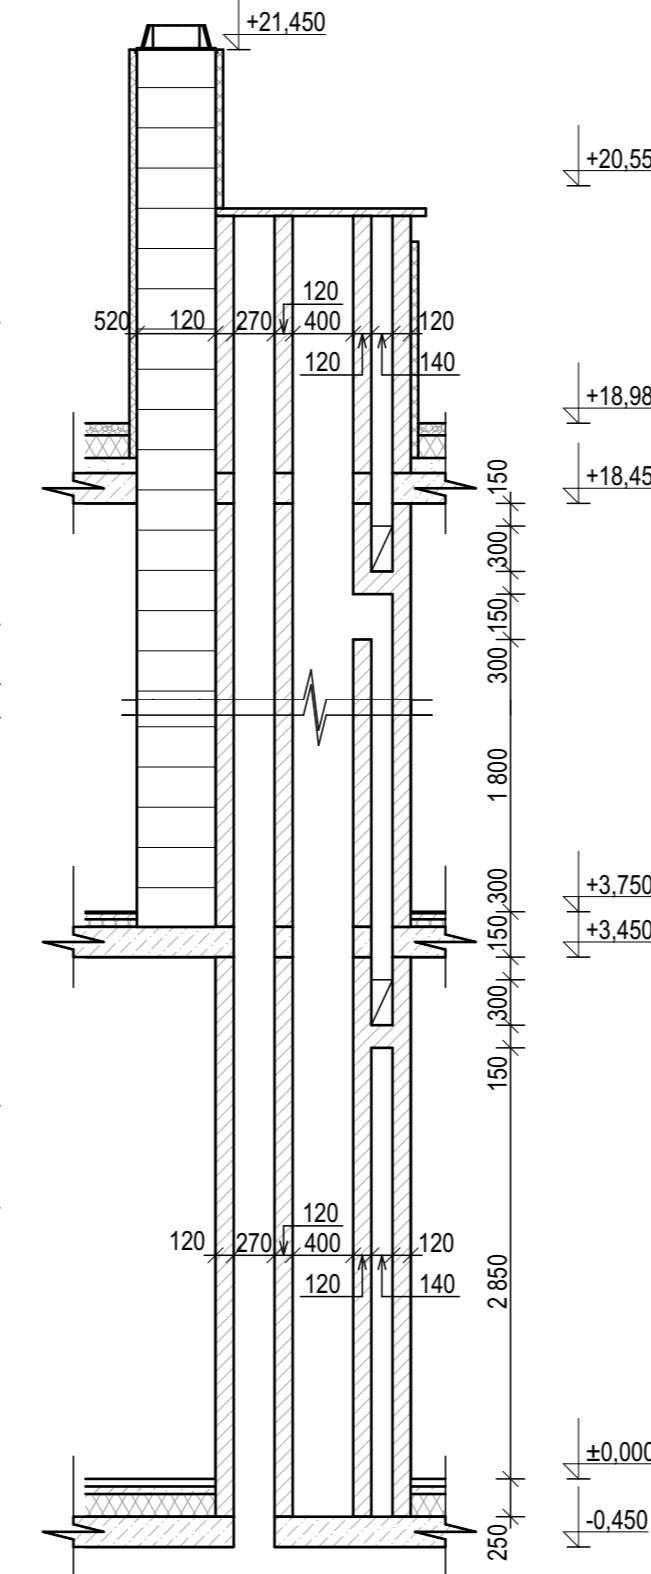

## Розгорта P-18

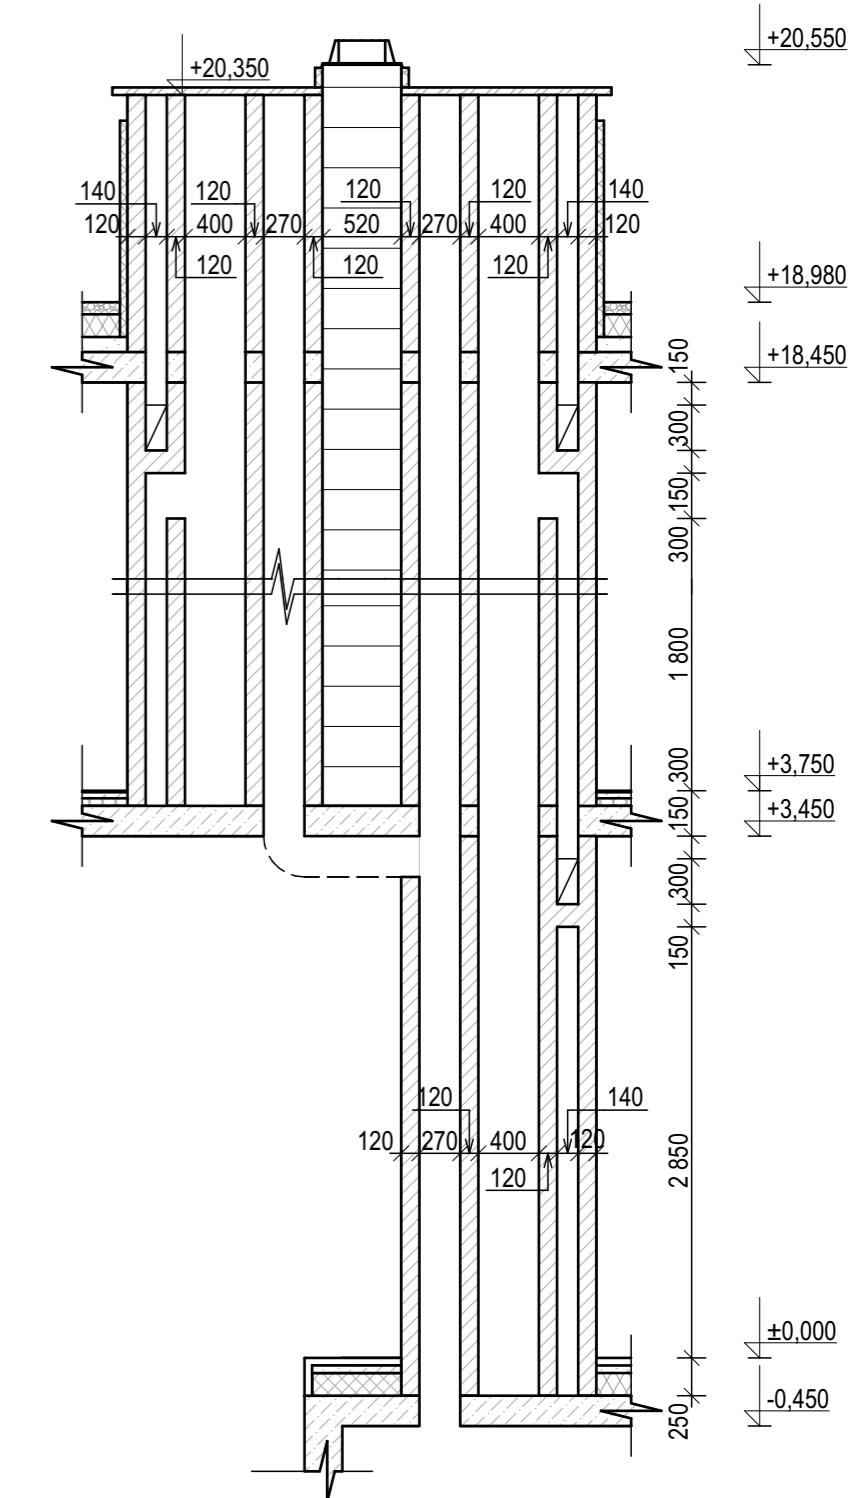

### Примітки:

1. Поквартирне опалення опалення здійснюється системою колективного димовидалення. Див. розділ ОВ (Опалення та вентиляція).
  2. Вентиляція приміщень здійснюється через вентиляційні шахти - виконані з керамічної цегли.

|           |        |                |       |        |   |        |       |                     |
|-----------|--------|----------------|-------|--------|---|--------|-------|---------------------|
|           |        |                |       |        | 04-01/24  | АР     |       |                     |
|           |        |                |       |        | Нове будівництво багатоквартирного житлового будинку з приміщеннями громадського призначення, за адресою: пл. Авіації, 19б, м. Новий Калинів, Самбірський район, Львівська область. |        |       |                     |
| змін      | кільк. | арк.           | №док. | підпис | дата  |        |       |                     |
| ГП        |        | Зіньків А.Б    |       |        | Багатоквартирний житловий будинок<br>м. Новий Калинів, Львівська область.<br>1 черга будівництва.   | стадія | аркуш | аркушів             |
| ГАП       |        | Головецький Н. |       |        |   | П      | 36    |                     |
| Виконав   |        | Попелястий Р.  |       |        |   |        |       |                     |
| Перевірив |        | Зіньків А.Б    |       |        | Розгортка вентиляційних каналів М1:50   |        |       | ФОП Никифорець І.І. |